

7/1/2024 4:26:04 PM

NUMBERED NOTES	
01	INFRASTRUCTURE TO SUPPORT FUTURE PROJECTOR.
02	HALL CALL ELEVATOR CARD READER CONTROL.
03	WALL OUTLET FOR MECHANICAL CONTROLS PANEL.

SHEET NOTES	
A.	REFER TO SHEET T6.01 FOR ABBREVIATIONS, GENERAL NOTES, AND SYMBOL DEFINITIONS.
B.	REFER TO SHEET T6.02 FOR PRIMARY PATHWAY REQUIREMENTS AND DEFINITIONS.
C.	REFER TO SHEET T6.03 AND T6.04 FOR OUTLETS/DEVICES SECONDARY PATHWAY AND CABLING REQUIREMENTS.
D.	SERVE OUTLETS/DEVICES ON THIS SHEET FROM TELECOM ROOMS AS NOTED.
E.	REFER TO SECURITY INSTALLATION DETAILS FOR SECONDARY PATHWAY REQUIREMENTS, SYSTEM INTERFACES, AND COMPONENT CONFIGURATIONS.
F.	INSTALL SECONDARY PATHWAYS ALONG THE MOST DIRECT ROUTES TO PRIMARY PATHWAYS OR SERVING ROOM.
G.	INSTALL HORIZONTAL CABLES ALONG THE MOST DIRECT PRIMARY PATHWAY ROUTE TO THE SERVING TELECOM ROOM.
H.	PROVIDE APPROVED FIRESTOP SYSTEMS AT PENETRATIONS THROUGH FIRE BARRIERS, SMOKE BARRIERS, AND SMOKE PARTITIONS TO MAINTAIN RATINGS.



STAMP



DB STAMP


DATE	BY	DATE	BY
06/15/2024			

ST. IGNATIUS COLLEGE PREPARATORY

2001 37th Ave. San Francisco, CA 94116

CAMERA SYSTEM RISER DIAGRAM

T6.07

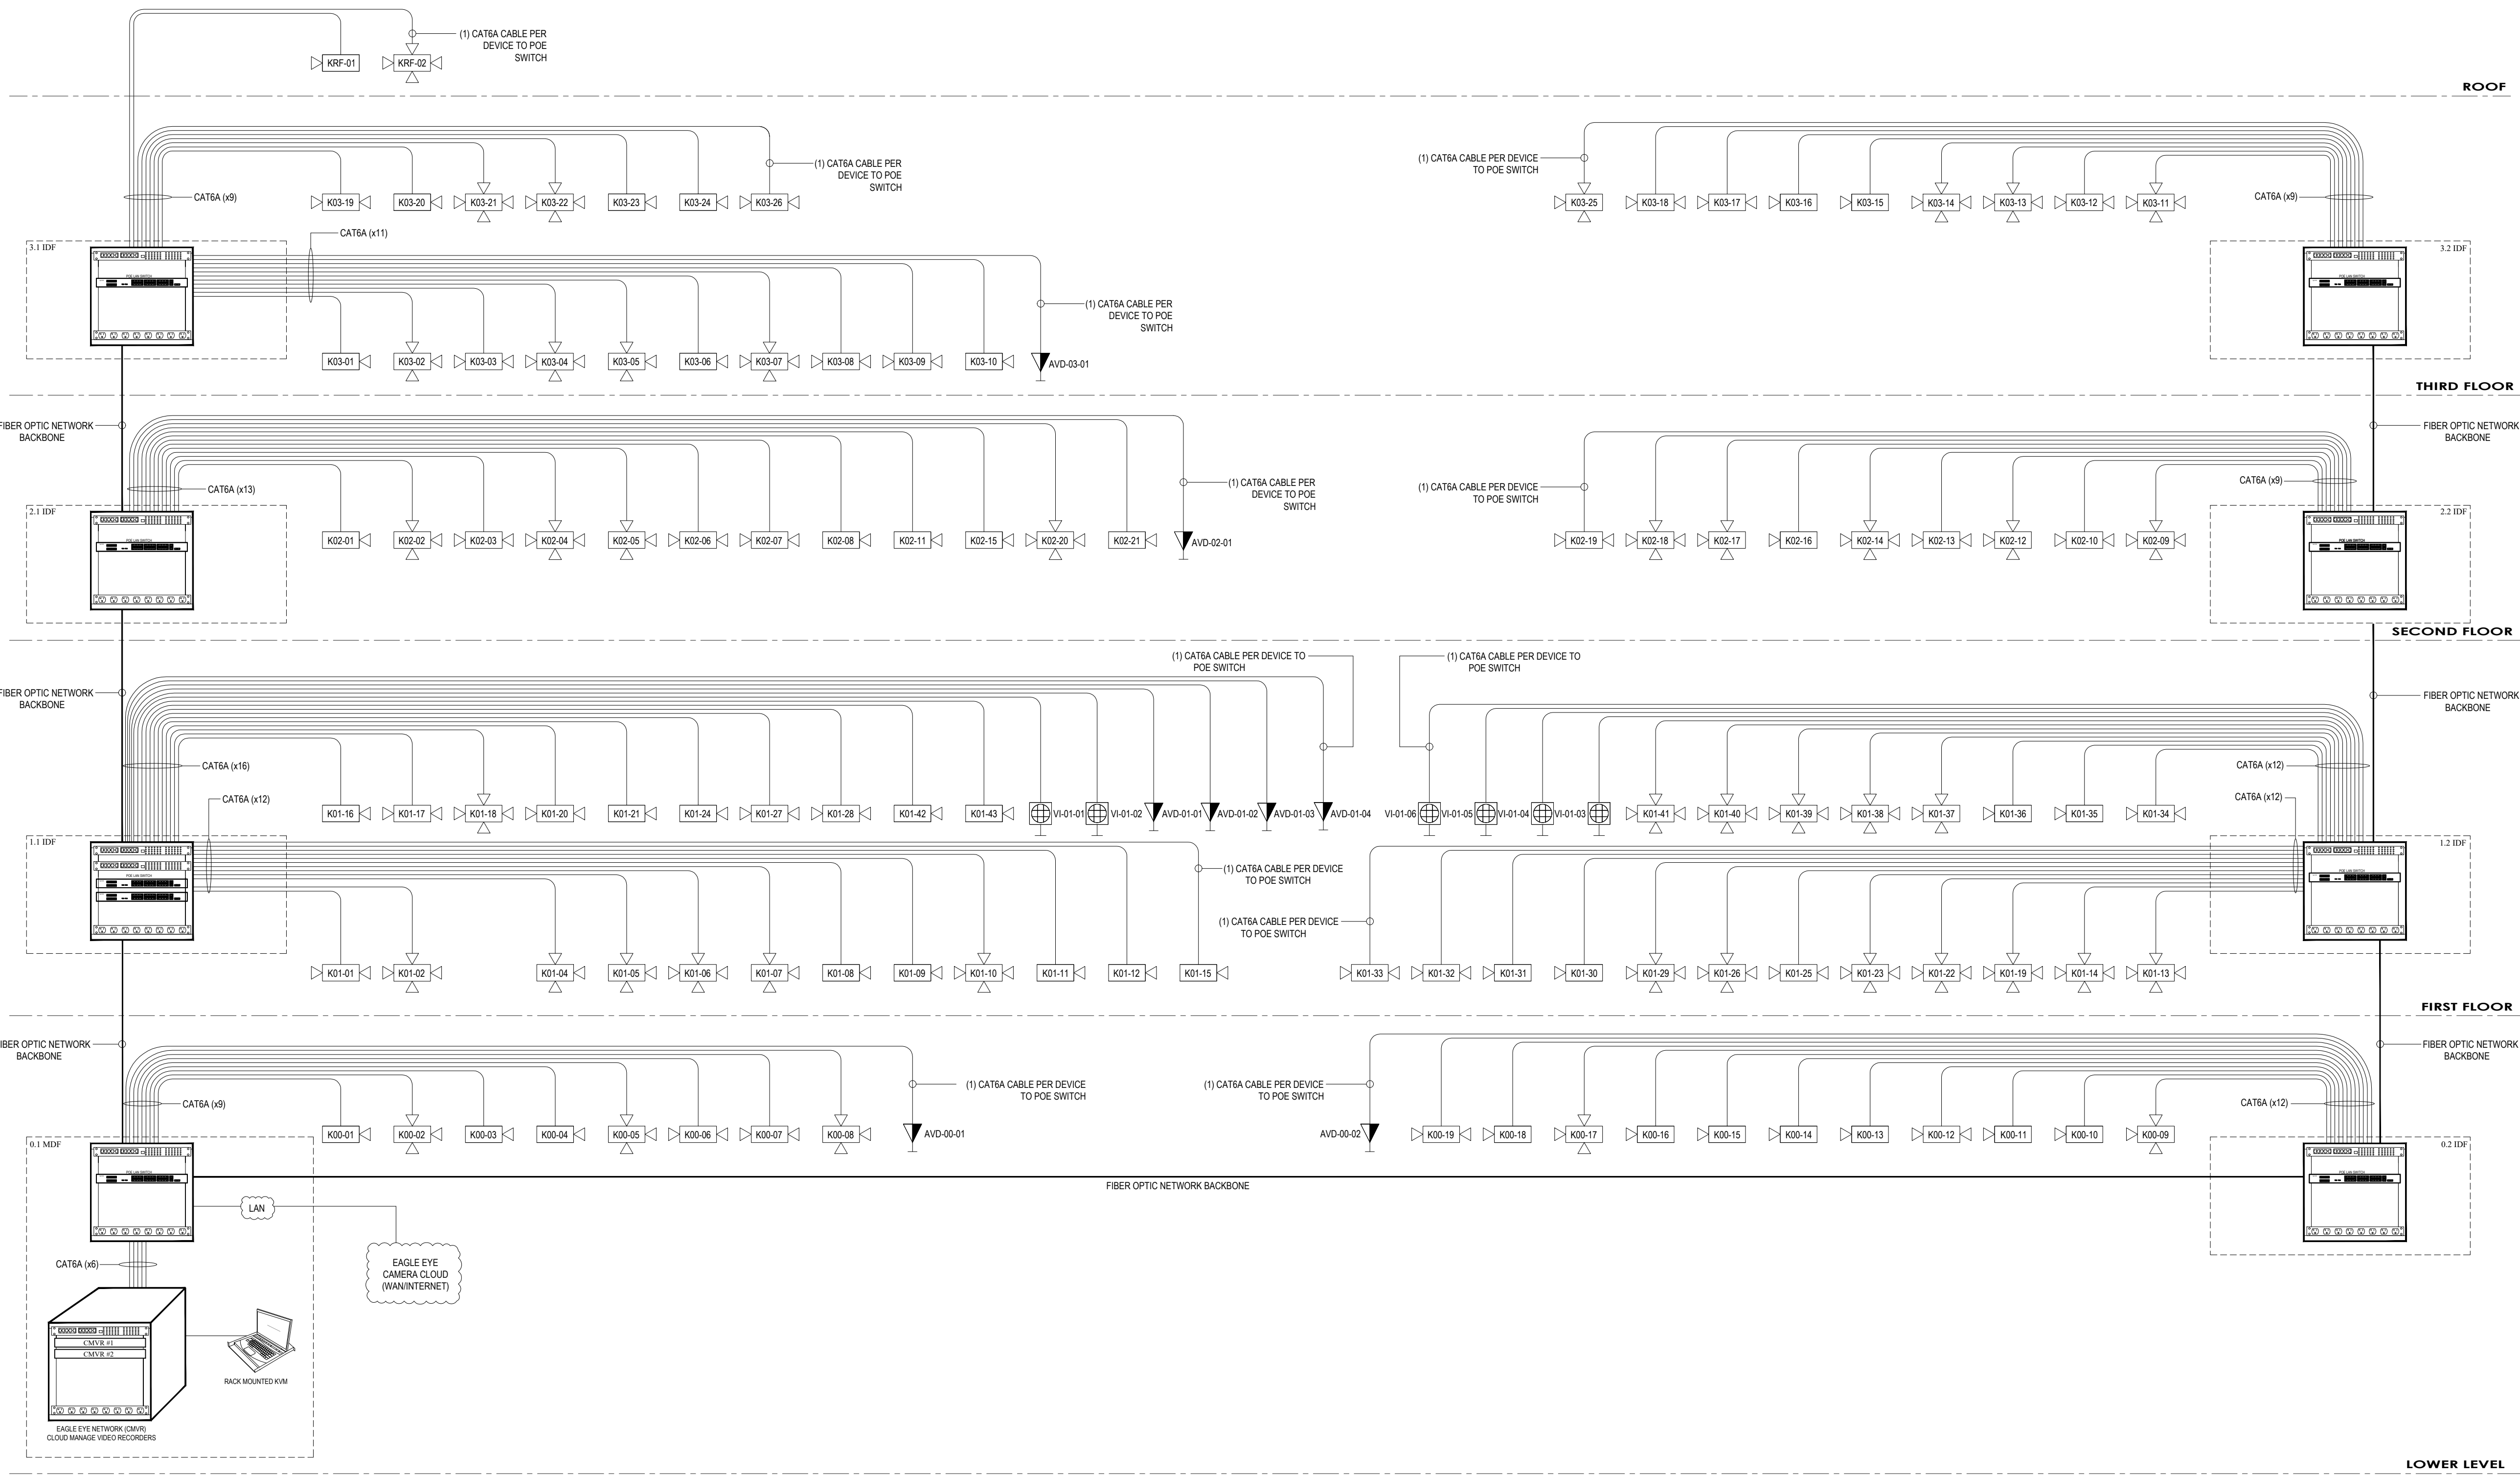

A CAMERA SYSTEM RISER DIAGRAM
SCALE: N.T.S.