


1.2 IDF LEVEL ONE NORTH

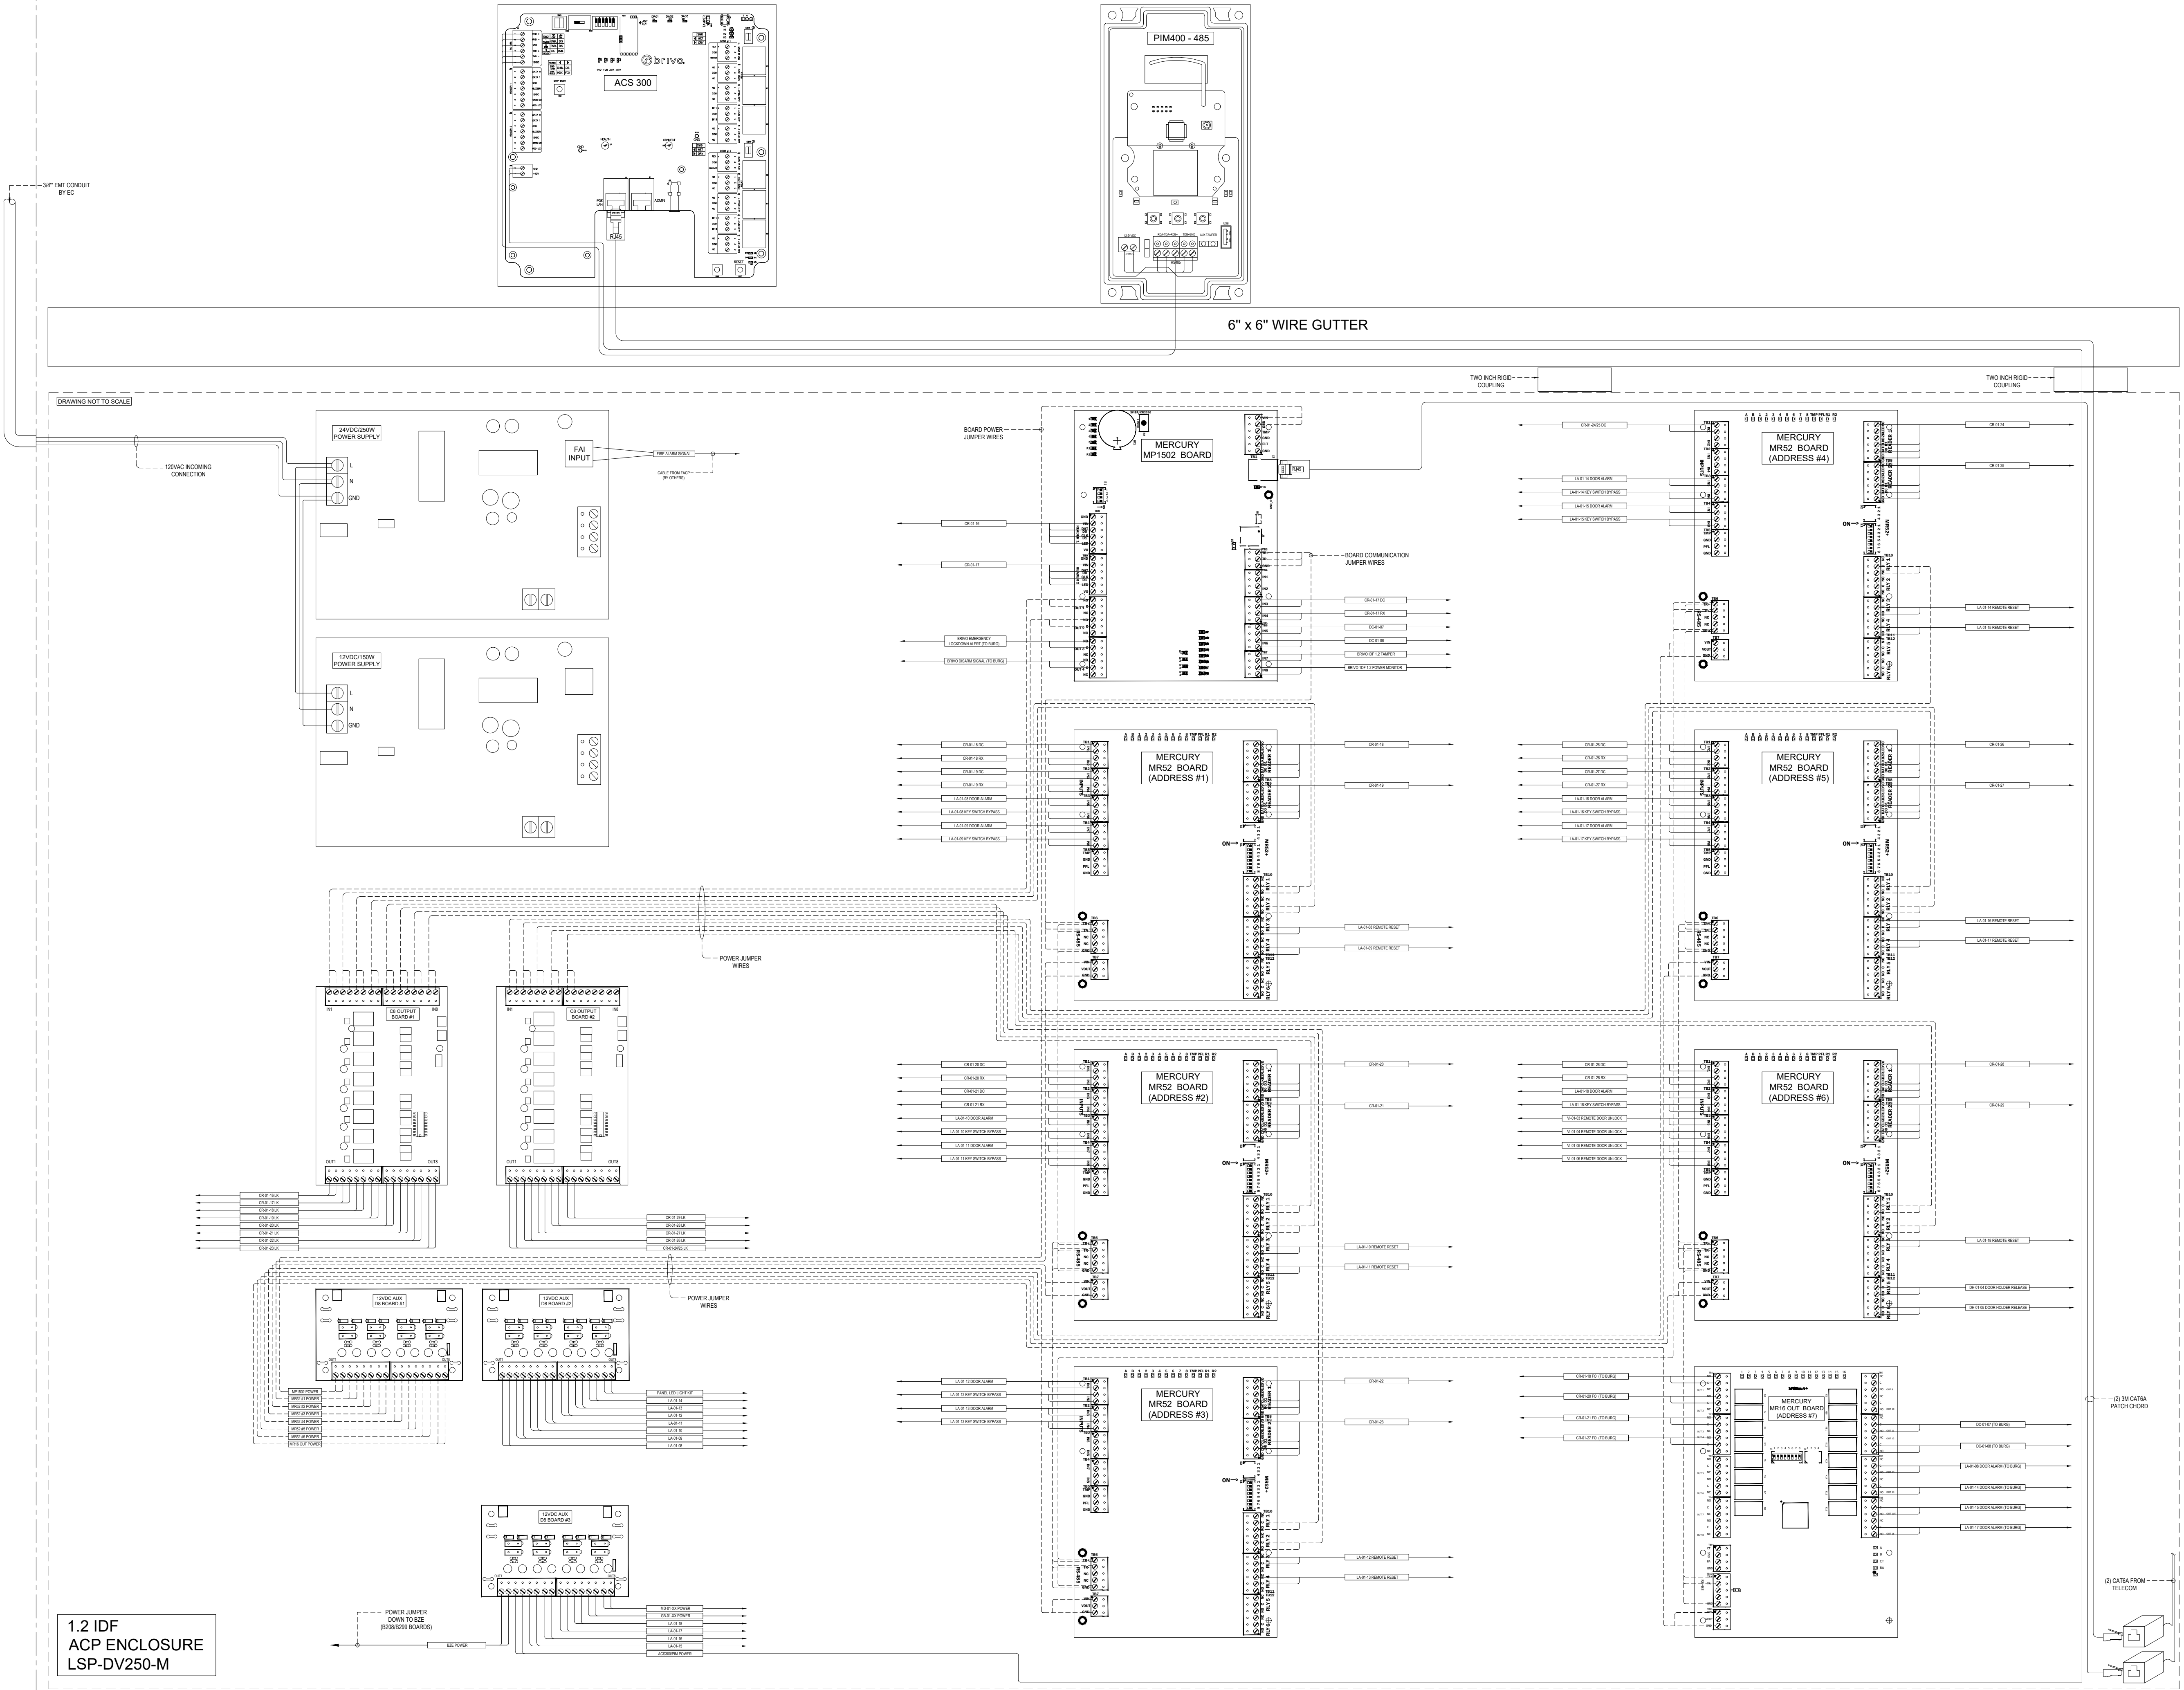

1.2 IDF
ACP ENCLOSURE
LSP-DV250-M



ST. IGNATIUS COLLEGE PREPARATORY

2001 37th Ave. San Francisco, CA 94116

ACCESS CONTROL SYSTEM POINT TO POINT DIAGRAM

T6.17D

STAMP

COMPLIANT LOGO

TEECOM

10 California Street
Suite 100
San Francisco, CA 94111
(415) 397-1800
www.teecom.com

DBI STAMP

REV. DATE DESCRIPTION

NO. 10/20/2025 DYNAMIC SECURITY PLANS