


2.1 IDF LEVEL TWO SOUTH

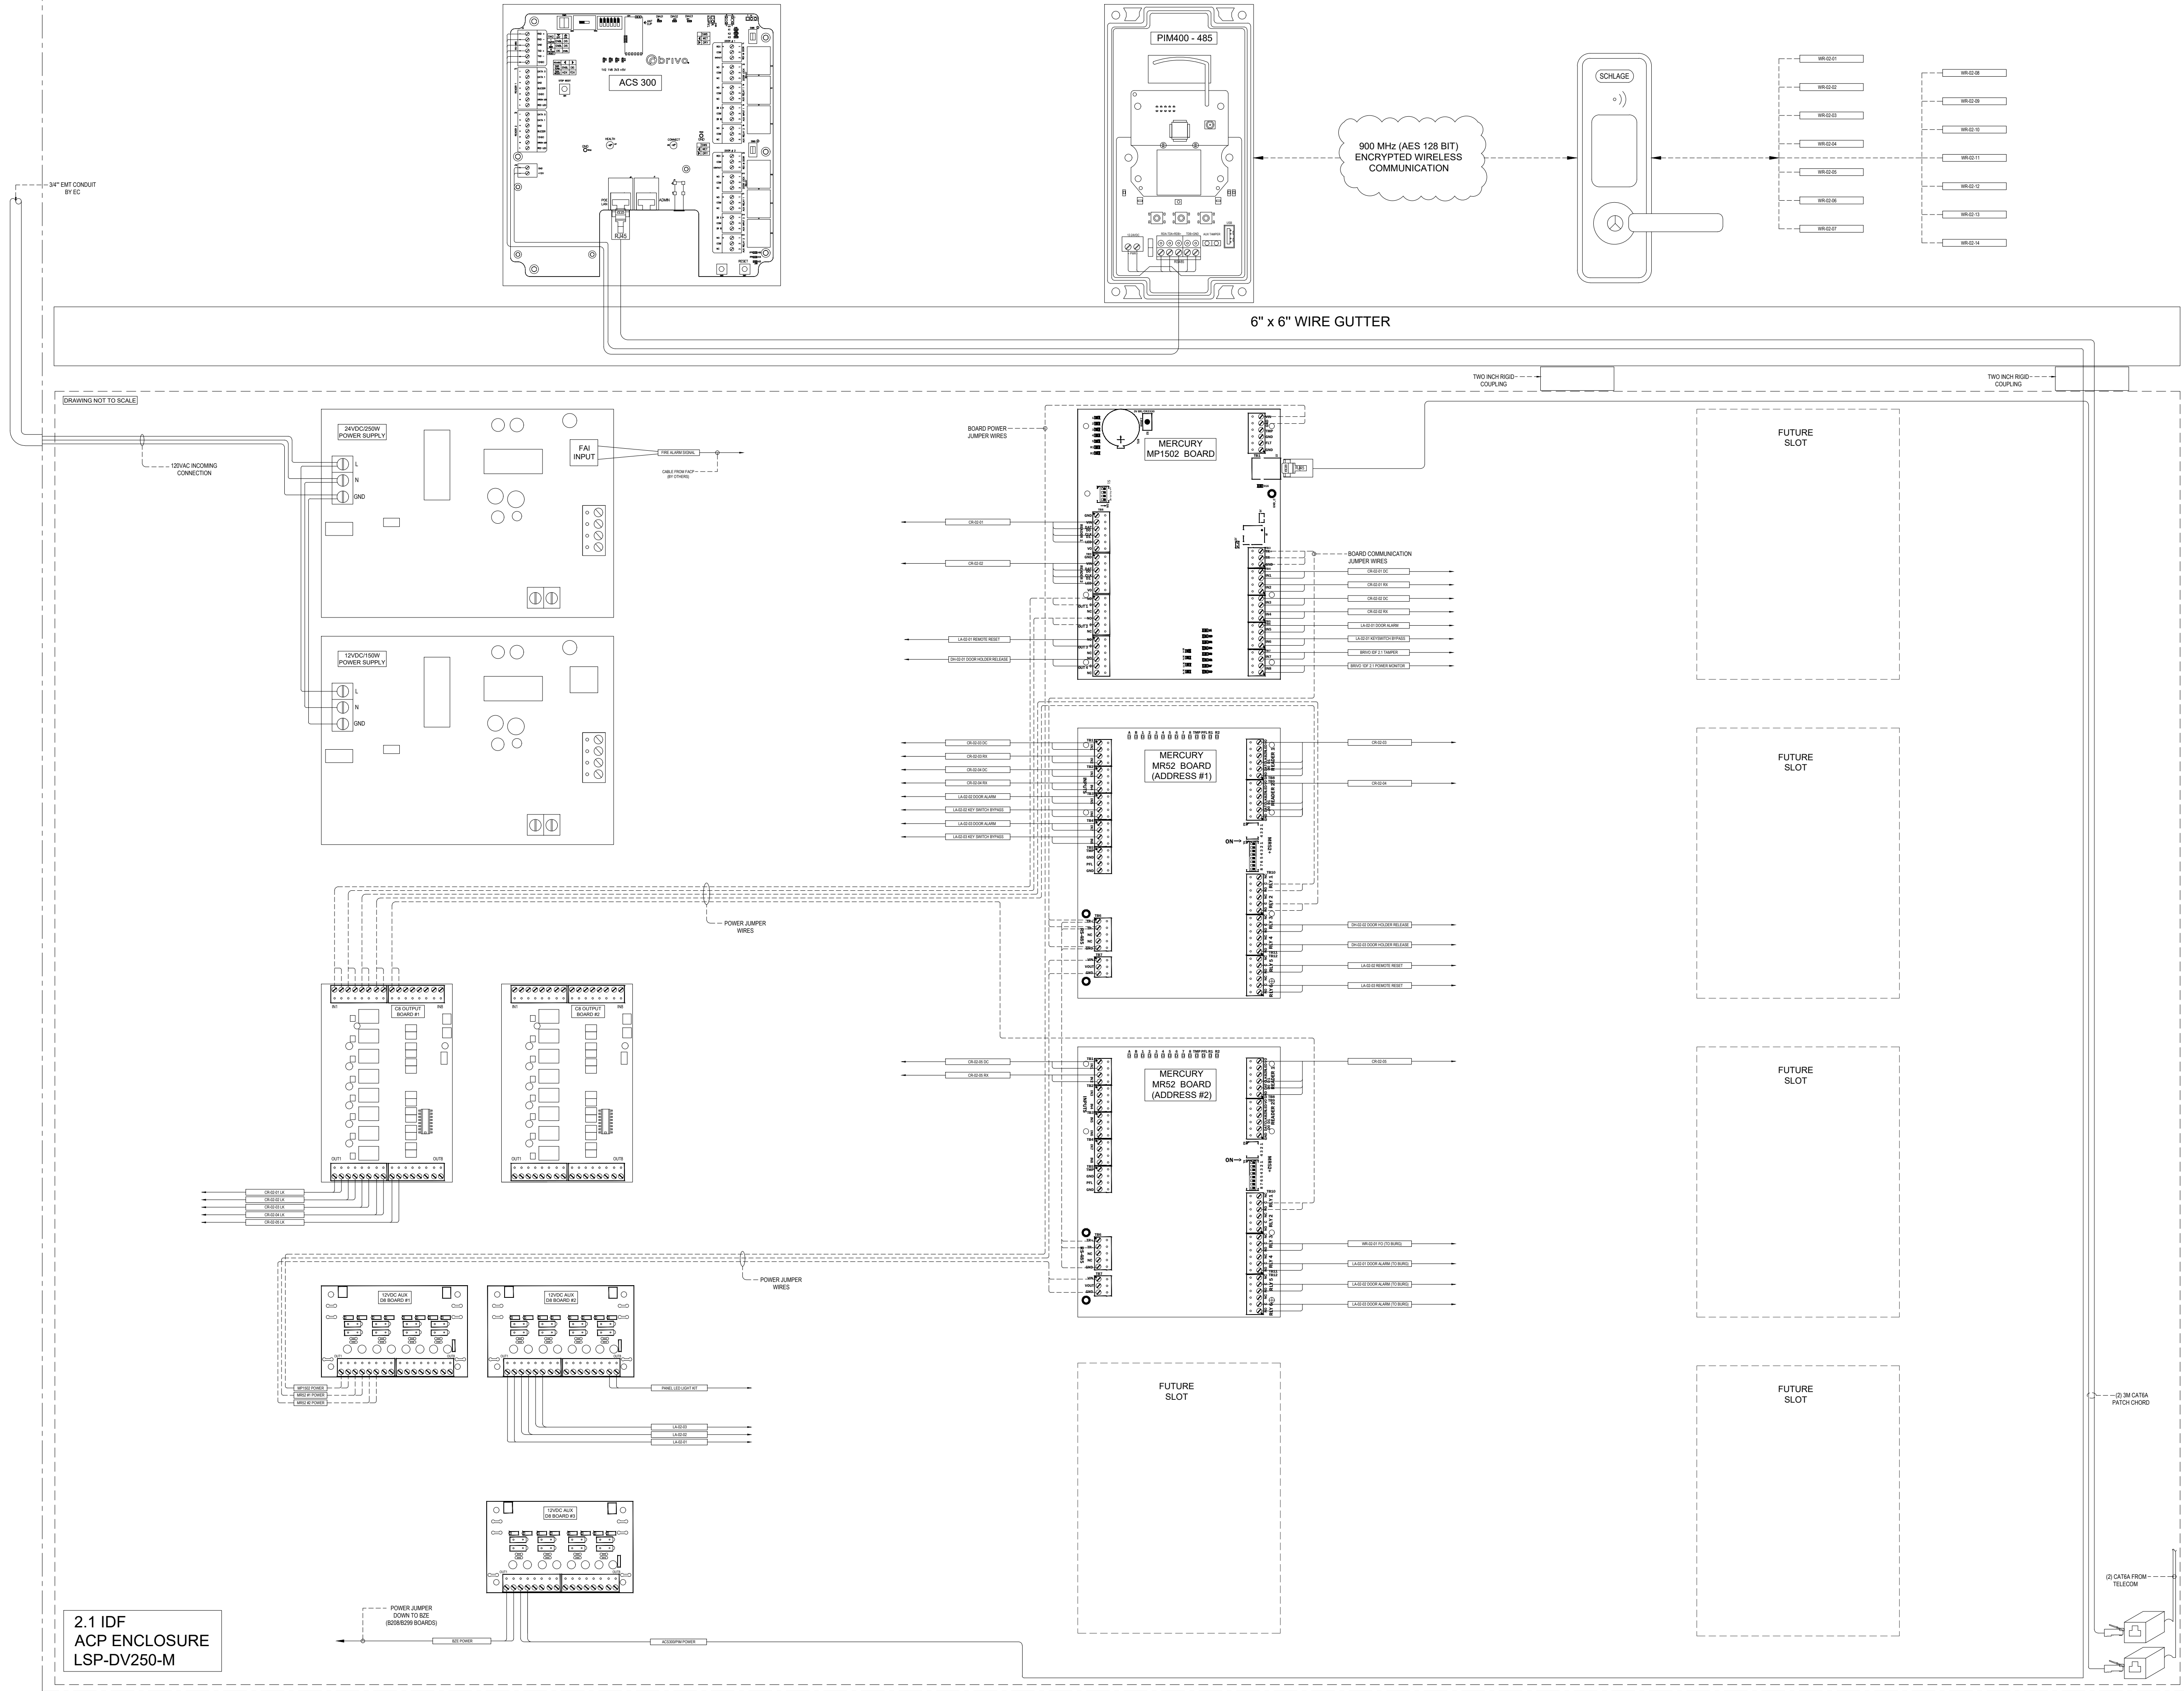



ST. IGNATIUS COLLEGE PREPARATORY

STAMP

CONSULTANT LOGO



TEECOM

50 California Street  
Suite 100  
San Francisco, CA 94111  
(415) 397-1800  
www.teecom.com

DBI STAMP

| REV | DATE       | DESCRIPTION            |
|-----|------------|------------------------|
| 1   | 01/10/2025 | DYNAMIC SECURITY PLANS |

ACCESS CONTROL SYSTEM POINT TO POINT DIAGRAM

T6.17E