


7/1/2026 4:26:04 PM

2.2 IDF LEVEL TWO NORTH

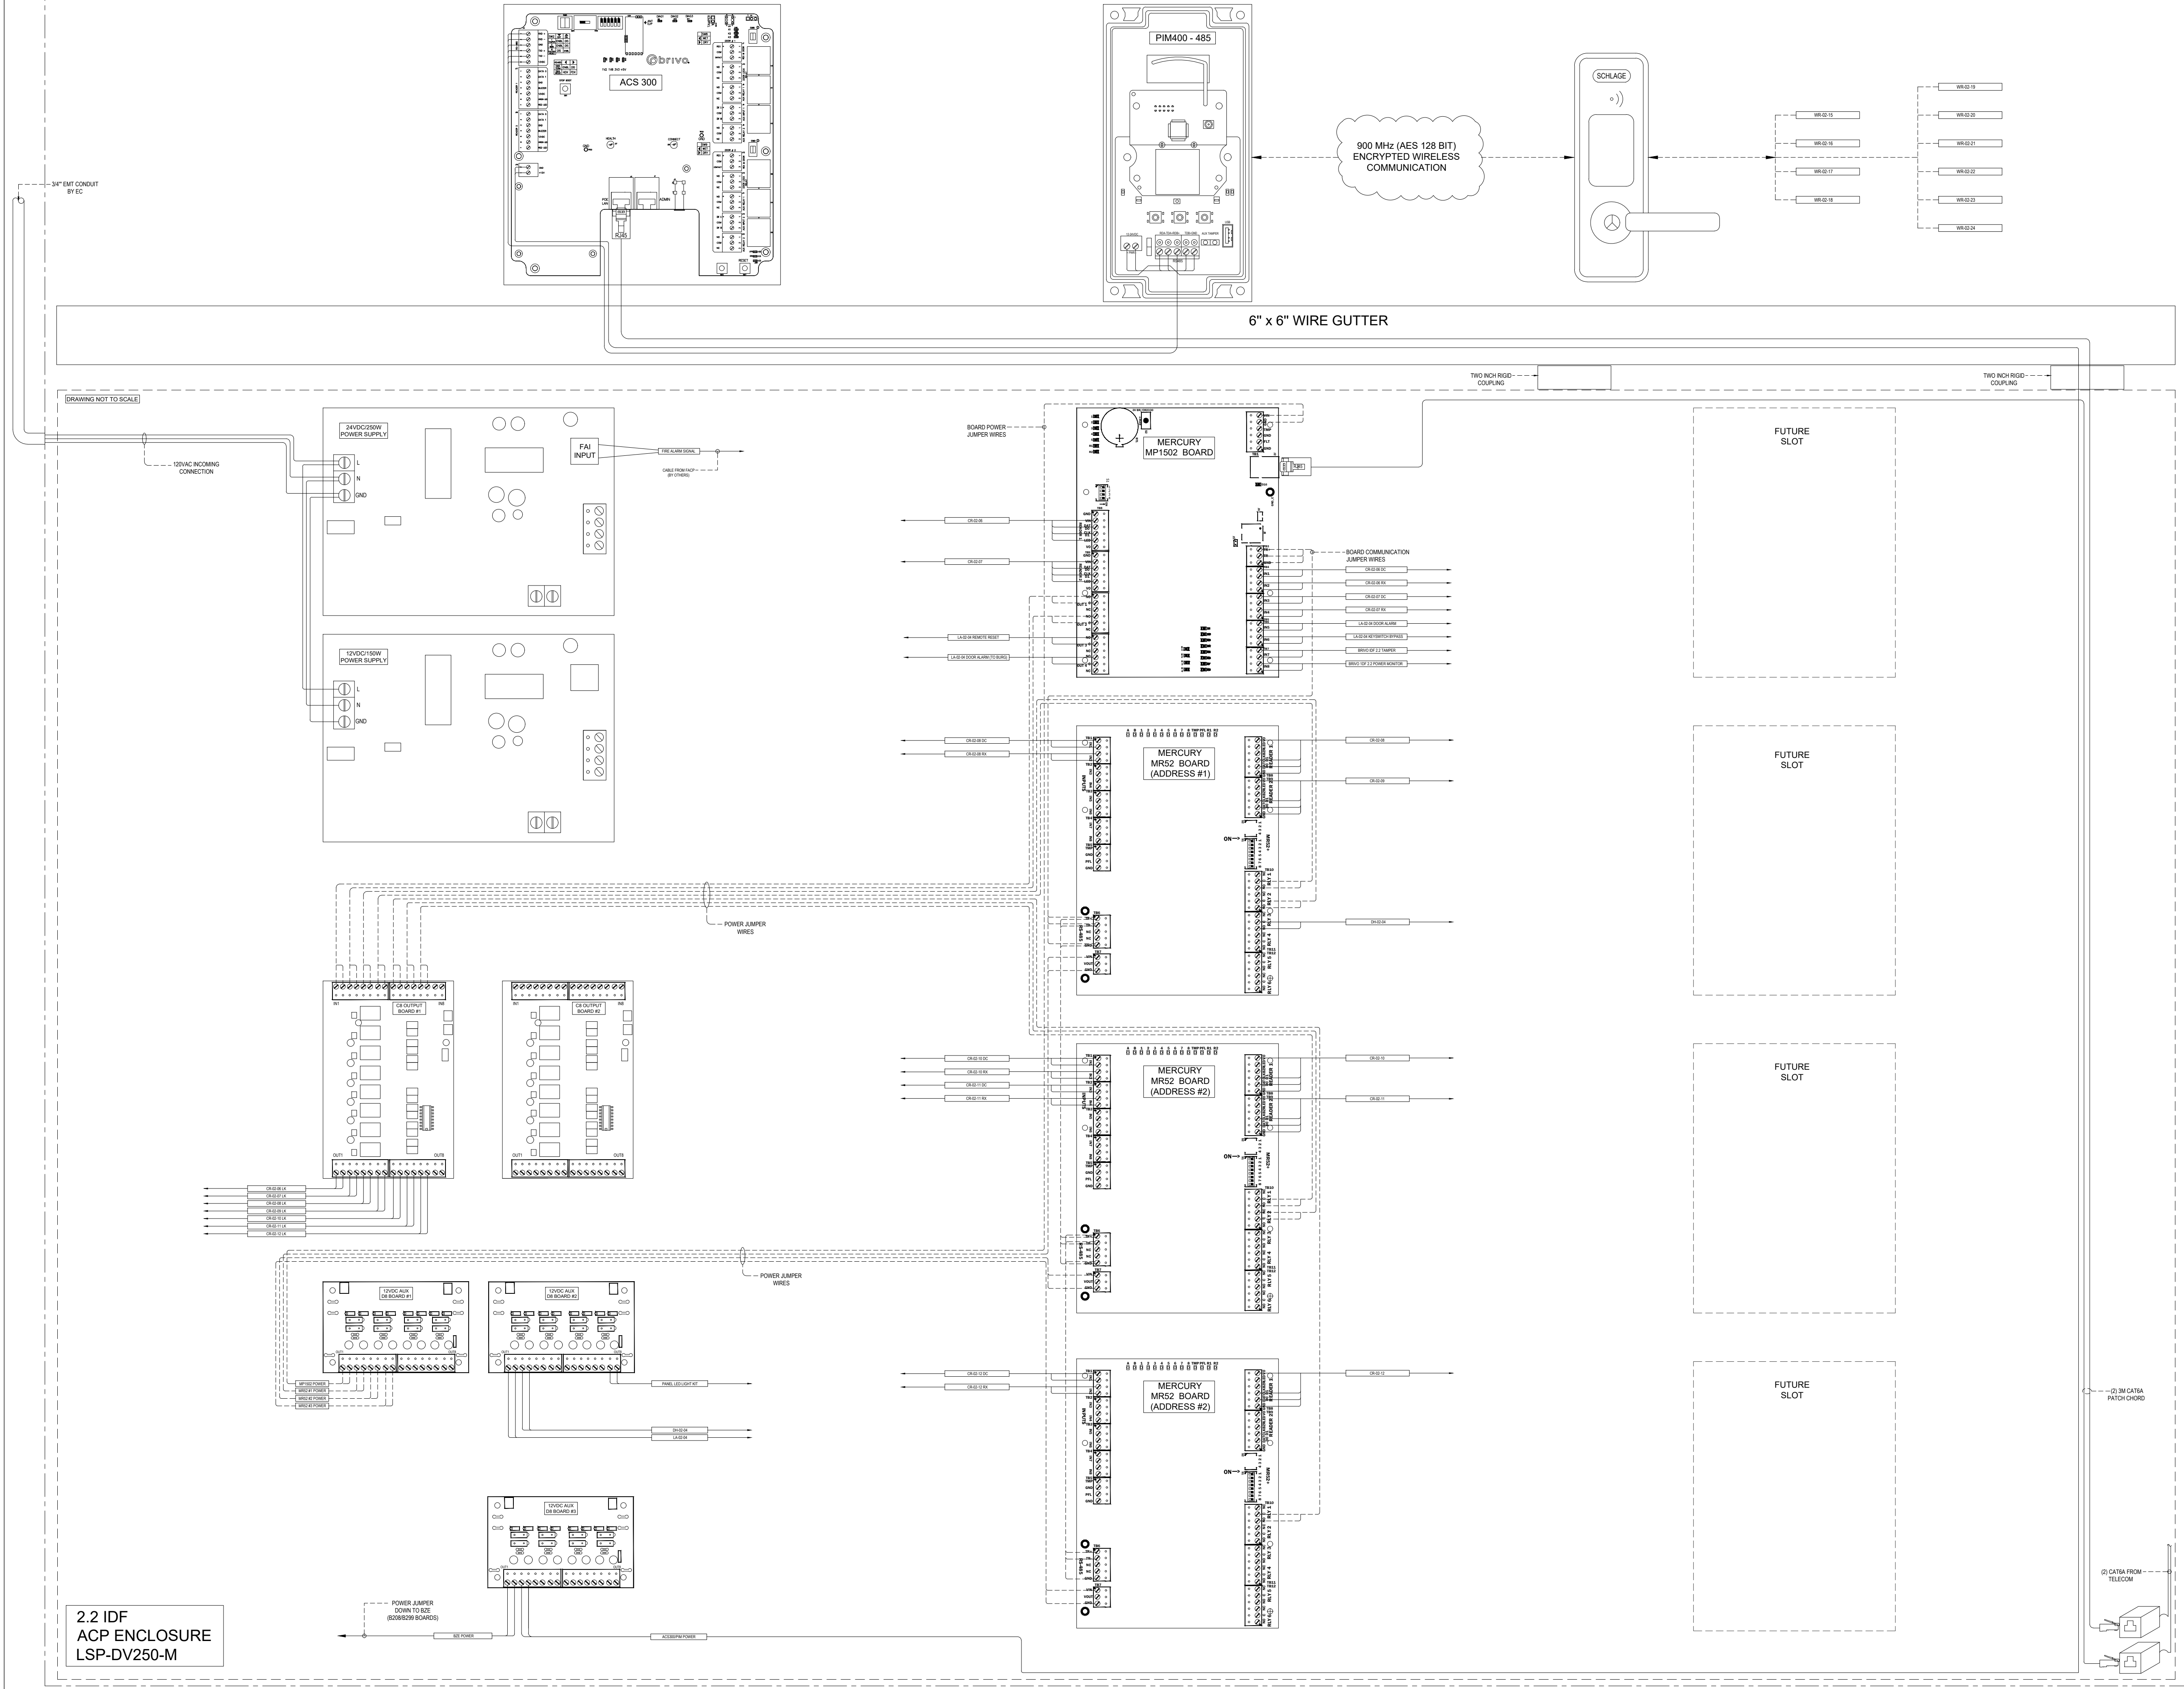

2.2 IDF
ACP ENCLOSURE
LSP-DV250-M



ST. IGNATIUS COLLEGE PREPARATORY

2001 37th Ave. San Francisco, CA 94116

STAMP

TEECOM

30 California Street
Suite 100
San Francisco, CA 94111
(415) 397-8888
www.teecom.com

DBI STAMP

REV	DATE	DESCRIPTION
1	03/20/25	DYNAMIC SECURITY PLANS

ACCESS CONTROL SYSTEM POINT TO POINT DIAGRAM

T6.17F