


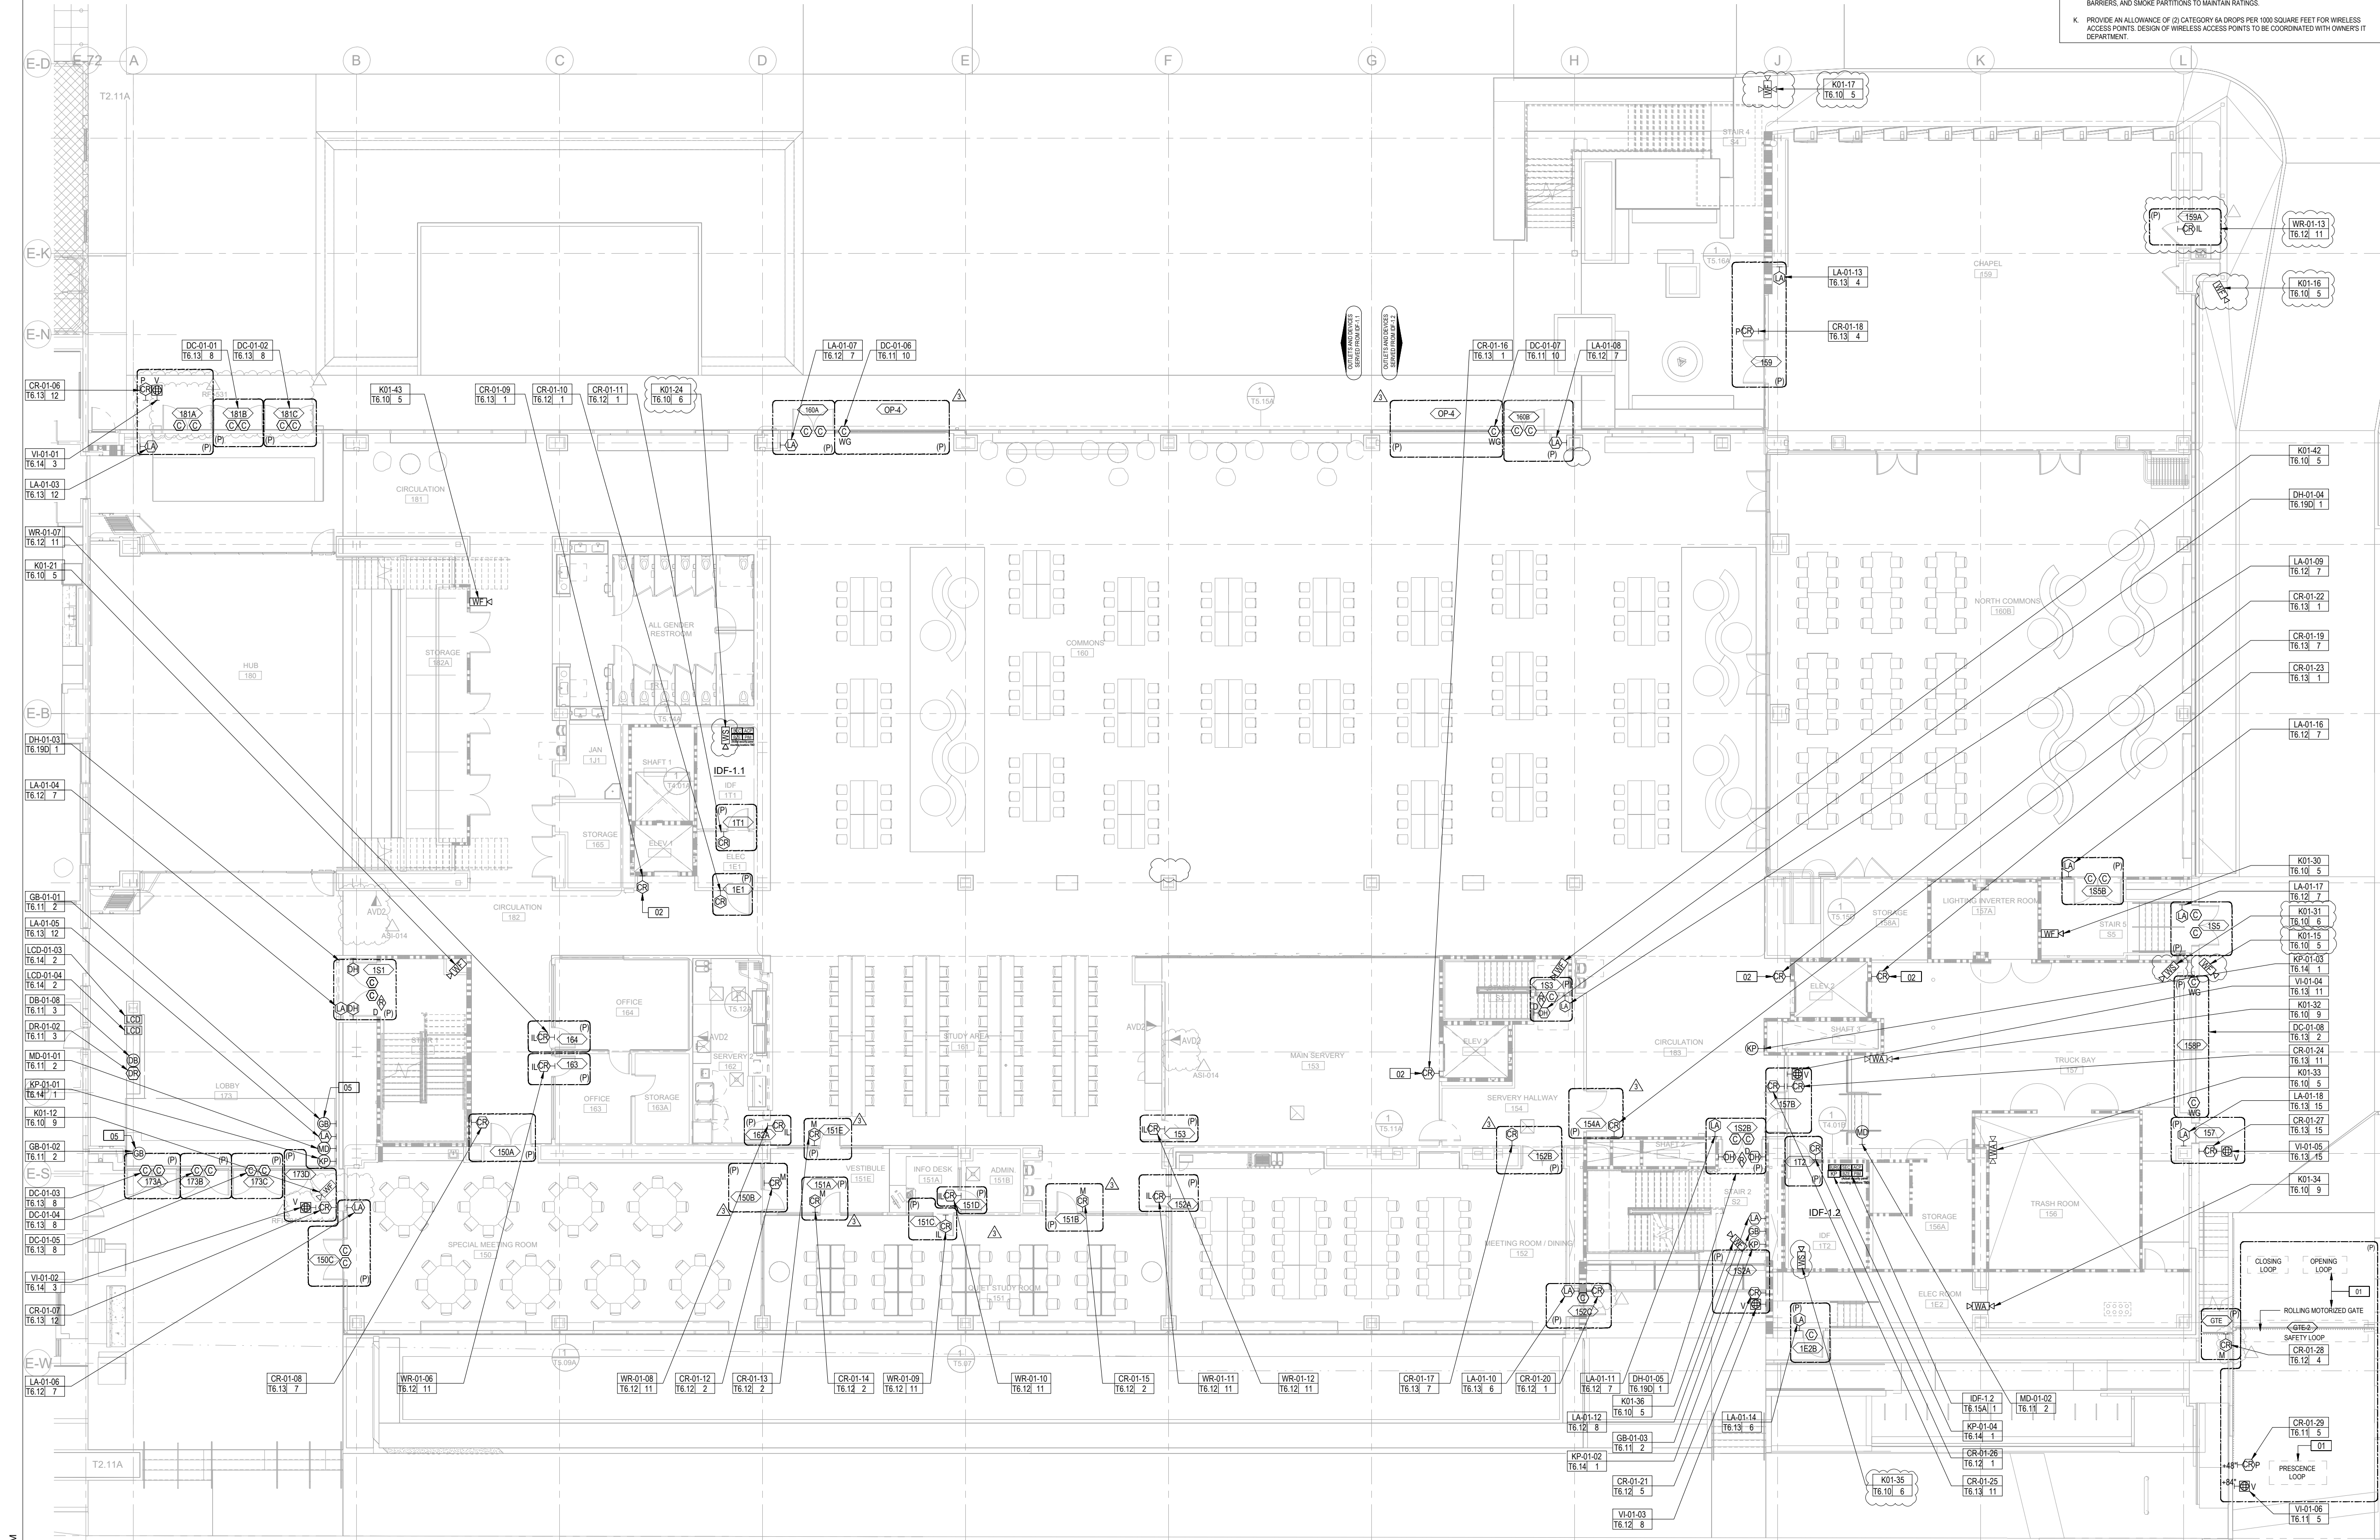

NUMBERED NOTES

- 01 GATE OPERATOR AND LOOPS SHOWN FOR REFERENCE ONLY. PROVIDED BY GC
- 02 HALL CALL ELEVATOR CARD READER CONTROL
- 03 WALL OUTLET FOR MECHANICAL CONTROLS PANEL
- 04 FLOOR OUTLET FOR POINT OF SALE MACHINES
- 05 WALL MOUNT GLASS BREAK SENSOR 12" AFF IN LINE WITH WALL OUTLETS

SHEET NOTES

- A. REFER TO SHEET T2.01 FOR ABBREVIATIONS, GENERAL NOTES, AND SYMBOL DEFINITIONS.
- B. REFER TO SHEET T2.02 FOR PRIMARY PATHWAY REQUIREMENTS AND DEFINITIONS.
- C. REFER TO SHEET T2.03 AND T2.04 FOR OUTLETS/DEVICES SECONDARY PATHWAY AND CABLING REQUIREMENTS
- D. SERVE OUTLETS/DEVICES ON THIS SHEET FROM TELECOM ROOMS AS NOTED.
- E. REFER TO ARCHITECTURAL PLANS FOR EXACT LOCATIONS OF OUTLETS/DEVICES, WHERE SHOWN. OUTLETS/DEVICES ON THIS SHEET ARE SHOWN DIAGRAMMATICALLY.
- F. REFER TO SECURITY INSTALLATION DETAILS FOR SECONDARY PATHWAY REQUIREMENTS, SYSTEM INTERFACES, AND COMPONENT CONFIGURATIONS.
- G. PATHWAYS SHOWN ARE DEDICATED FOR TECHNOLOGY CABLING.
- H. INSTALL SECONDARY PATHWAYS ALONG THE MOST DIRECT ROUTES TO PRIMARY PATHWAYS OR SERVING ROOM.
- I. INSTALL HORIZONTAL CABLES ALONG THE MOST DIRECT PRIMARY PATHWAY ROUTE TO THE SERVING TELECOM ROOM.
- J. PROVIDE APPROVED FIRESTOP SYSTEMS AT PENETRATIONS THROUGH FIRE BARRIERS, SMOKE BARRIERS, AND SMOKE PARTITIONS TO MAINTAIN RATINGS.
- K. PROVIDE AN ALLOWANCE OF (2) CATEGORY 6A DROPS PER 1000 SQUARE FEET FOR WIRELESS ACCESS POINTS. DESIGN OF WIRELESS ACCESS POINTS TO BE COORDINATED WITH OWNER'S IT DEPARTMENT.



REV	DATE	DESCRIPTION	DESIGNED BY	CHECKED BY	DATE
1	07/01/2024	ISSUED FOR CONSTRUCTION	J. L. LEE	J. L. LEE	07/01/2024
2	07/01/2024	ISSUED FOR CONSTRUCTION	J. L. LEE	J. L. LEE	07/01/2024
3	07/01/2024	ISSUED FOR CONSTRUCTION	J. L. LEE	J. L. LEE	07/01/2024
4	07/01/2024	ISSUED FOR CONSTRUCTION	J. L. LEE	J. L. LEE	07/01/2024
5	07/01/2024	ISSUED FOR CONSTRUCTION	J. L. LEE	J. L. LEE	07/01/2024
6	07/01/2024	ISSUED FOR CONSTRUCTION	J. L. LEE	J. L. LEE	07/01/2024

ST. IGNATIUS COLLEGE PREPARATORY

SECTOR PLAN - LEVEL 1 (NORTH)

1/8" = 1'-0"

T2.11B