




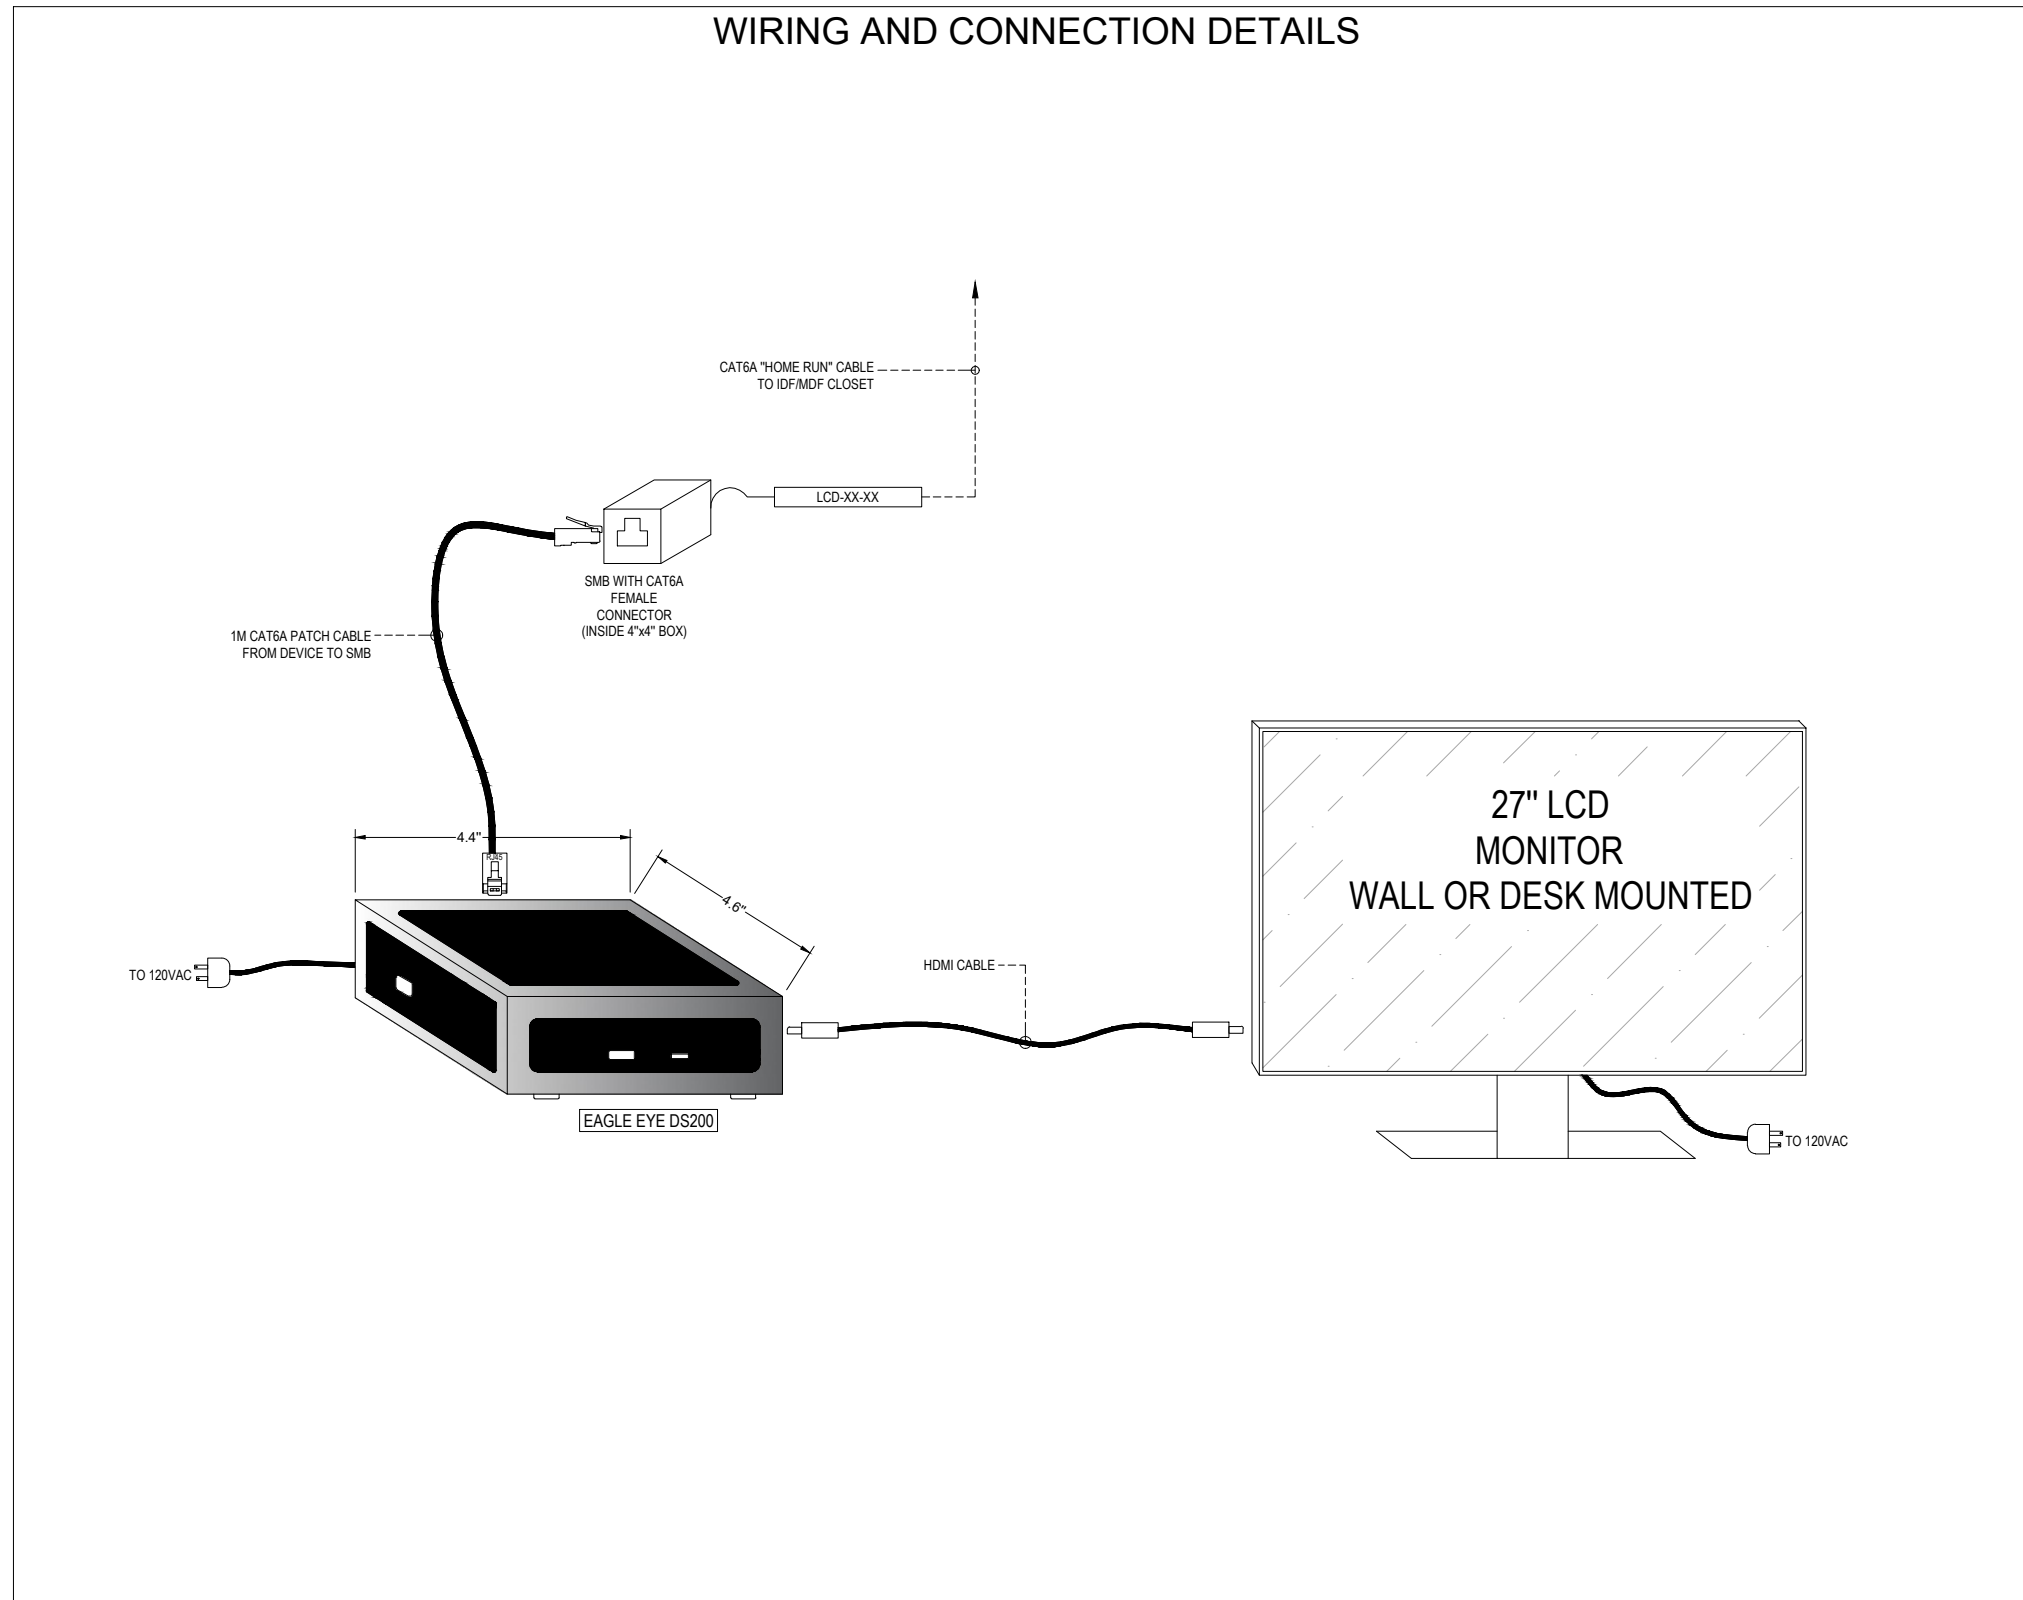


3 TYPICAL FIELD LCD MONITOR CAMERA DISPLAY (LCD-XX-XX)

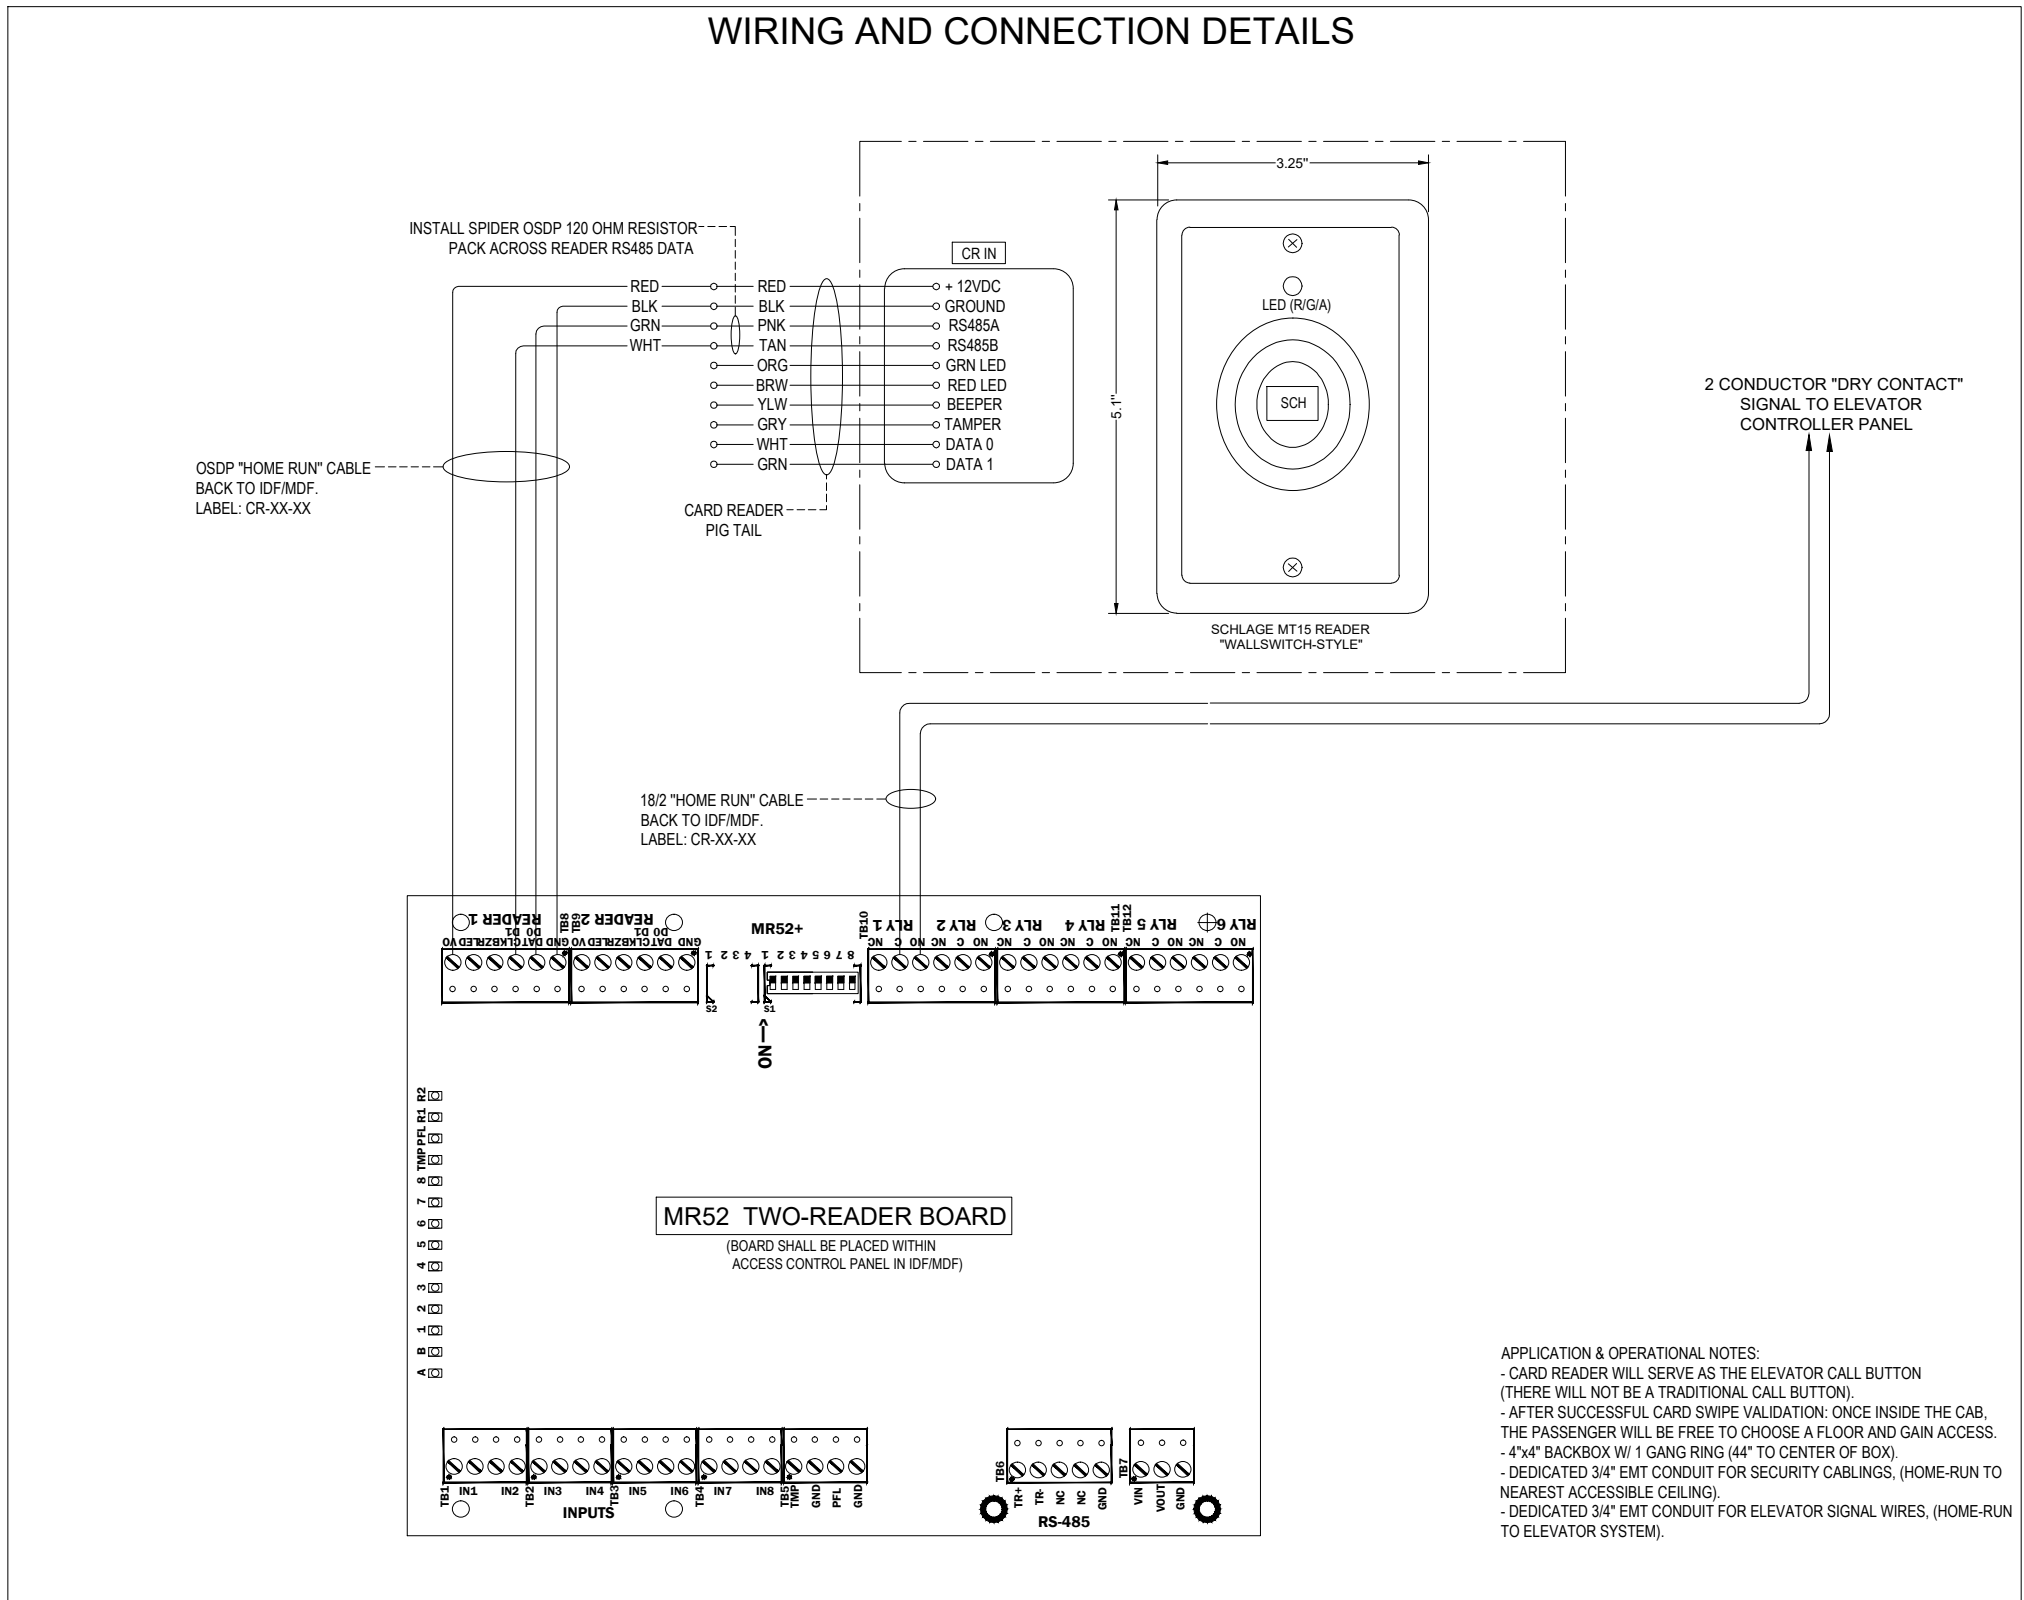


4 TYPICAL ELEVATOR HALL CALL CARD READER (CR)

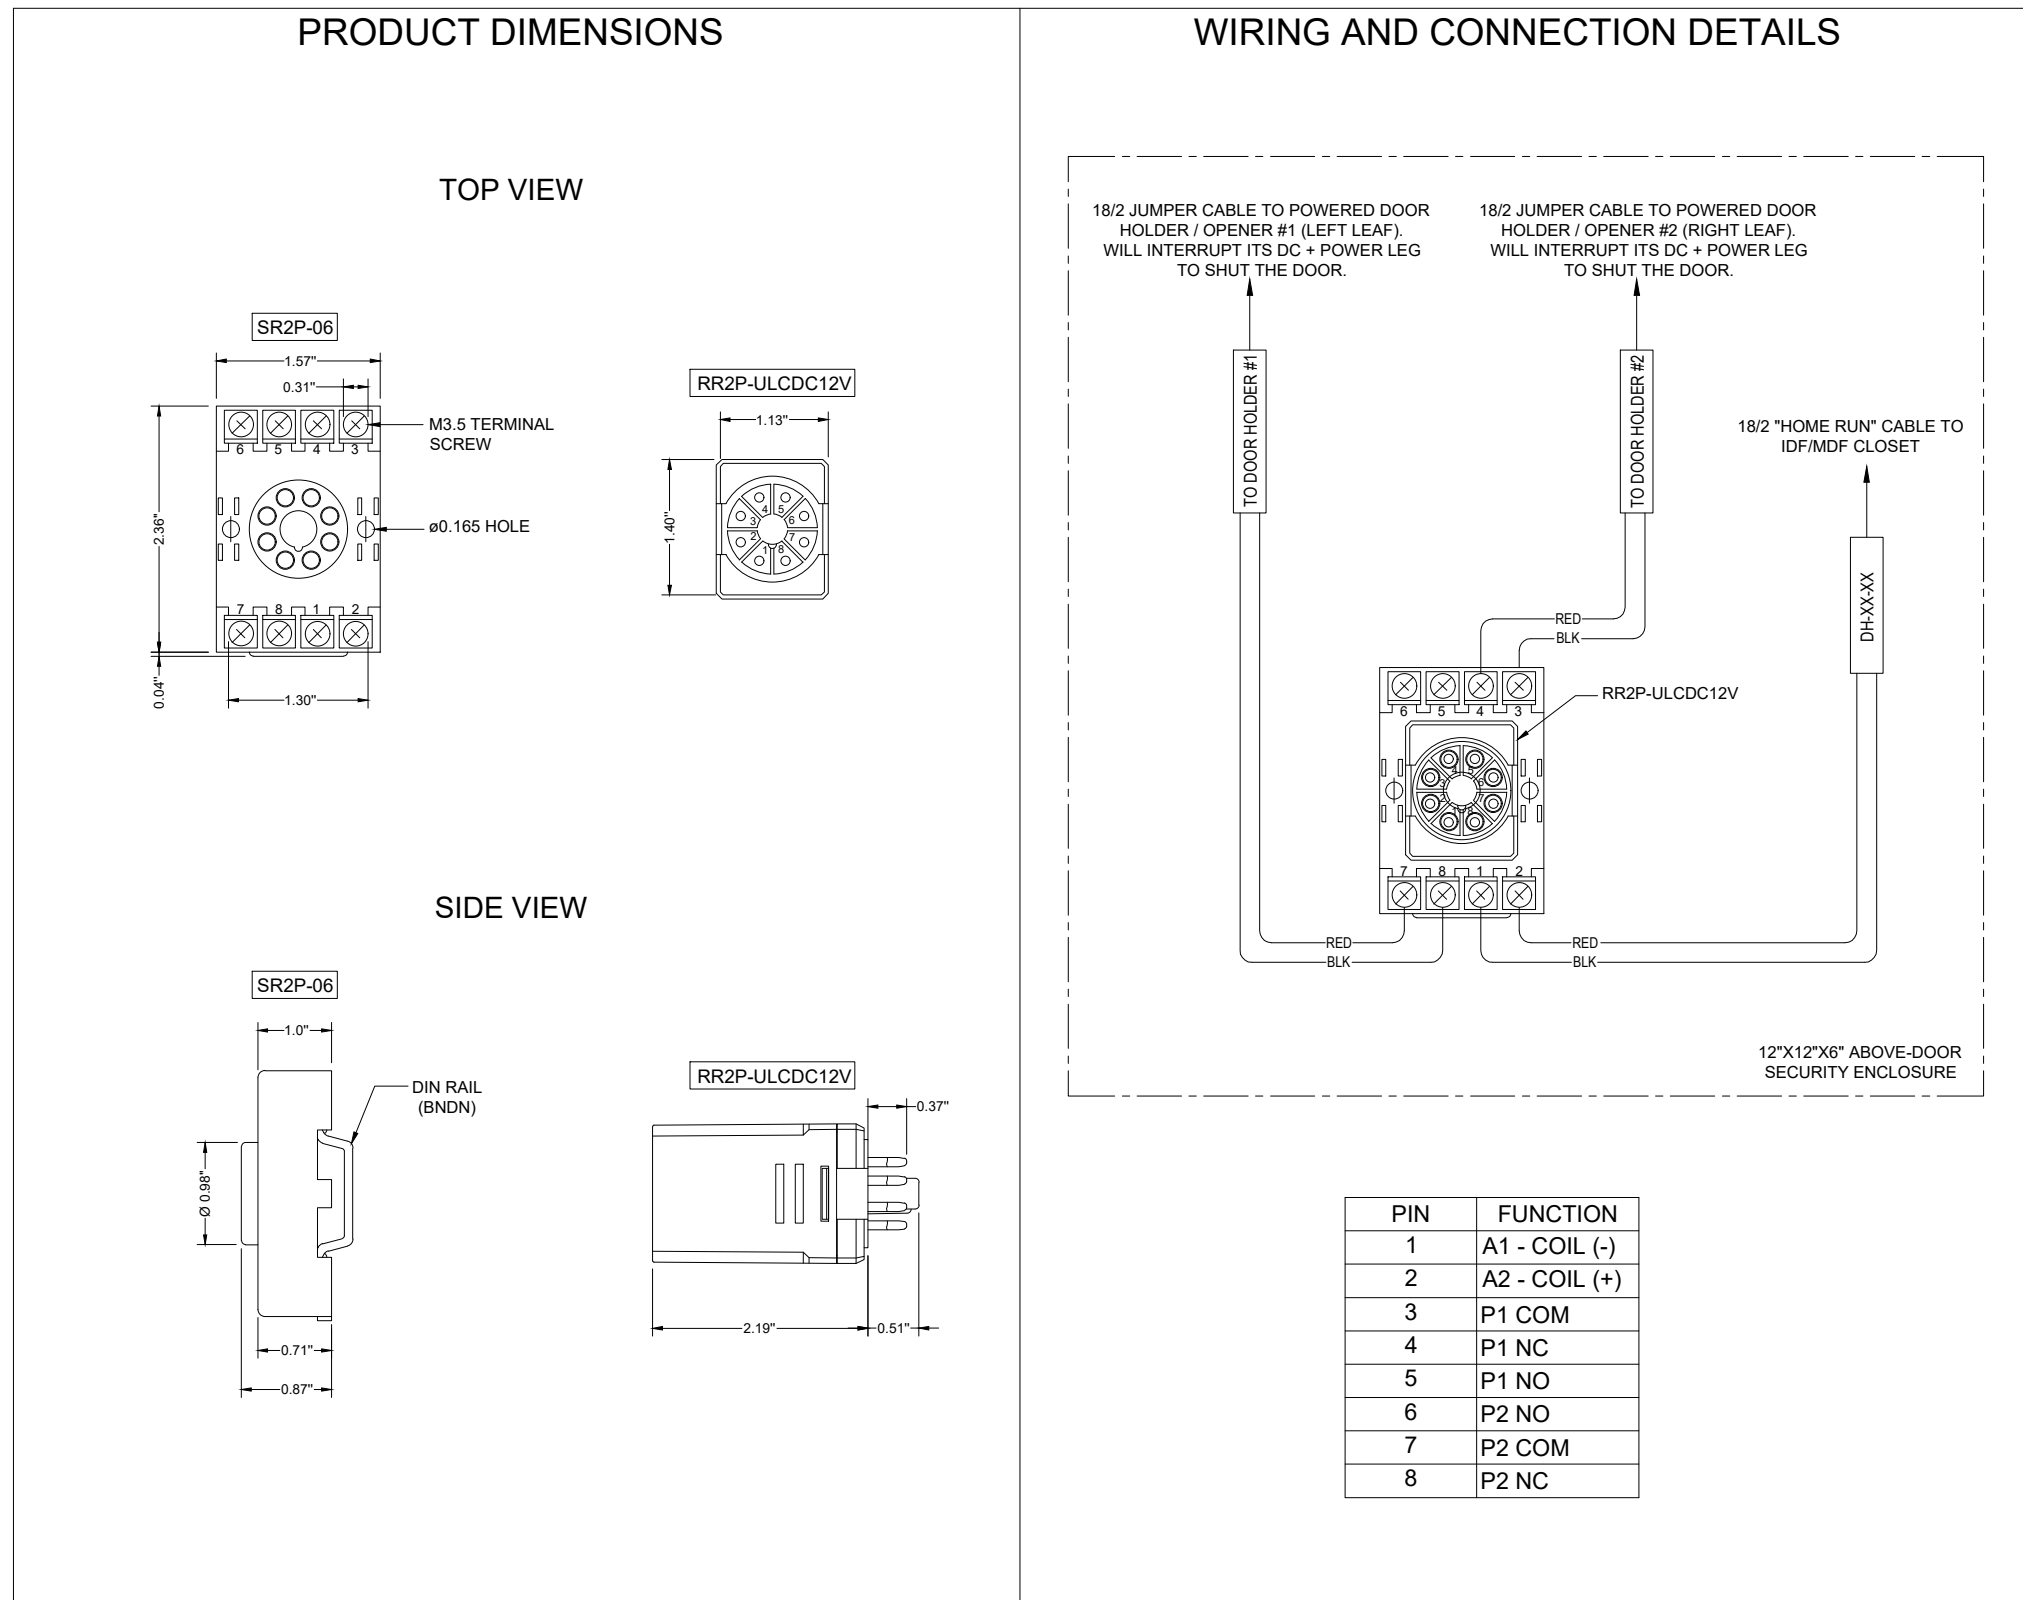

1 TYPICAL DOOR HOLDER (DH)

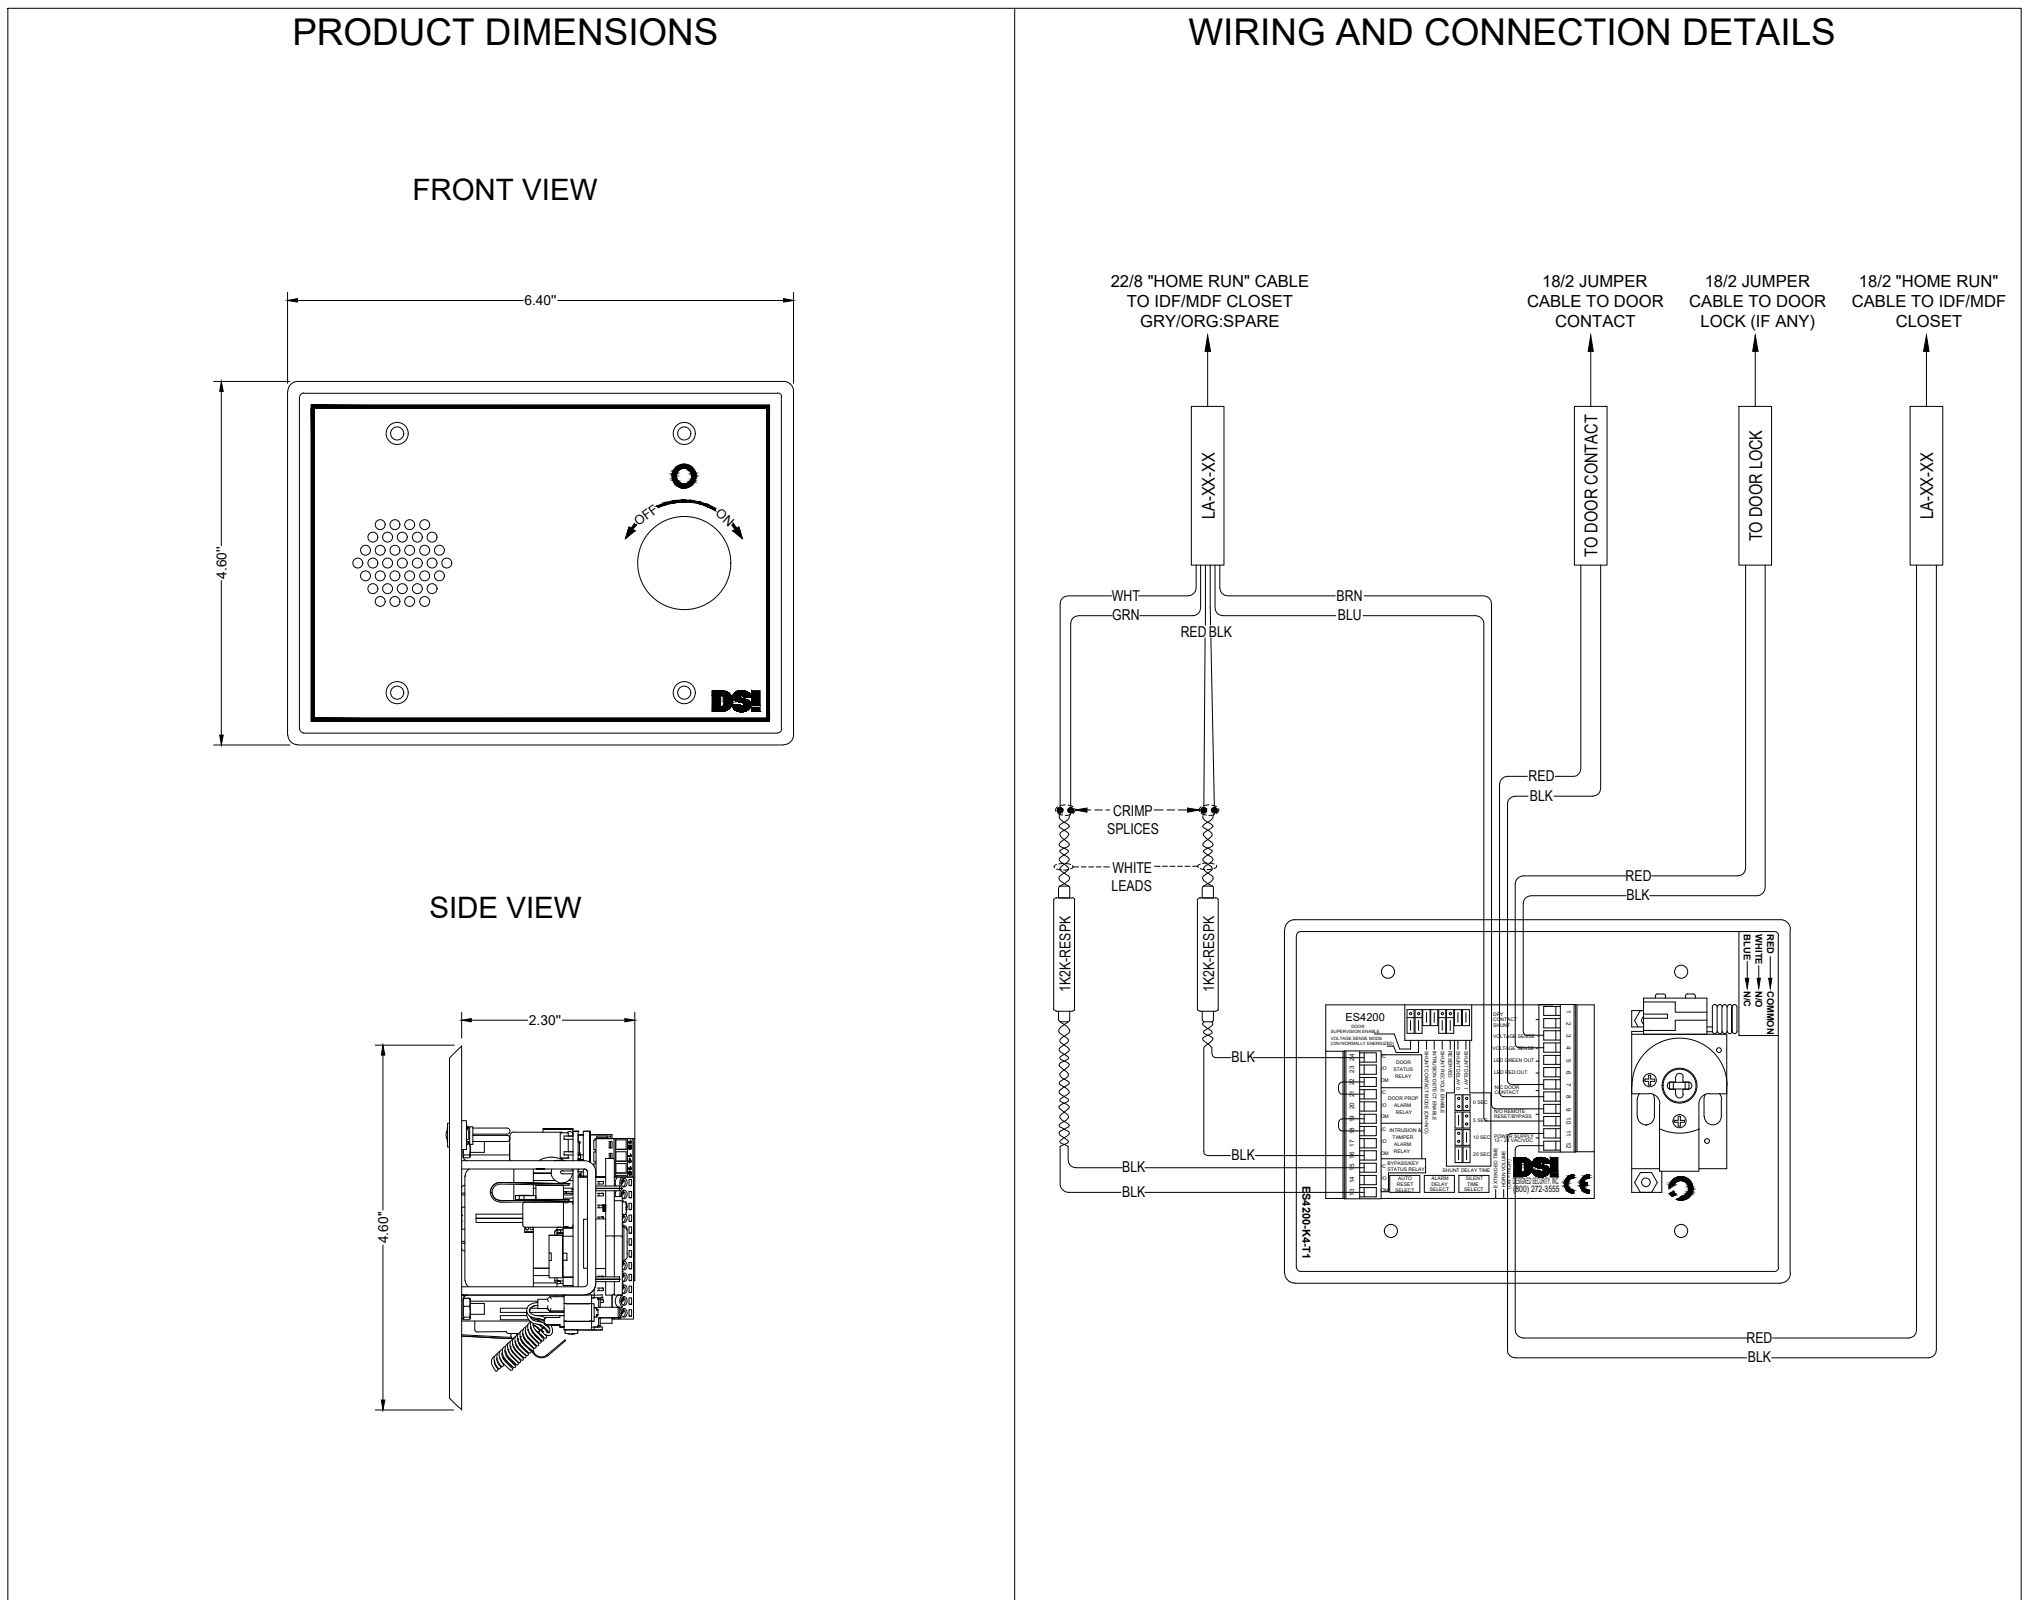

2 TYPICAL LOCAL AUDIBLE SOUNDER (LA)

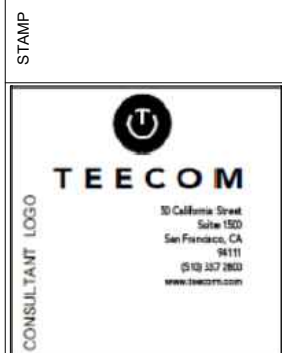

REV	DATE	DESCRIPTION	DESIGNER	CHECKER	DATE	DESCRIPTION
1	05/05/08	STANDARD SECURITY PLANS				

ST. IGNATIUS COLLEGE PREPARATORY
2001 37th Ave. San Francisco, CA 94116

DETAILS - SECURITY DEVICES

T6.19D