

- SHEET NOTES
- A.

REFER TO SHEET T3.101 FOR ABBREVIATIONS, GENERAL NOTES, AND SYMBOL DEFINITIONS.
- B.

REFER TO SHEET T3.002 FOR PRIMARY PATHWAY REQUIREMENTS AND DEFINITIONS.
- C.

REFER TO SHEET T3.003 AND T3.004 FOR OUTLETS/DEVICES SECONDARY PATHWAY AND CABLING REQUIREMENTS.
- D.

SERVE OUTLETS/DEVICES ON THIS SHEET FROM TELECOM ROOMS AS NOTED.
- E.

REFER TO ARCHITECTURAL PLANS FOR EXACT LOCATIONS OF OUTLETS/DEVICES, WHERE SHOWN. OUTLETS/DEVICES ON THIS SHEET ARE SHOWN DIAGRAMMATICALLY.
- F.

REFER TO SECURITY INSTALLATION DETAILS FOR SECONDARY PATHWAY REQUIREMENTS, SYSTEM INTERFACES, AND COMPONENT CONFIGURATIONS.
- G.

PATHWAYS SHOWN ARE DEDICATED FOR TECHNOLOGY CABLING.
- H.

INSTALL SECONDARY PATHWAYS ALONG THE MOST DIRECT ROUTES TO PRIMARY PATHWAYS OR SERVING ROOM.
- I.

INSTALL HORIZONTAL CABLES ALONG THE MOST DIRECT PRIMARY PATHWAY ROUTE TO THE SERVING TELECOM ROOM.
- J.

PROVIDE APPROVED FIRESTOP SYSTEMS AT PENETRATIONS THROUGH FIRE BARRIERS, SMOKE BARRIERS, AND SMOKE PARTITIONS TO MAINTAIN RATINGS.
- K.

PROVIDE AN ALLOWANCE OF (2) CATEGORY 6A DROPS PER 1000 SQUARE FEET FOR WIRELESS ACCESS POINTS. DESIGN OF WIRELESS ACCESS POINTS TO BE COORDINATED WITH OWNER'S IT DEPARTMENT.



STAMP



DB STAMP

REV	DATE	DESCRIPTION
1	01/12/2024	ISSUED FOR CONSTRUCTION
2	02/15/2024	REVISION: ADDITIONAL CABLE TRAYS
3	03/01/2024	REVISION: UPDATE CABLE TRAY SIZES
4	03/15/2024	REVISION: ADDITIONAL CABLE TRAYS
5	04/01/2024	REVISION: UPDATE CABLE TRAY SIZES
6	04/15/2024	REVISION: ADDITIONAL CABLE TRAYS
7	05/01/2024	REVISION: UPDATE CABLE TRAY SIZES
8	05/15/2024	REVISION: ADDITIONAL CABLE TRAYS
9	06/01/2024	REVISION: UPDATE CABLE TRAY SIZES
10	06/15/2024	REVISION: ADDITIONAL CABLE TRAYS


ST. IGNATIUS COLLEGE PREPARATORY

SECTOR REFLECTED CEILING PLAN - LEVEL 1 (NORTH)

2001 37th Ave. San Francisco, CA 94116

1/8" = 1'-0"

T3.11B

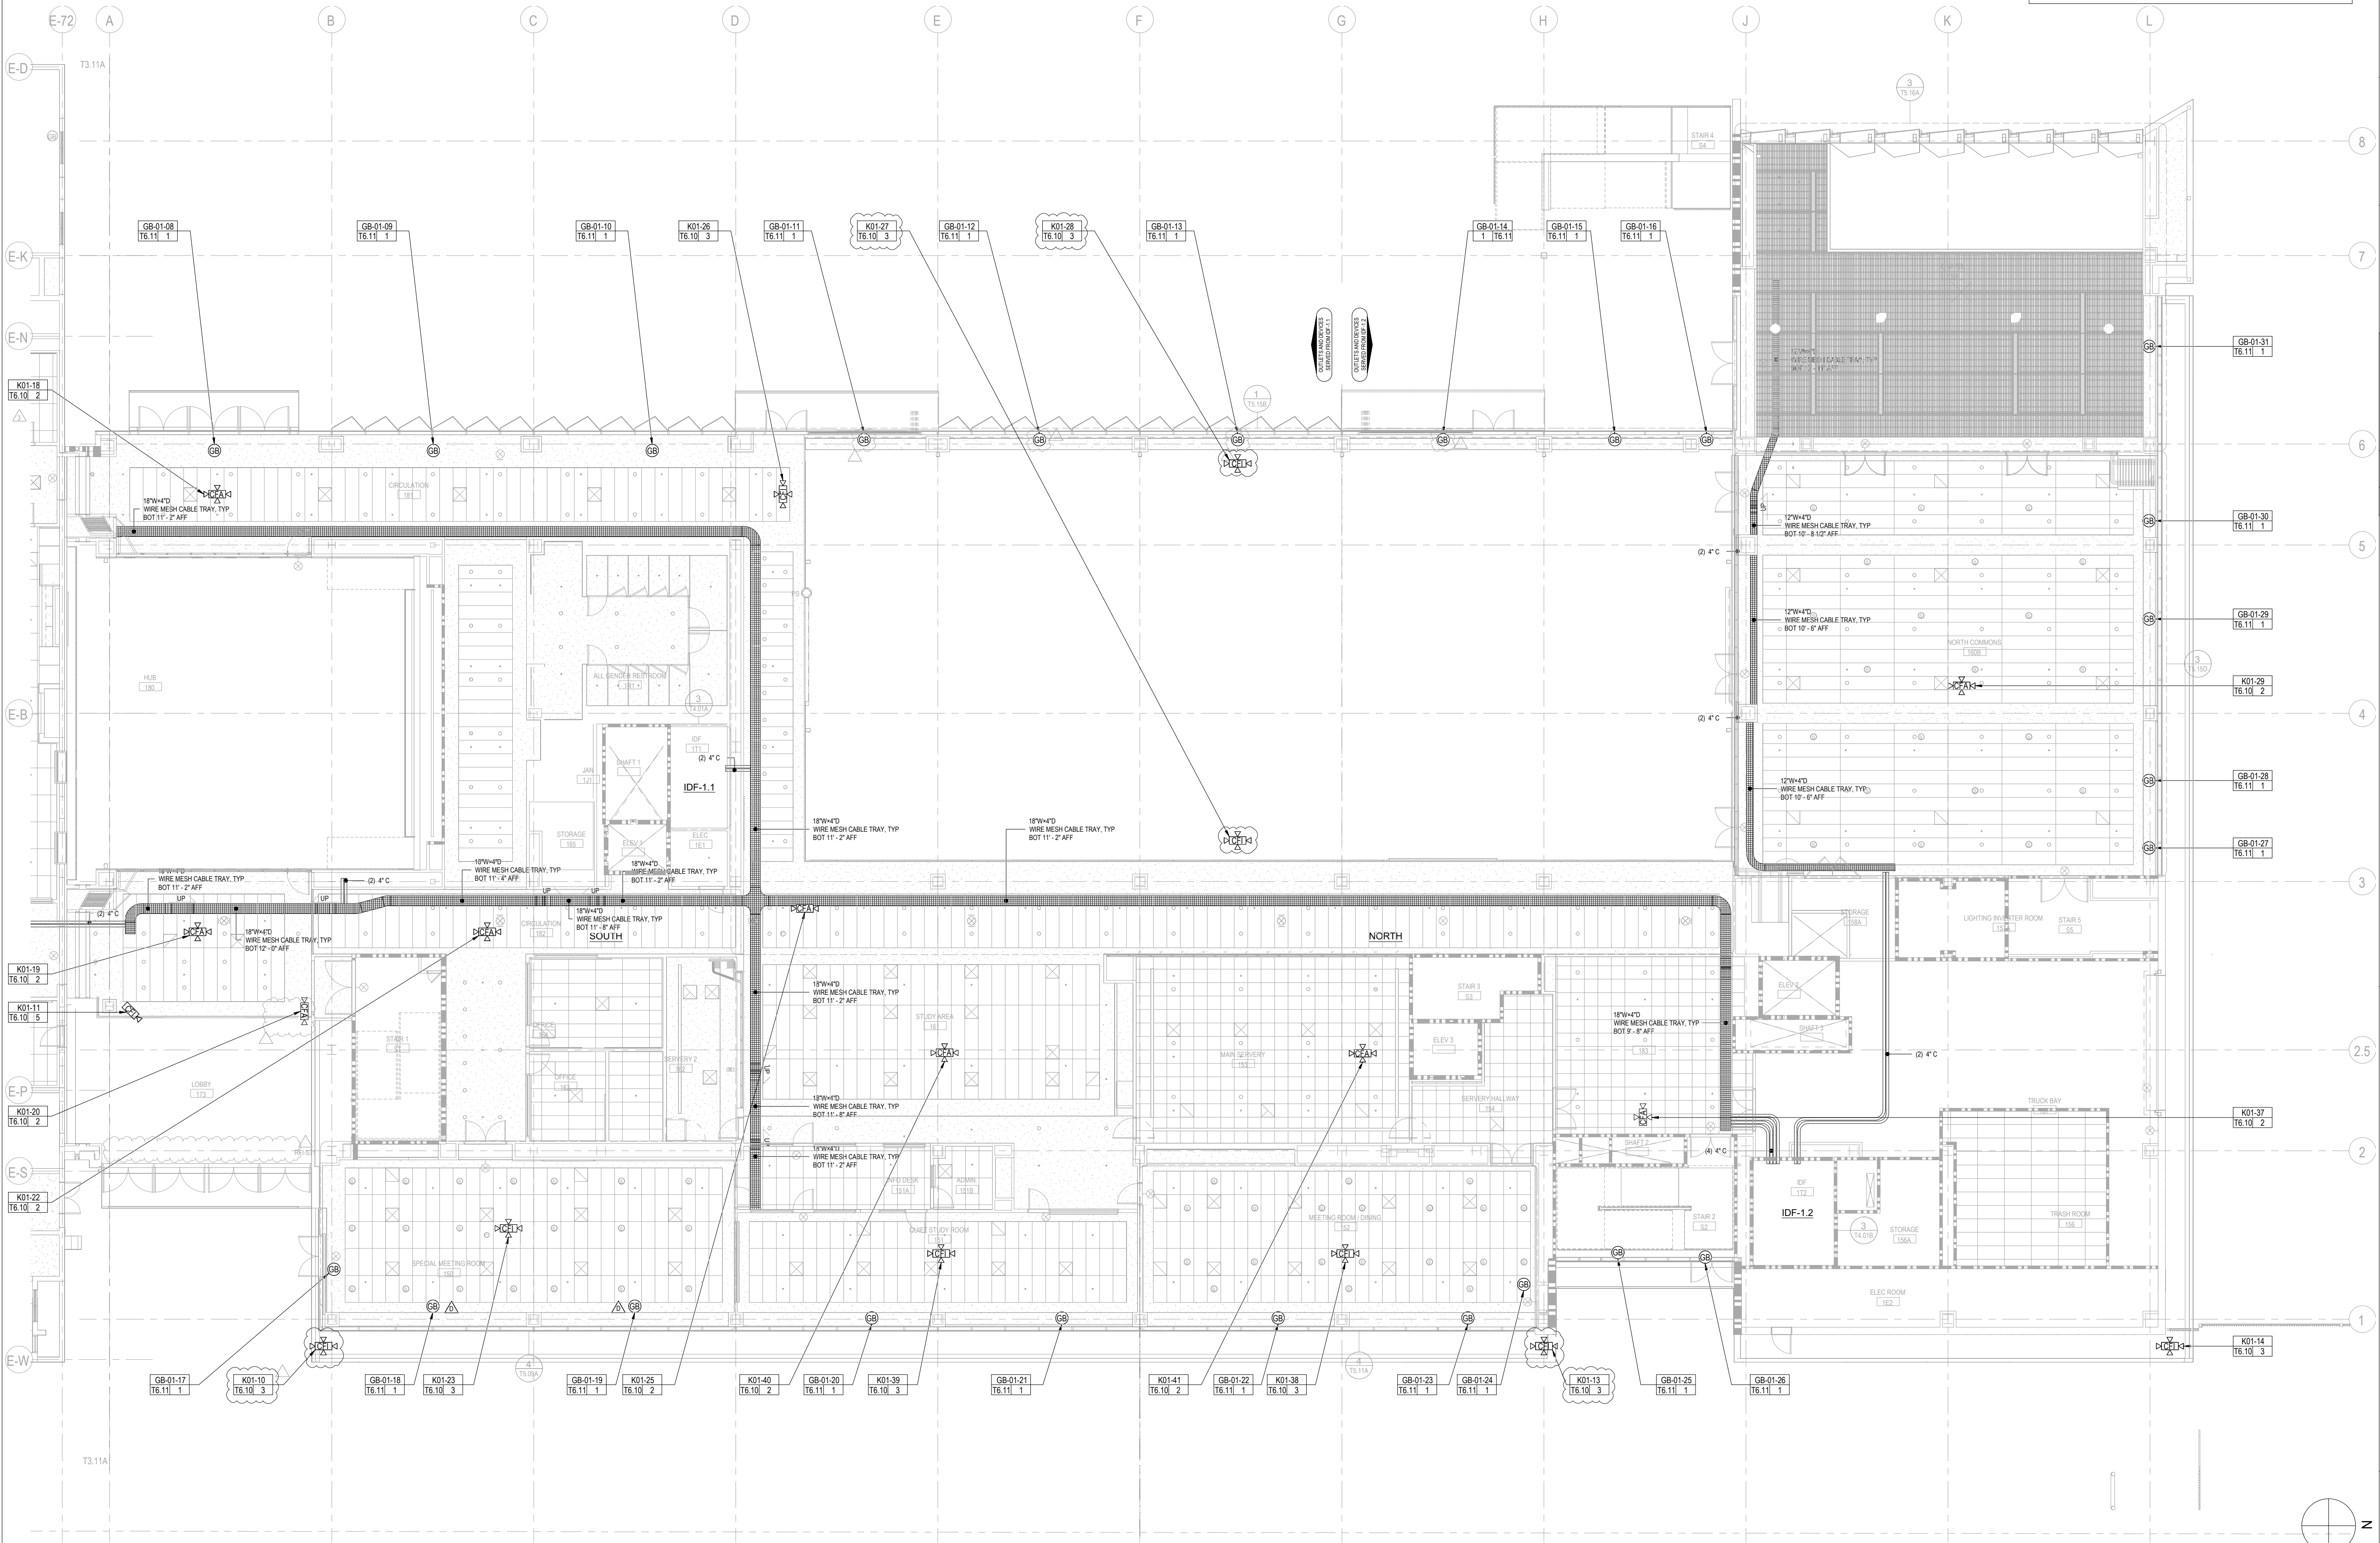

7/1/2024 4:27:05 PM