

SHEET NOTES

1. ALL 48" x 96" PLYWOOD MOUNTING BACKBOARD MUST BE FIRE-RATED



DES. STAMP


REV. DATE DESCRIPTION

ST. IGNATIUS COLLEGE PREPARATORY

2001, 37th Ave. San Francisco, CA 94116


SECURITY ENCLOSURE LAYOUTS

T6.15A

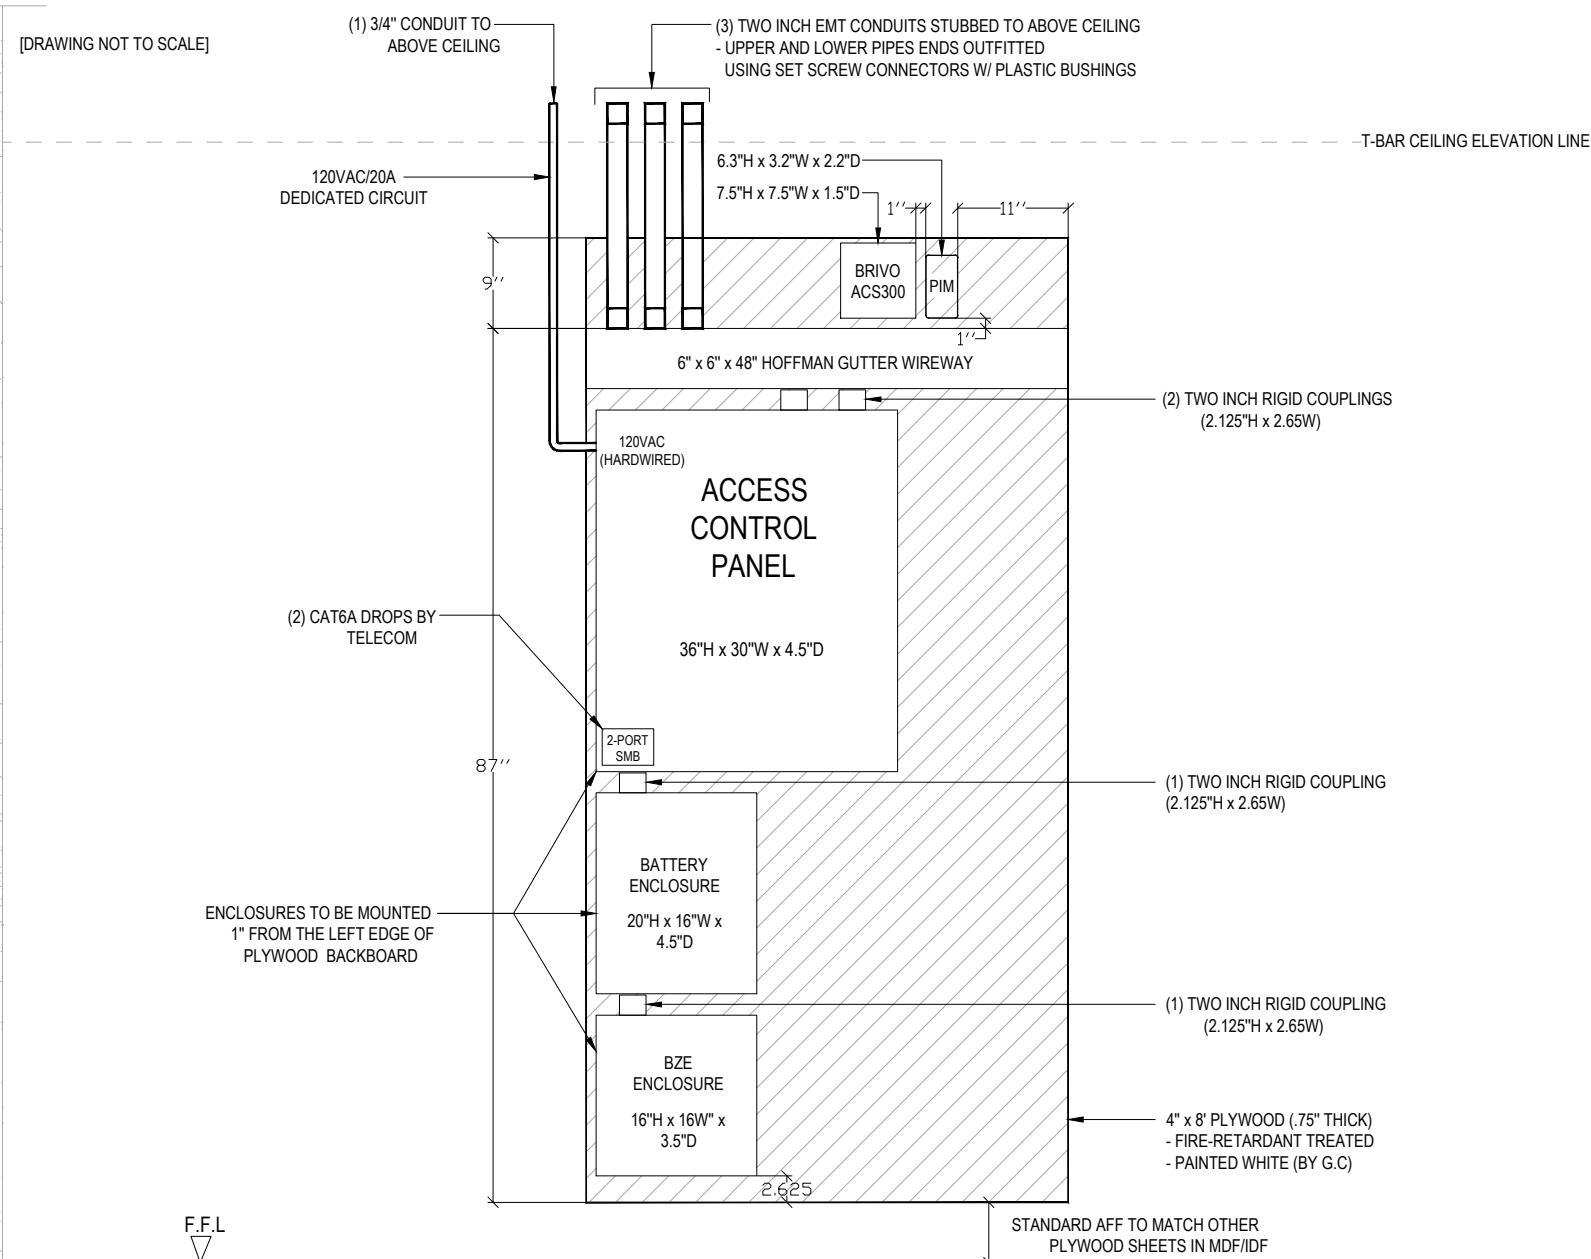


3

1.1 IDF LEVEL 1 SOUTH

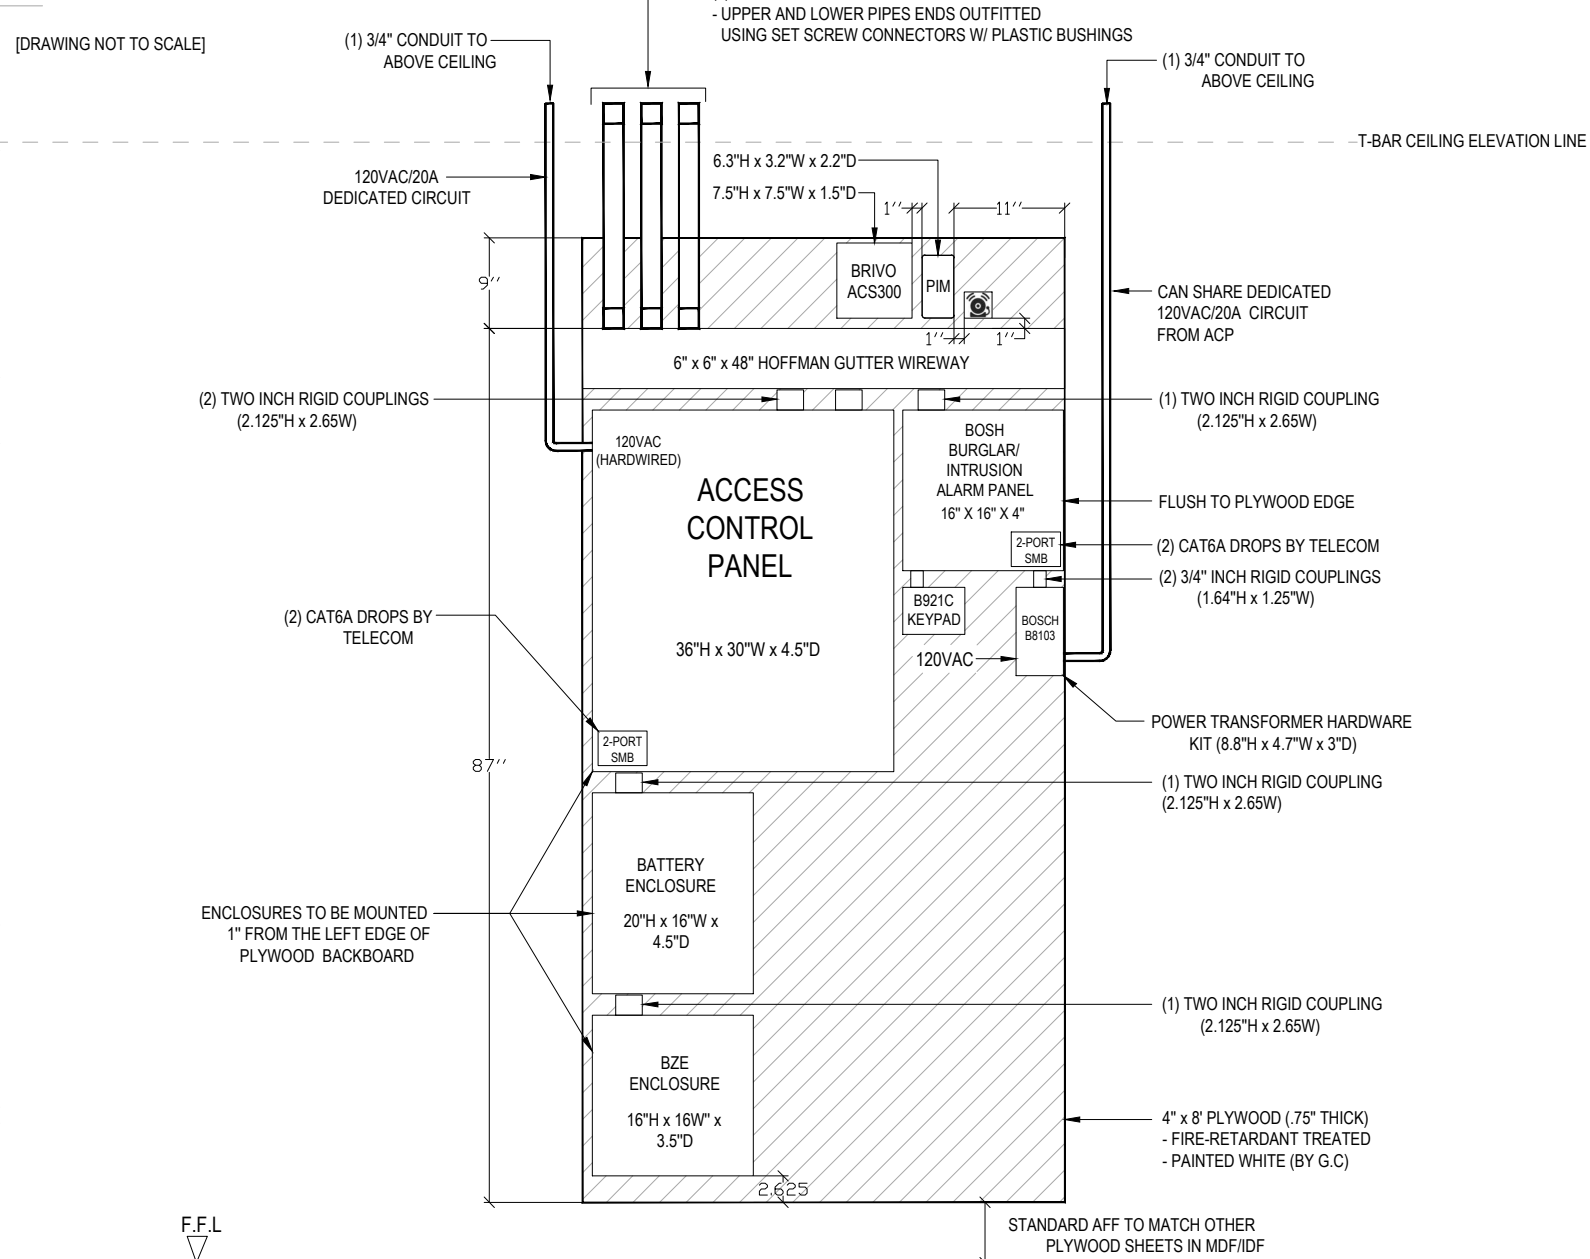


4

1.2 IDF LEVEL 1 NORTH

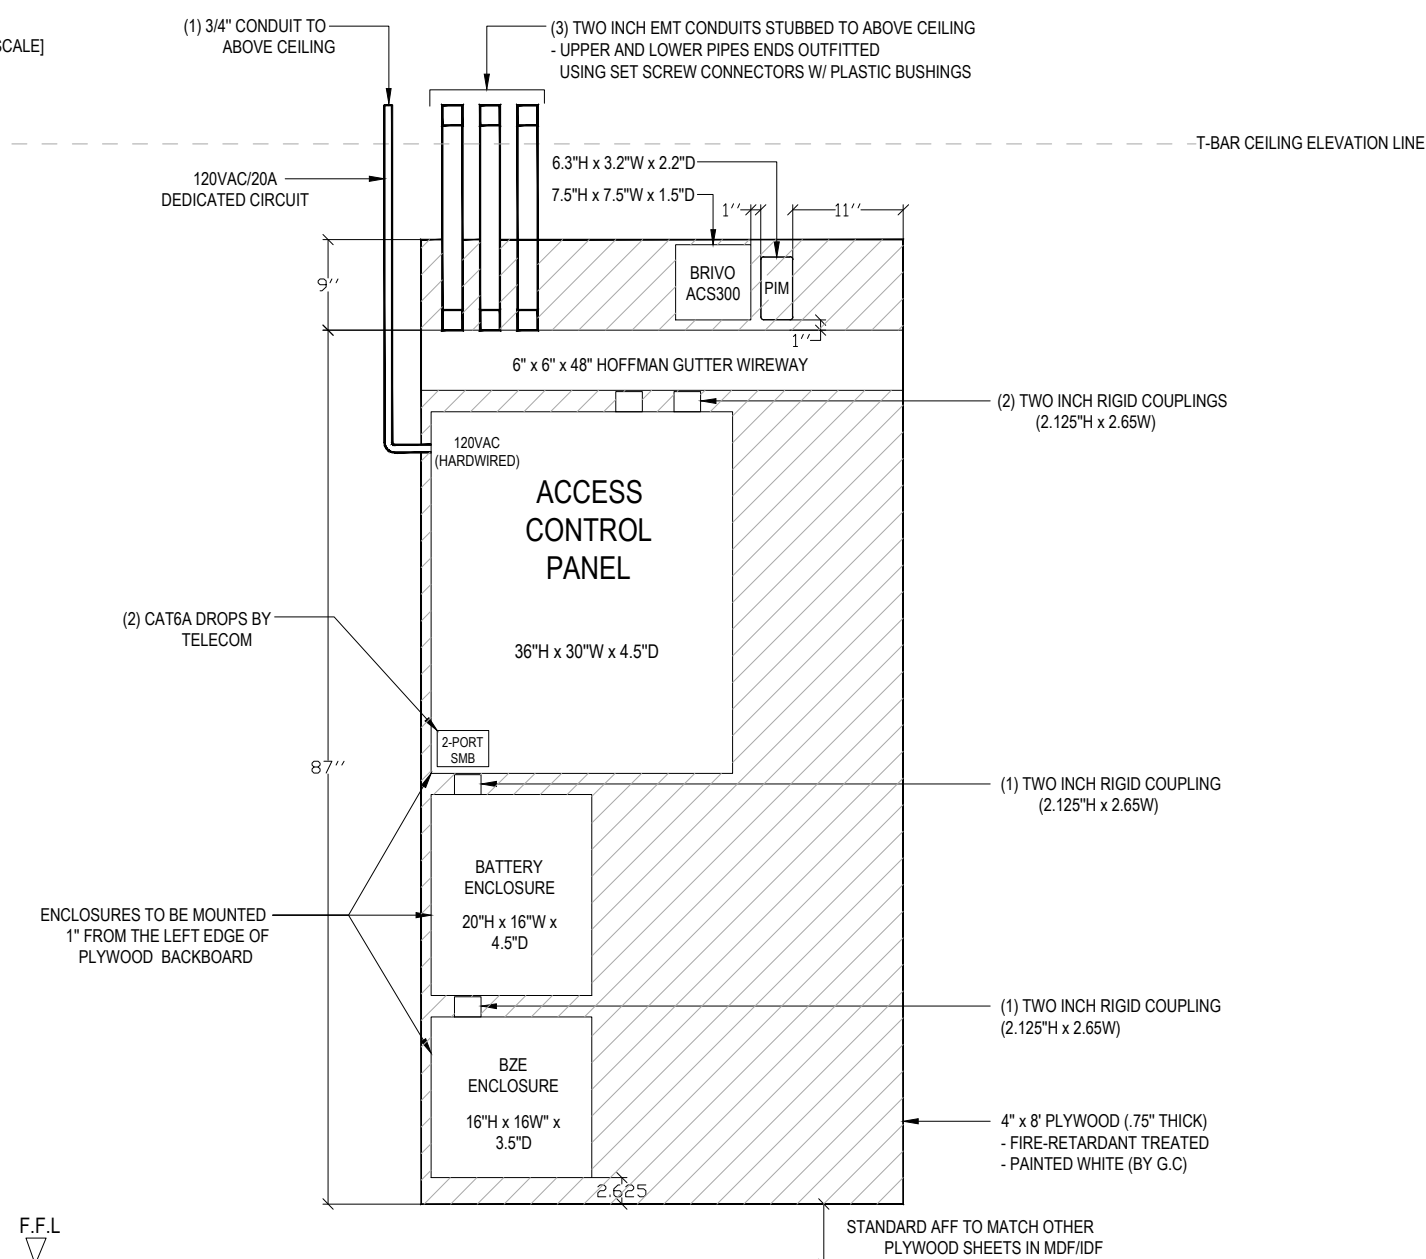

1

0.1 MDF LOWER LEVEL SOUTH

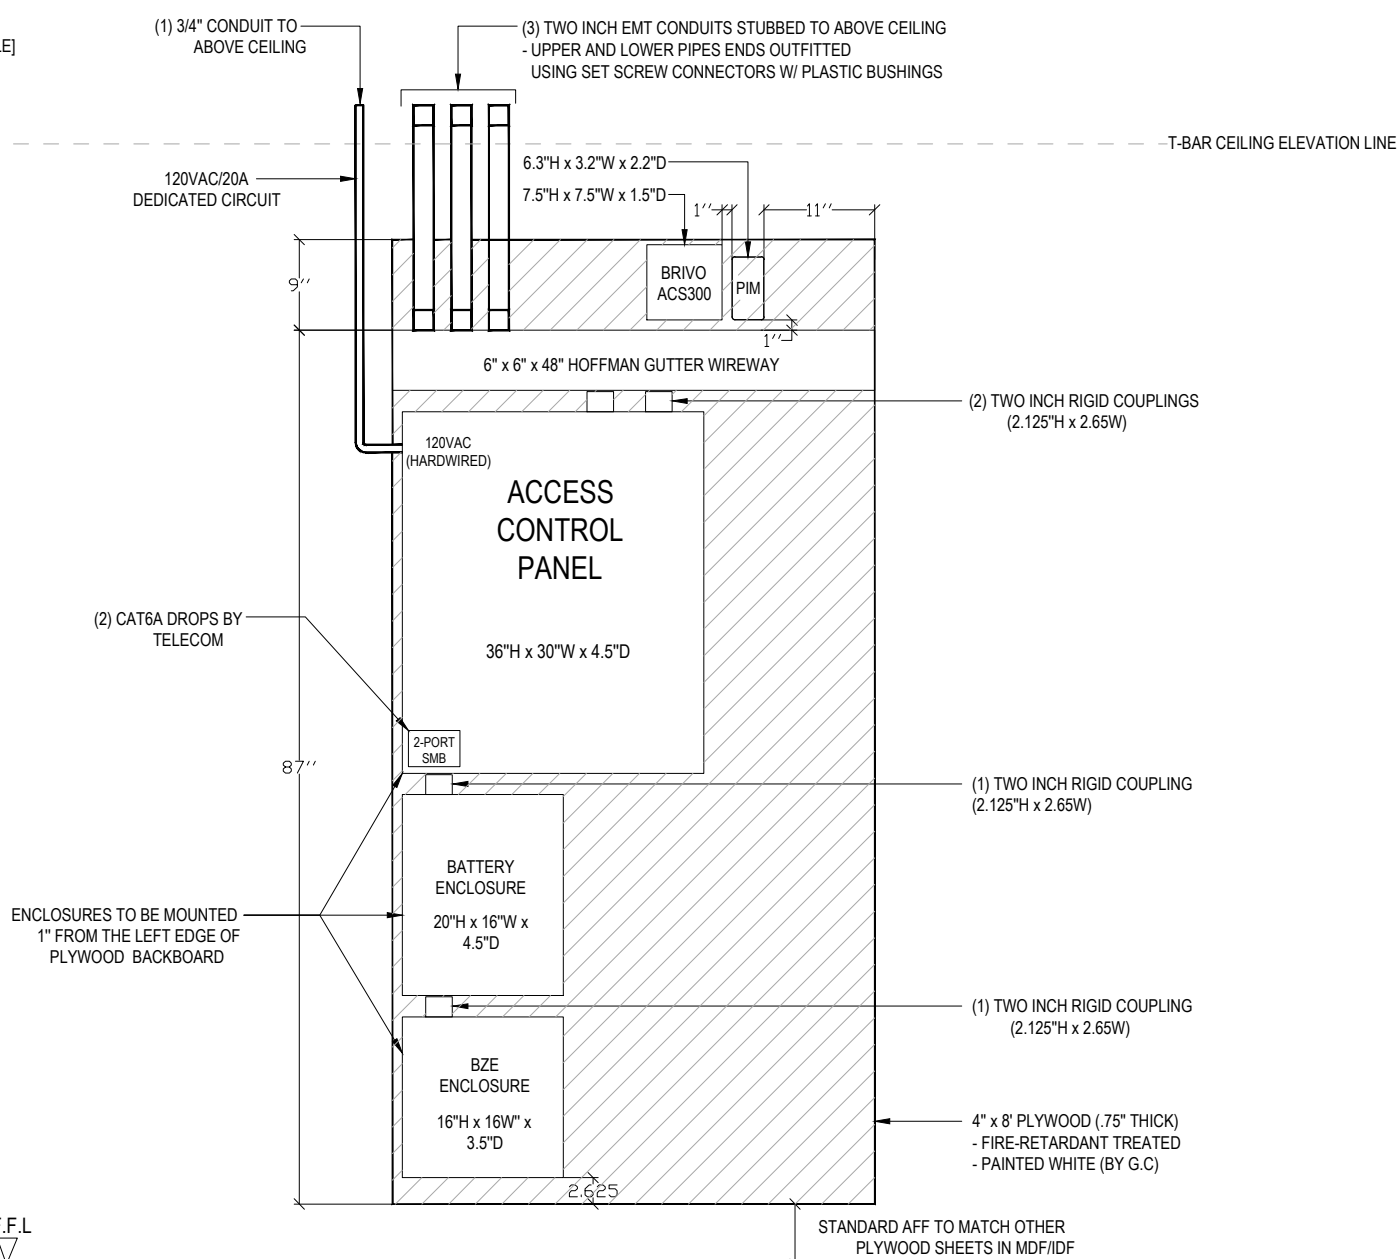

2

0.2 IDF LOWER LEVEL NORTH