



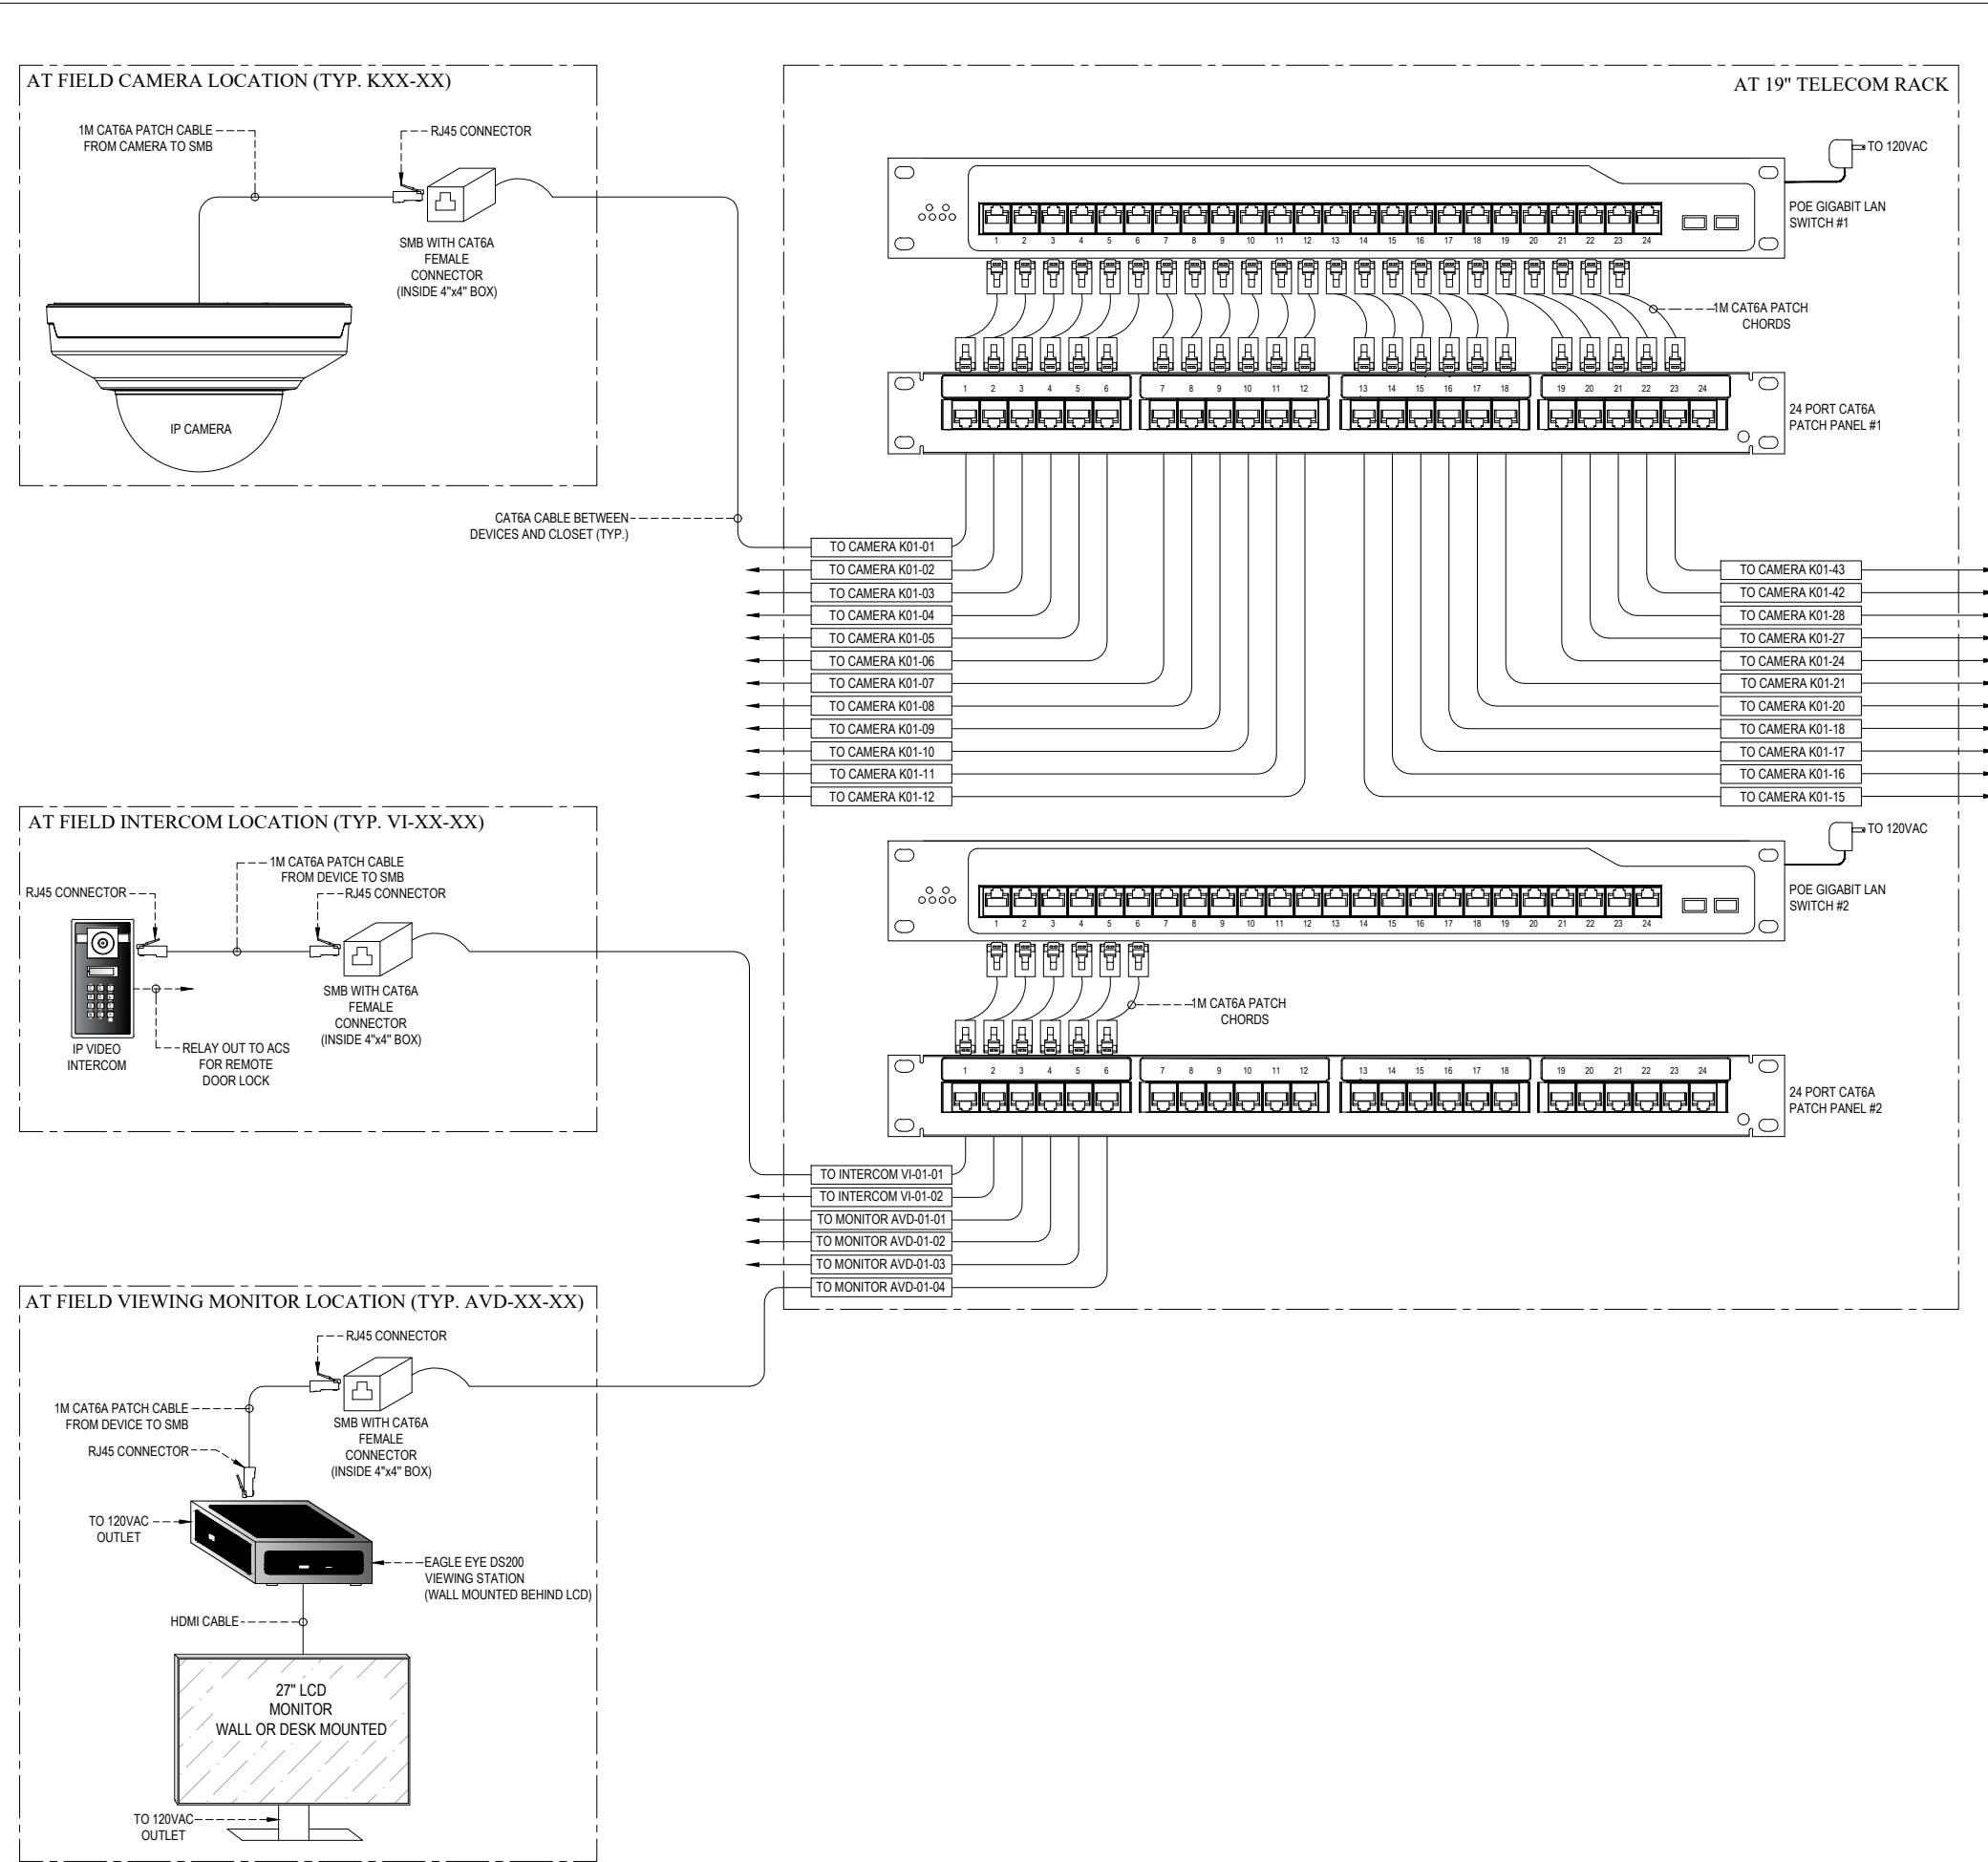


3

1.1 IDF (LEVEL ONE SOUTH)

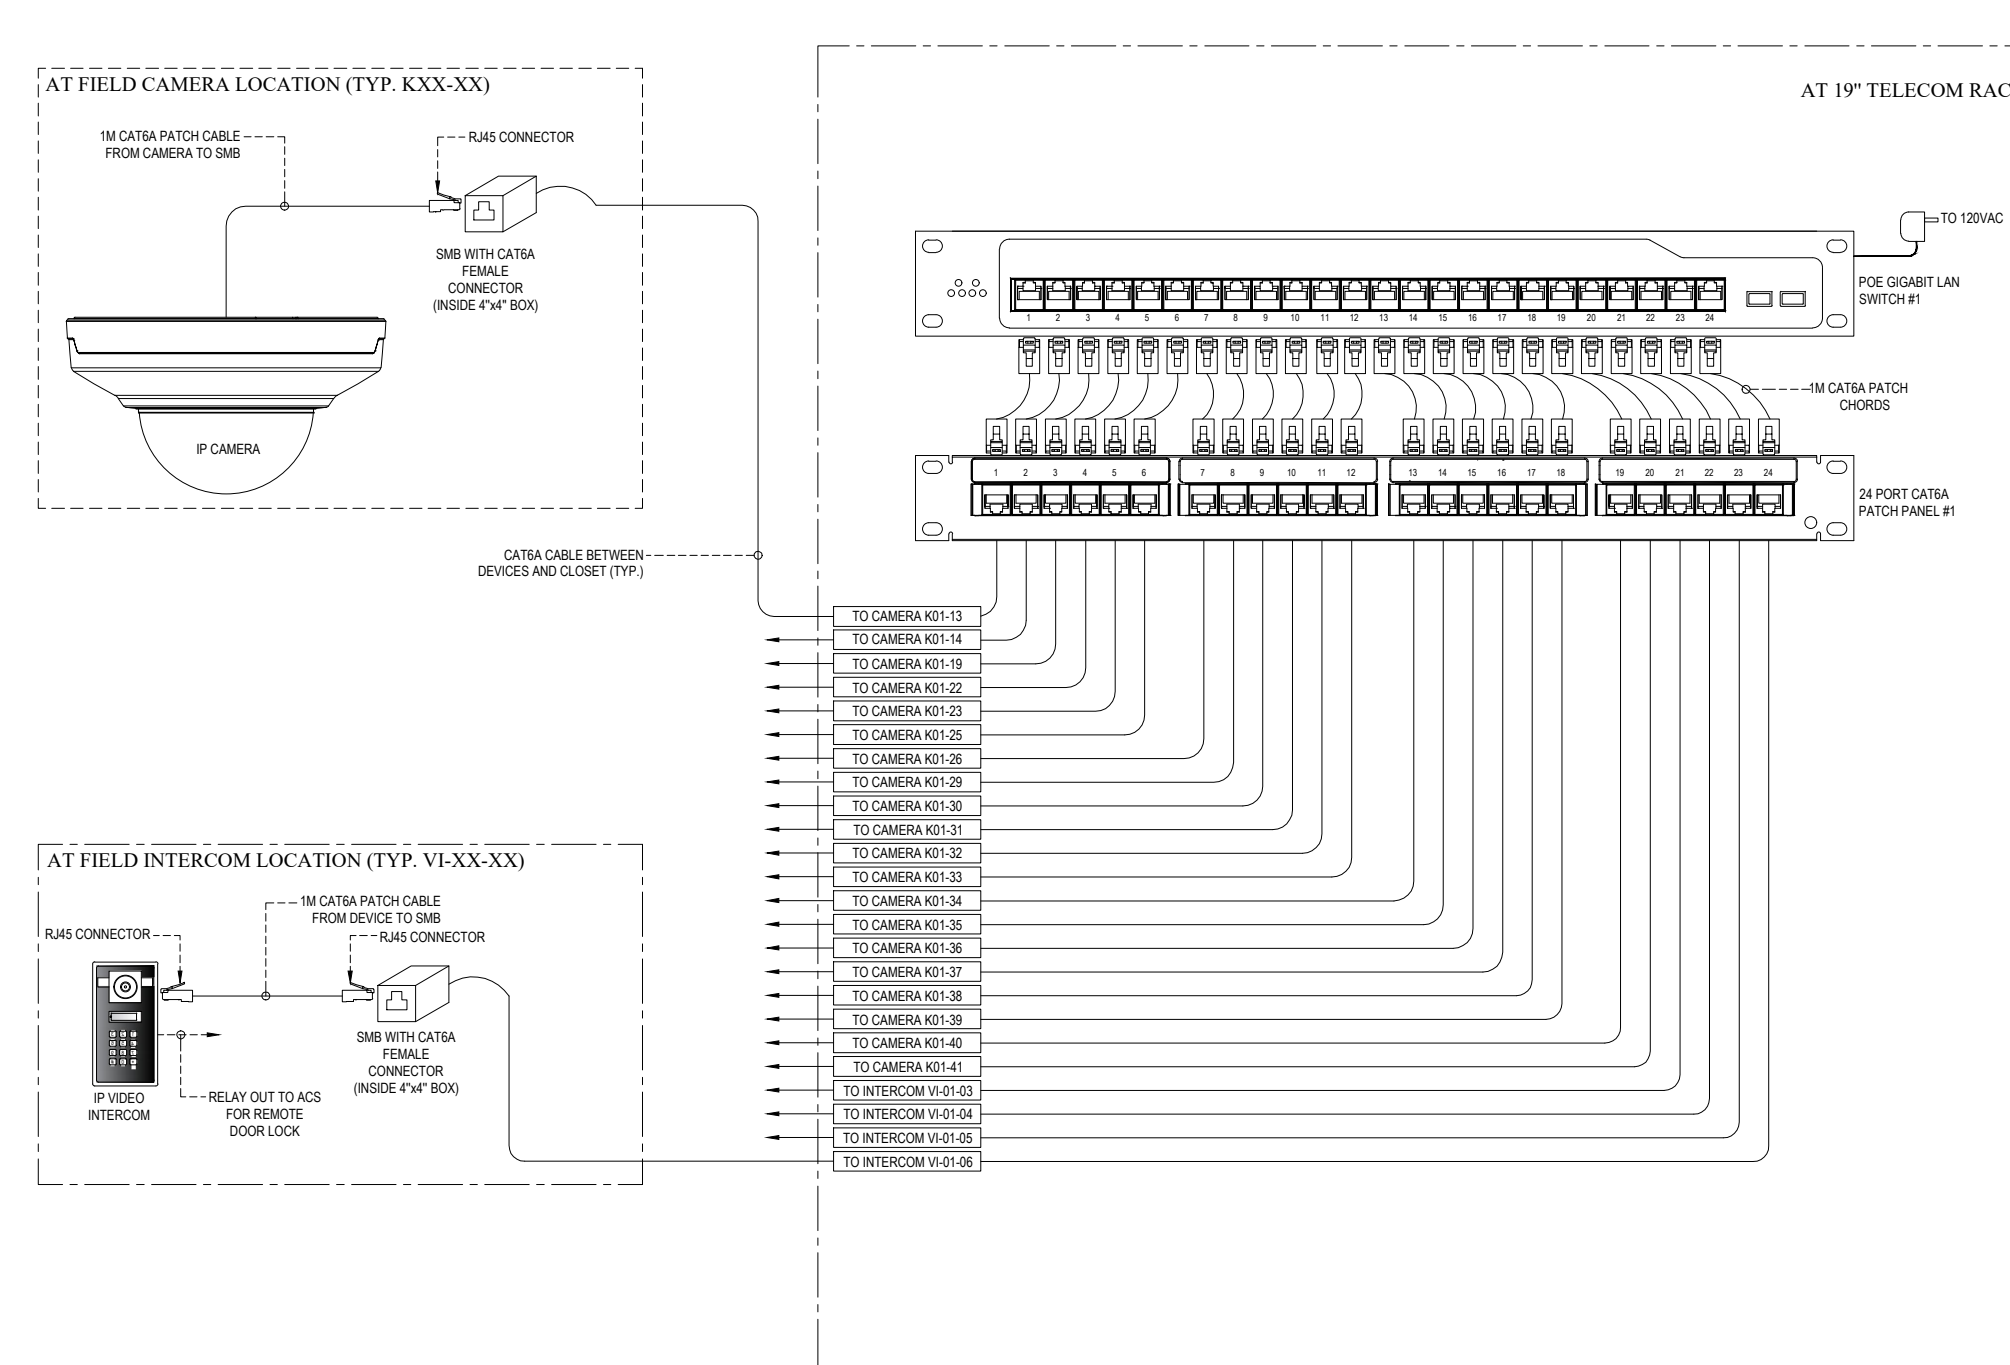


4

1.2 IDF (LEVEL ONE NORTH)

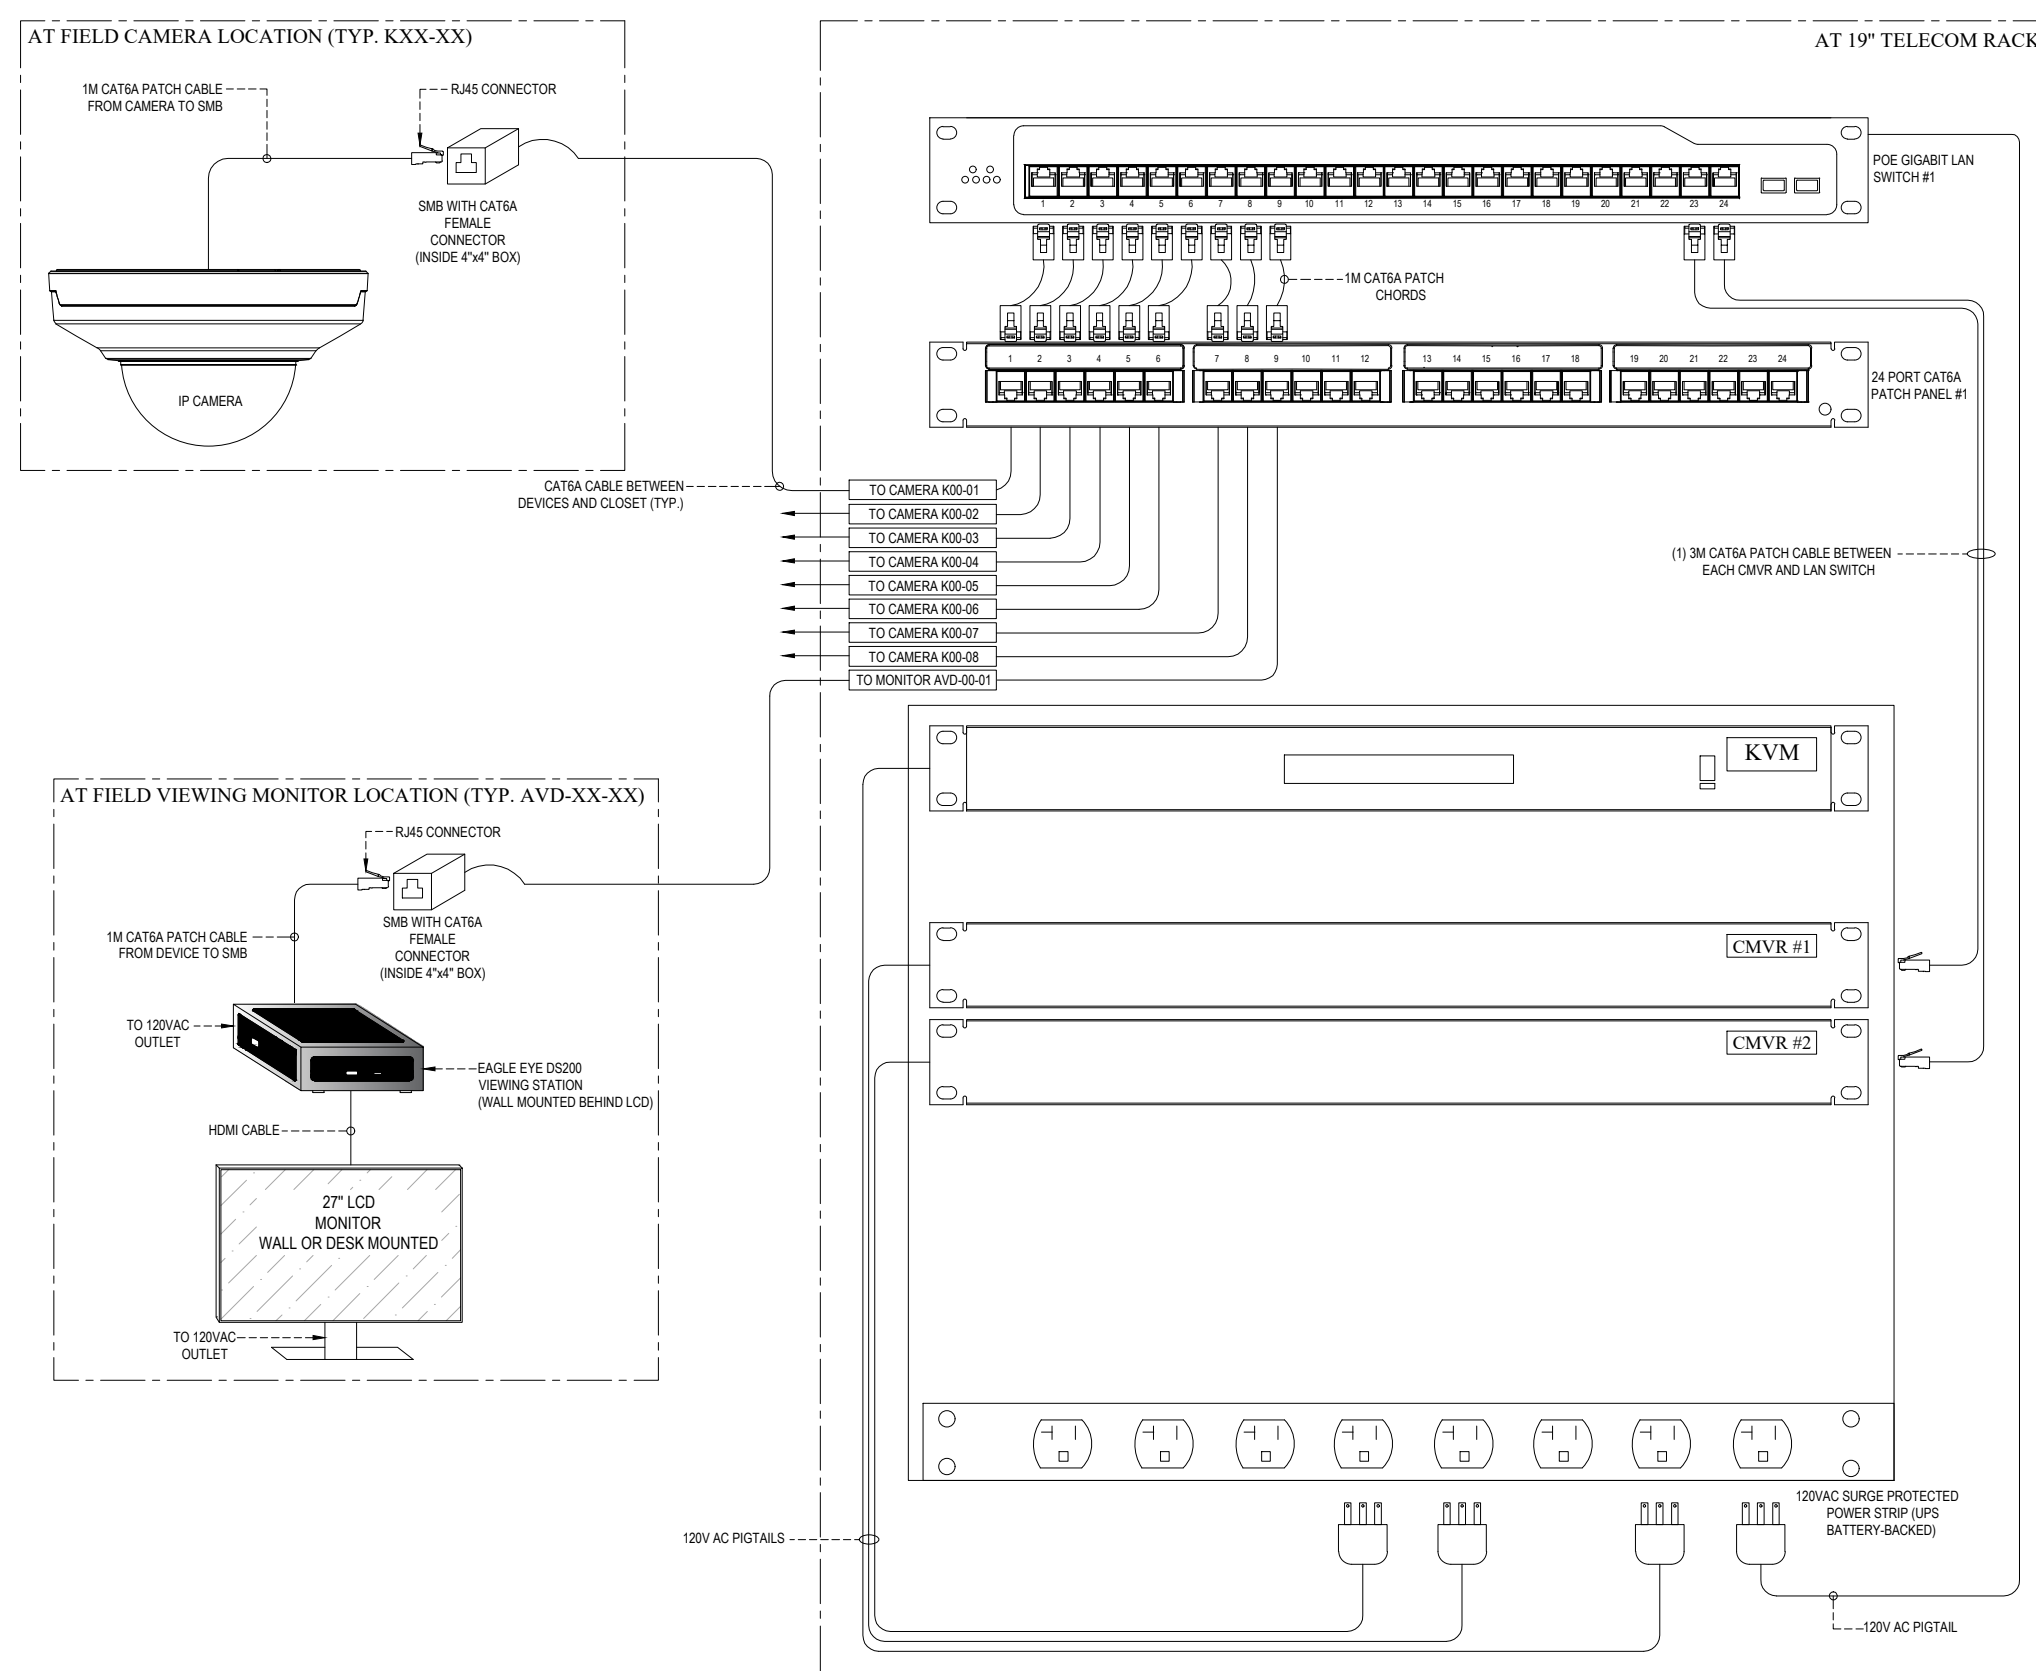


1

0.1 MDF (LOWER LEVEL SOUTH)

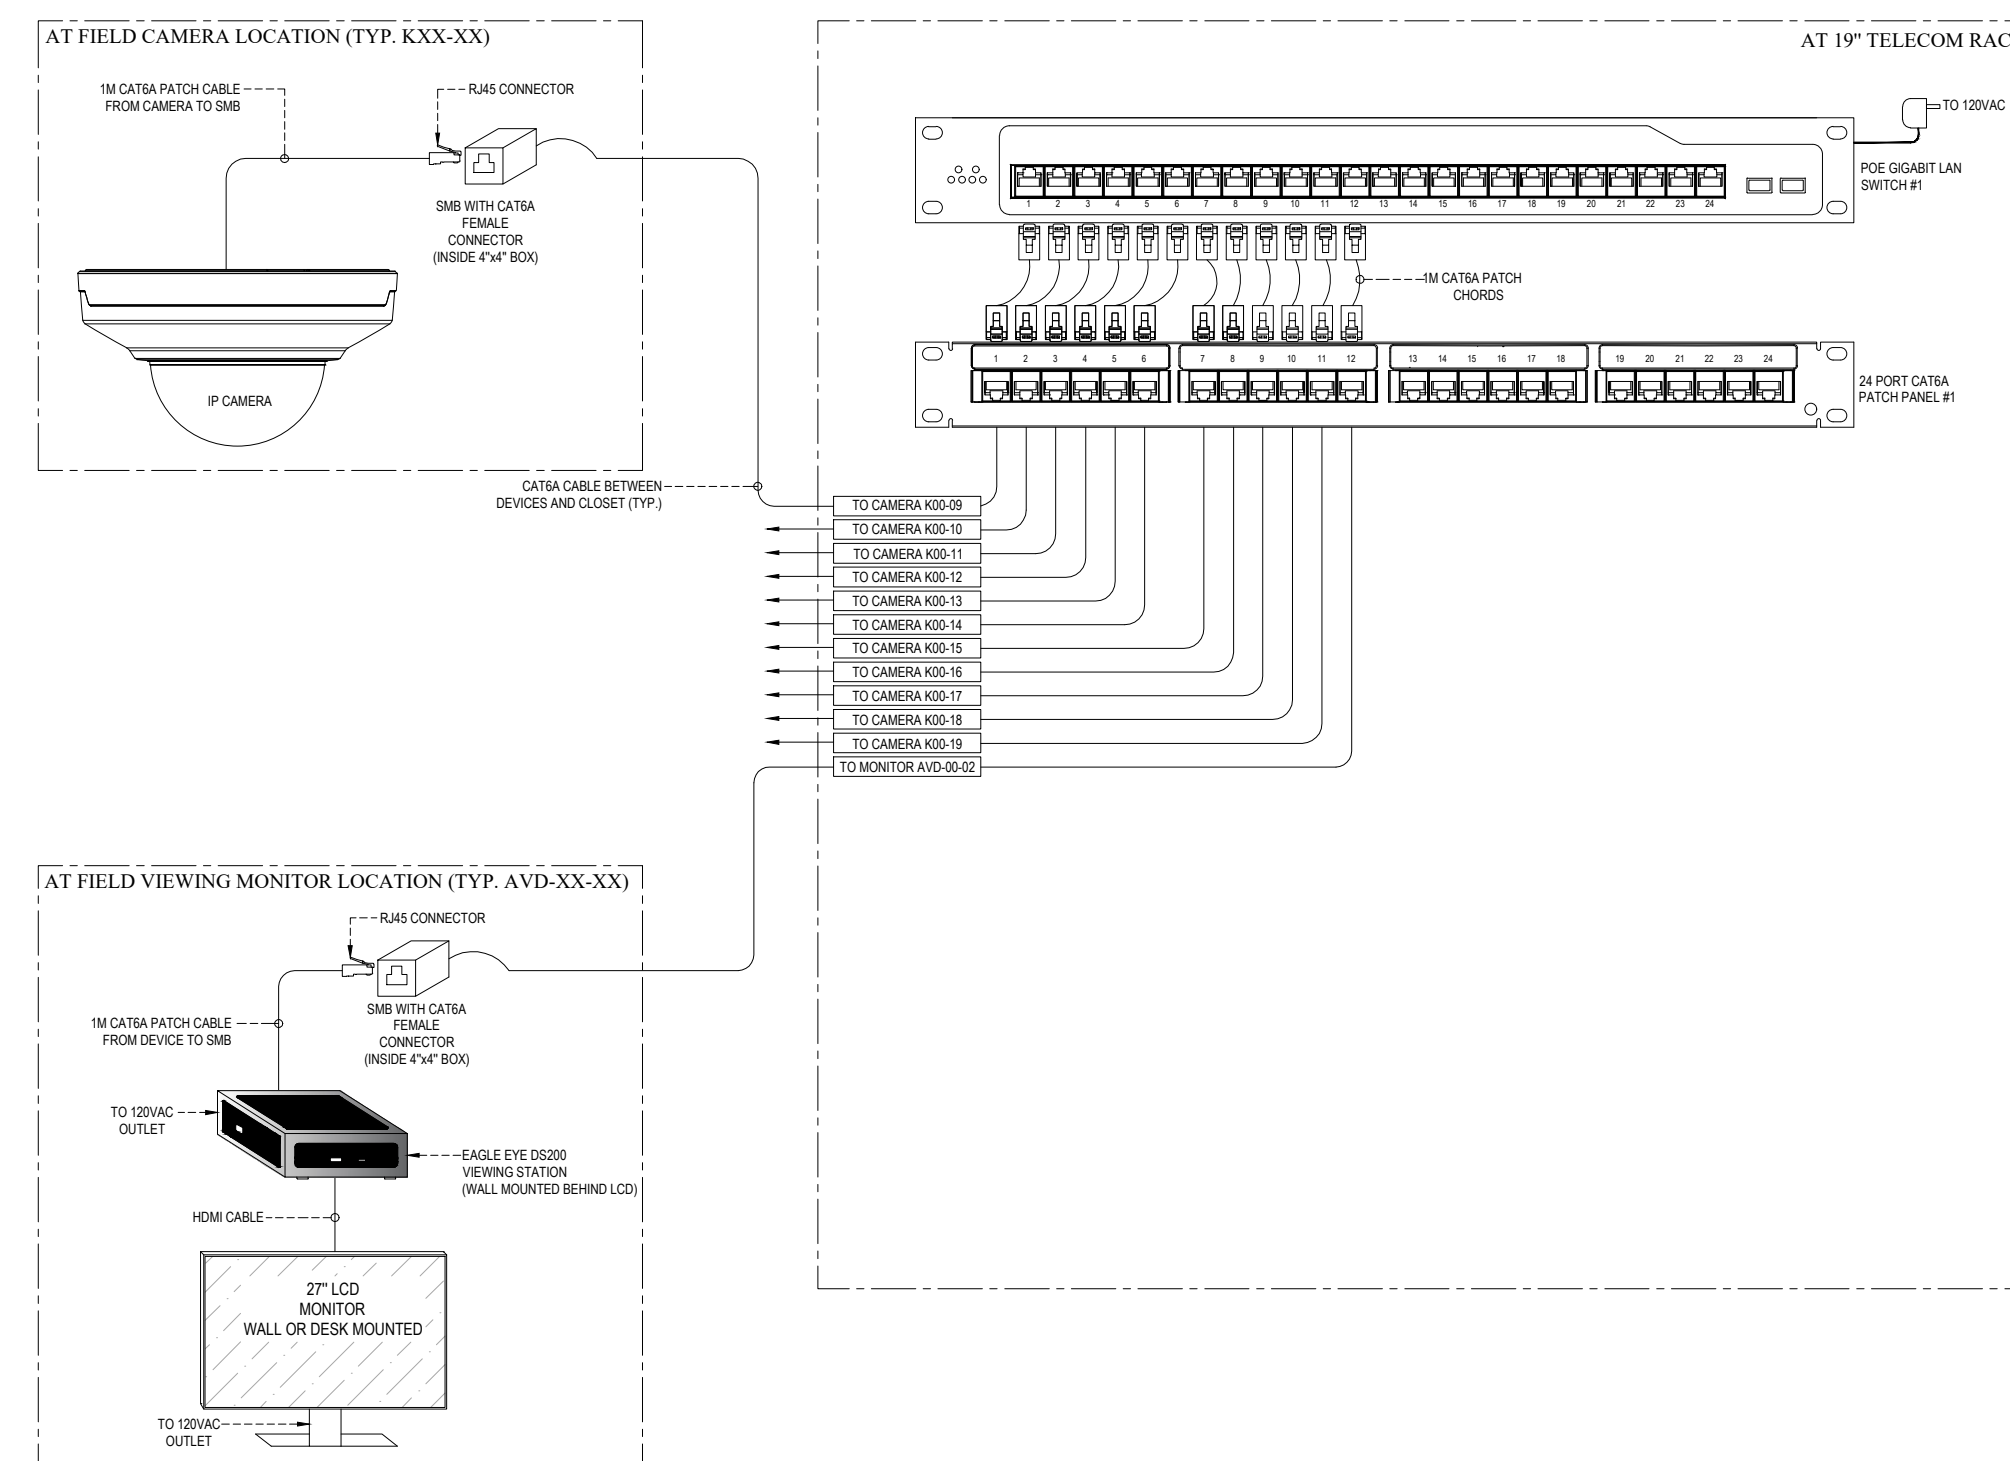

2

0.2 IDF (LOWER LEVEL NORTH)

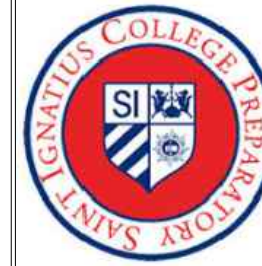

STAMP



DB STAMP

REV	DATE	DESCRIPTION
1	05/03/2024	STANISLAW SECURITY PLANS

ST. IGNATIUS COLLEGE PREPARATORY

2001 37th Ave. San Francisco, CA 94116

CAMERA SYSTEM POINT TO POINT DIAGRAM

T6.16A