
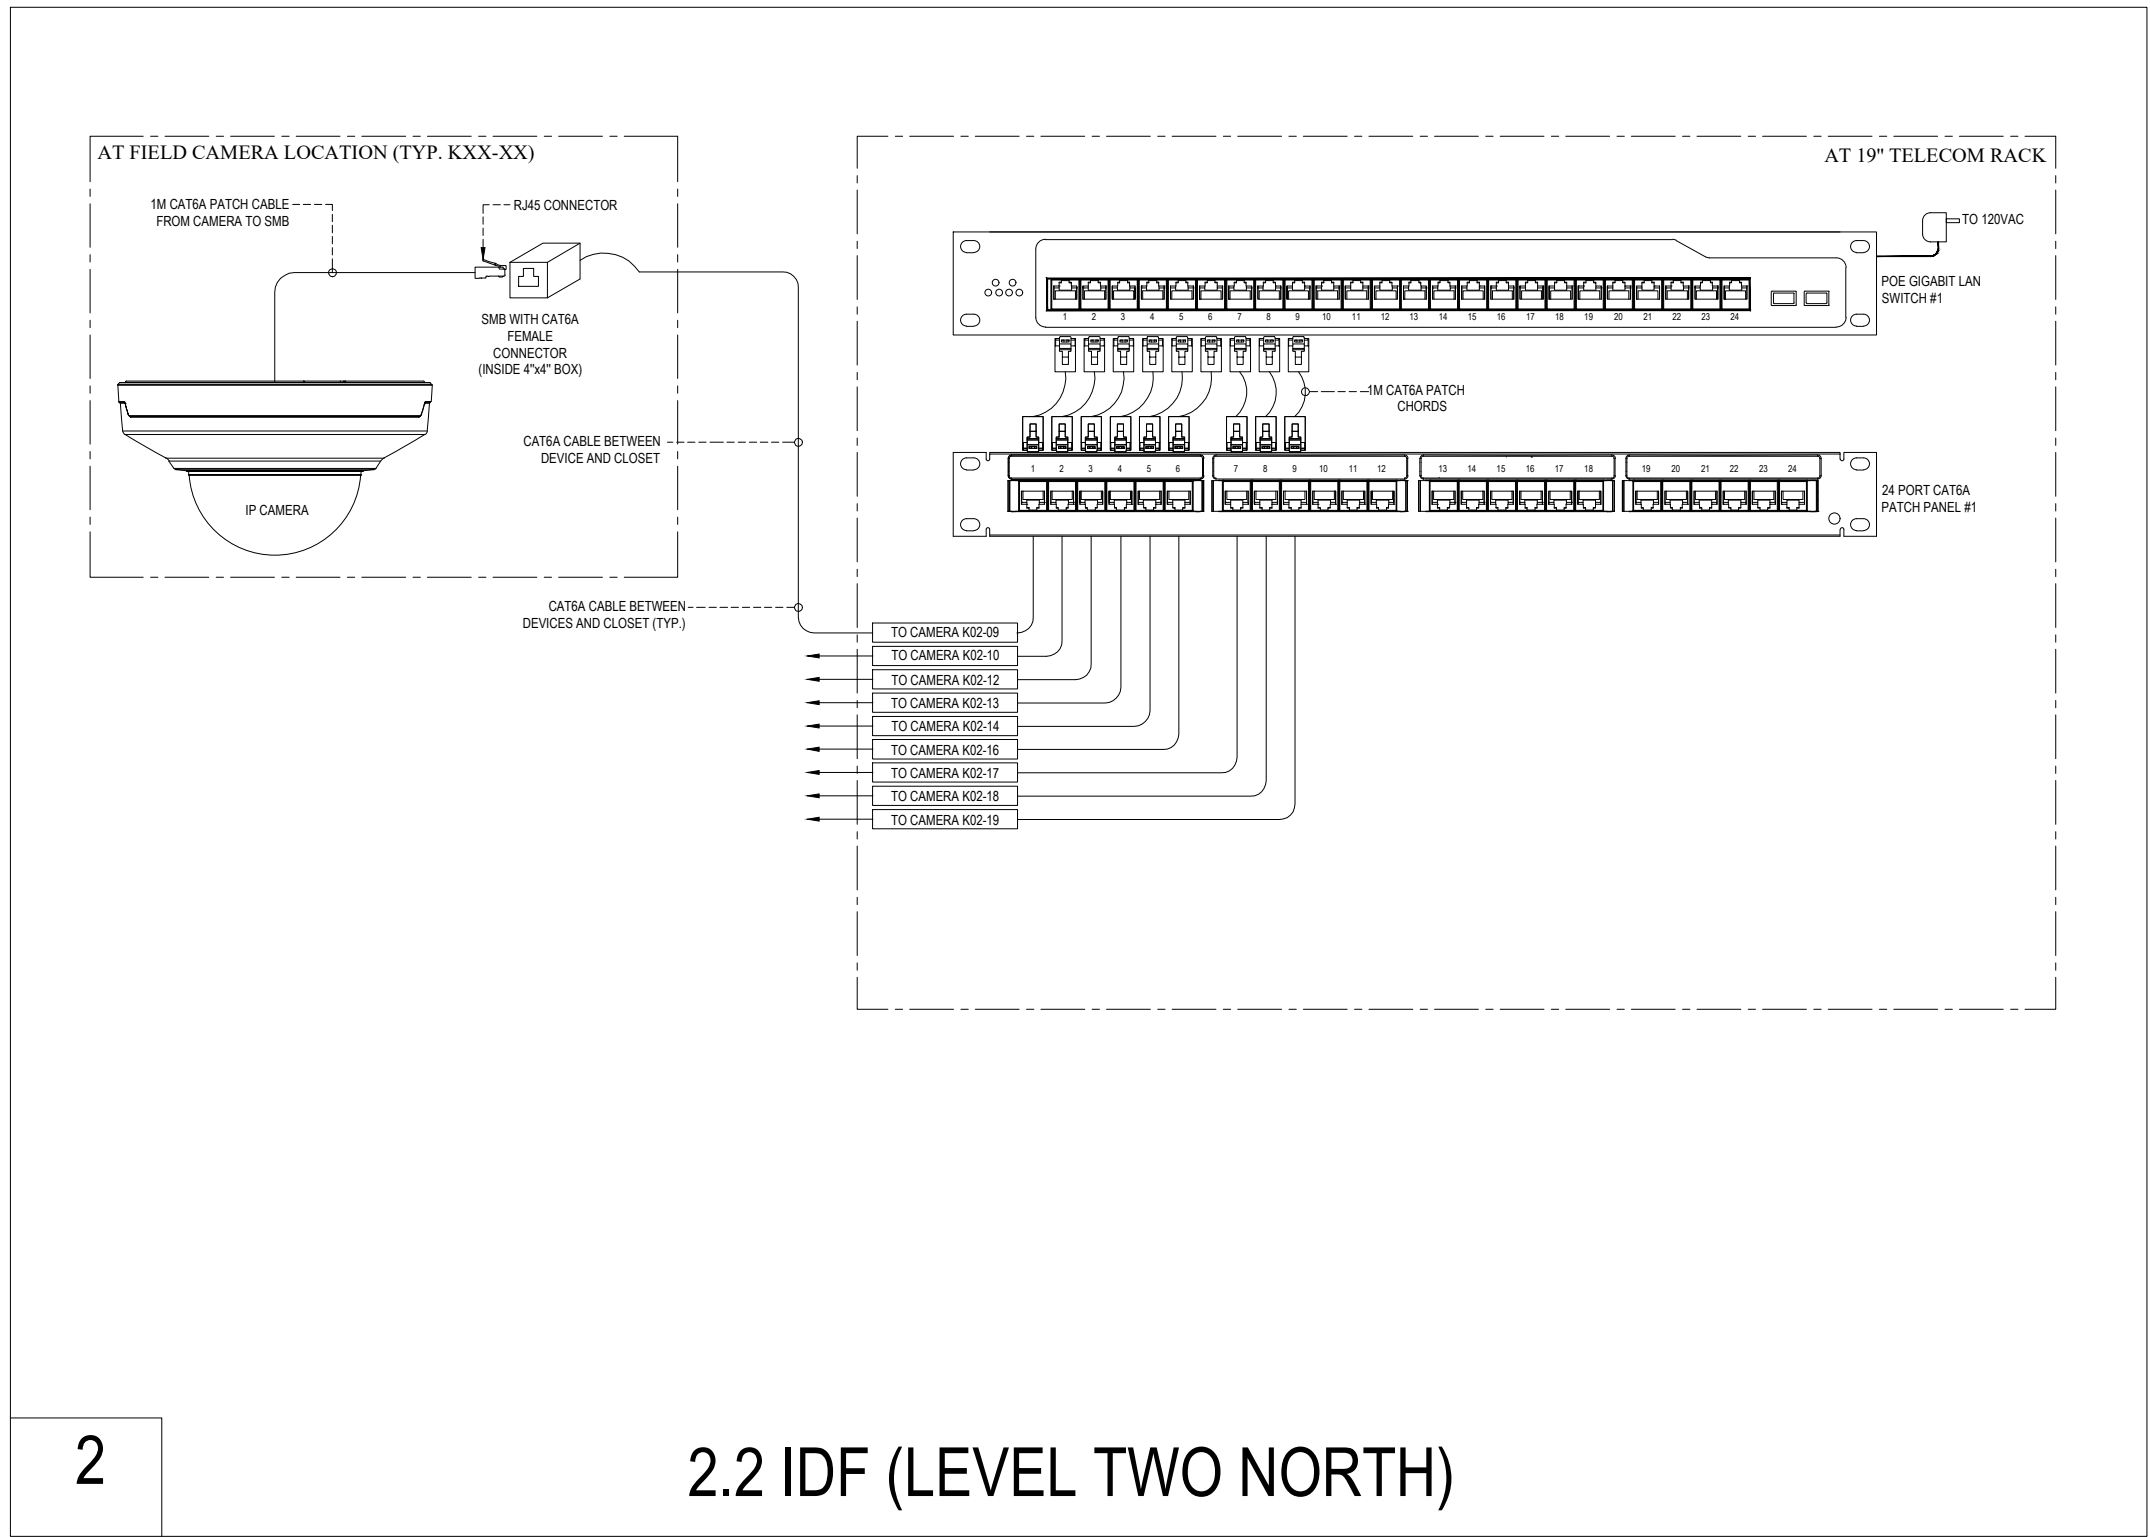
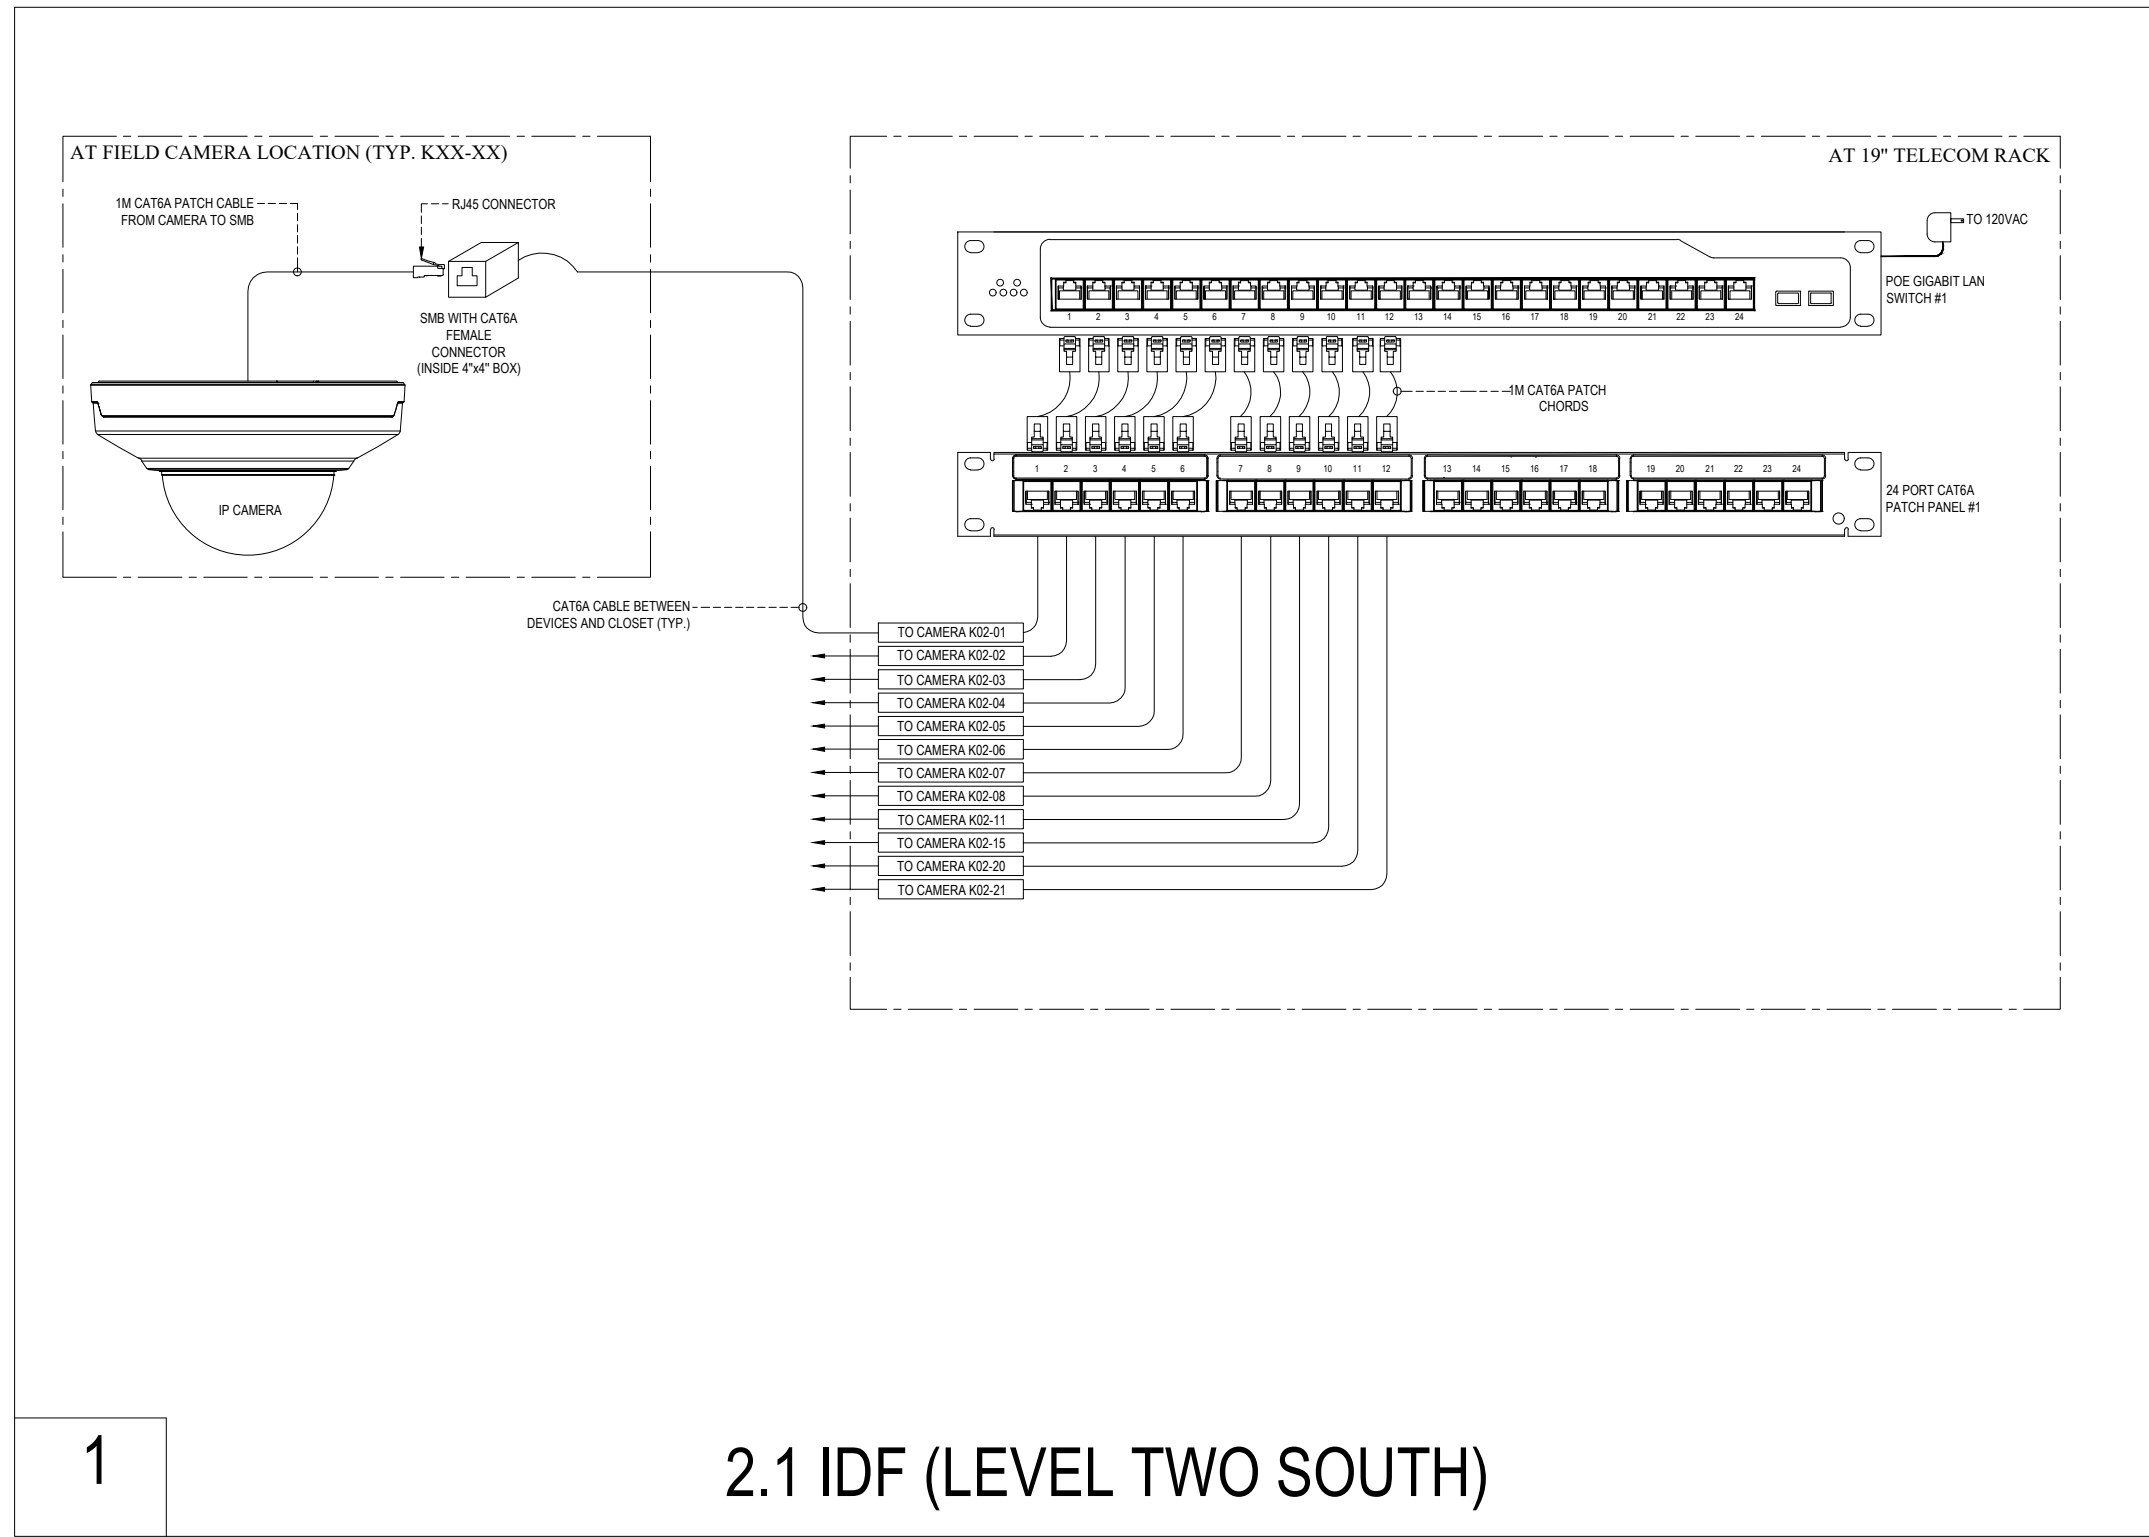
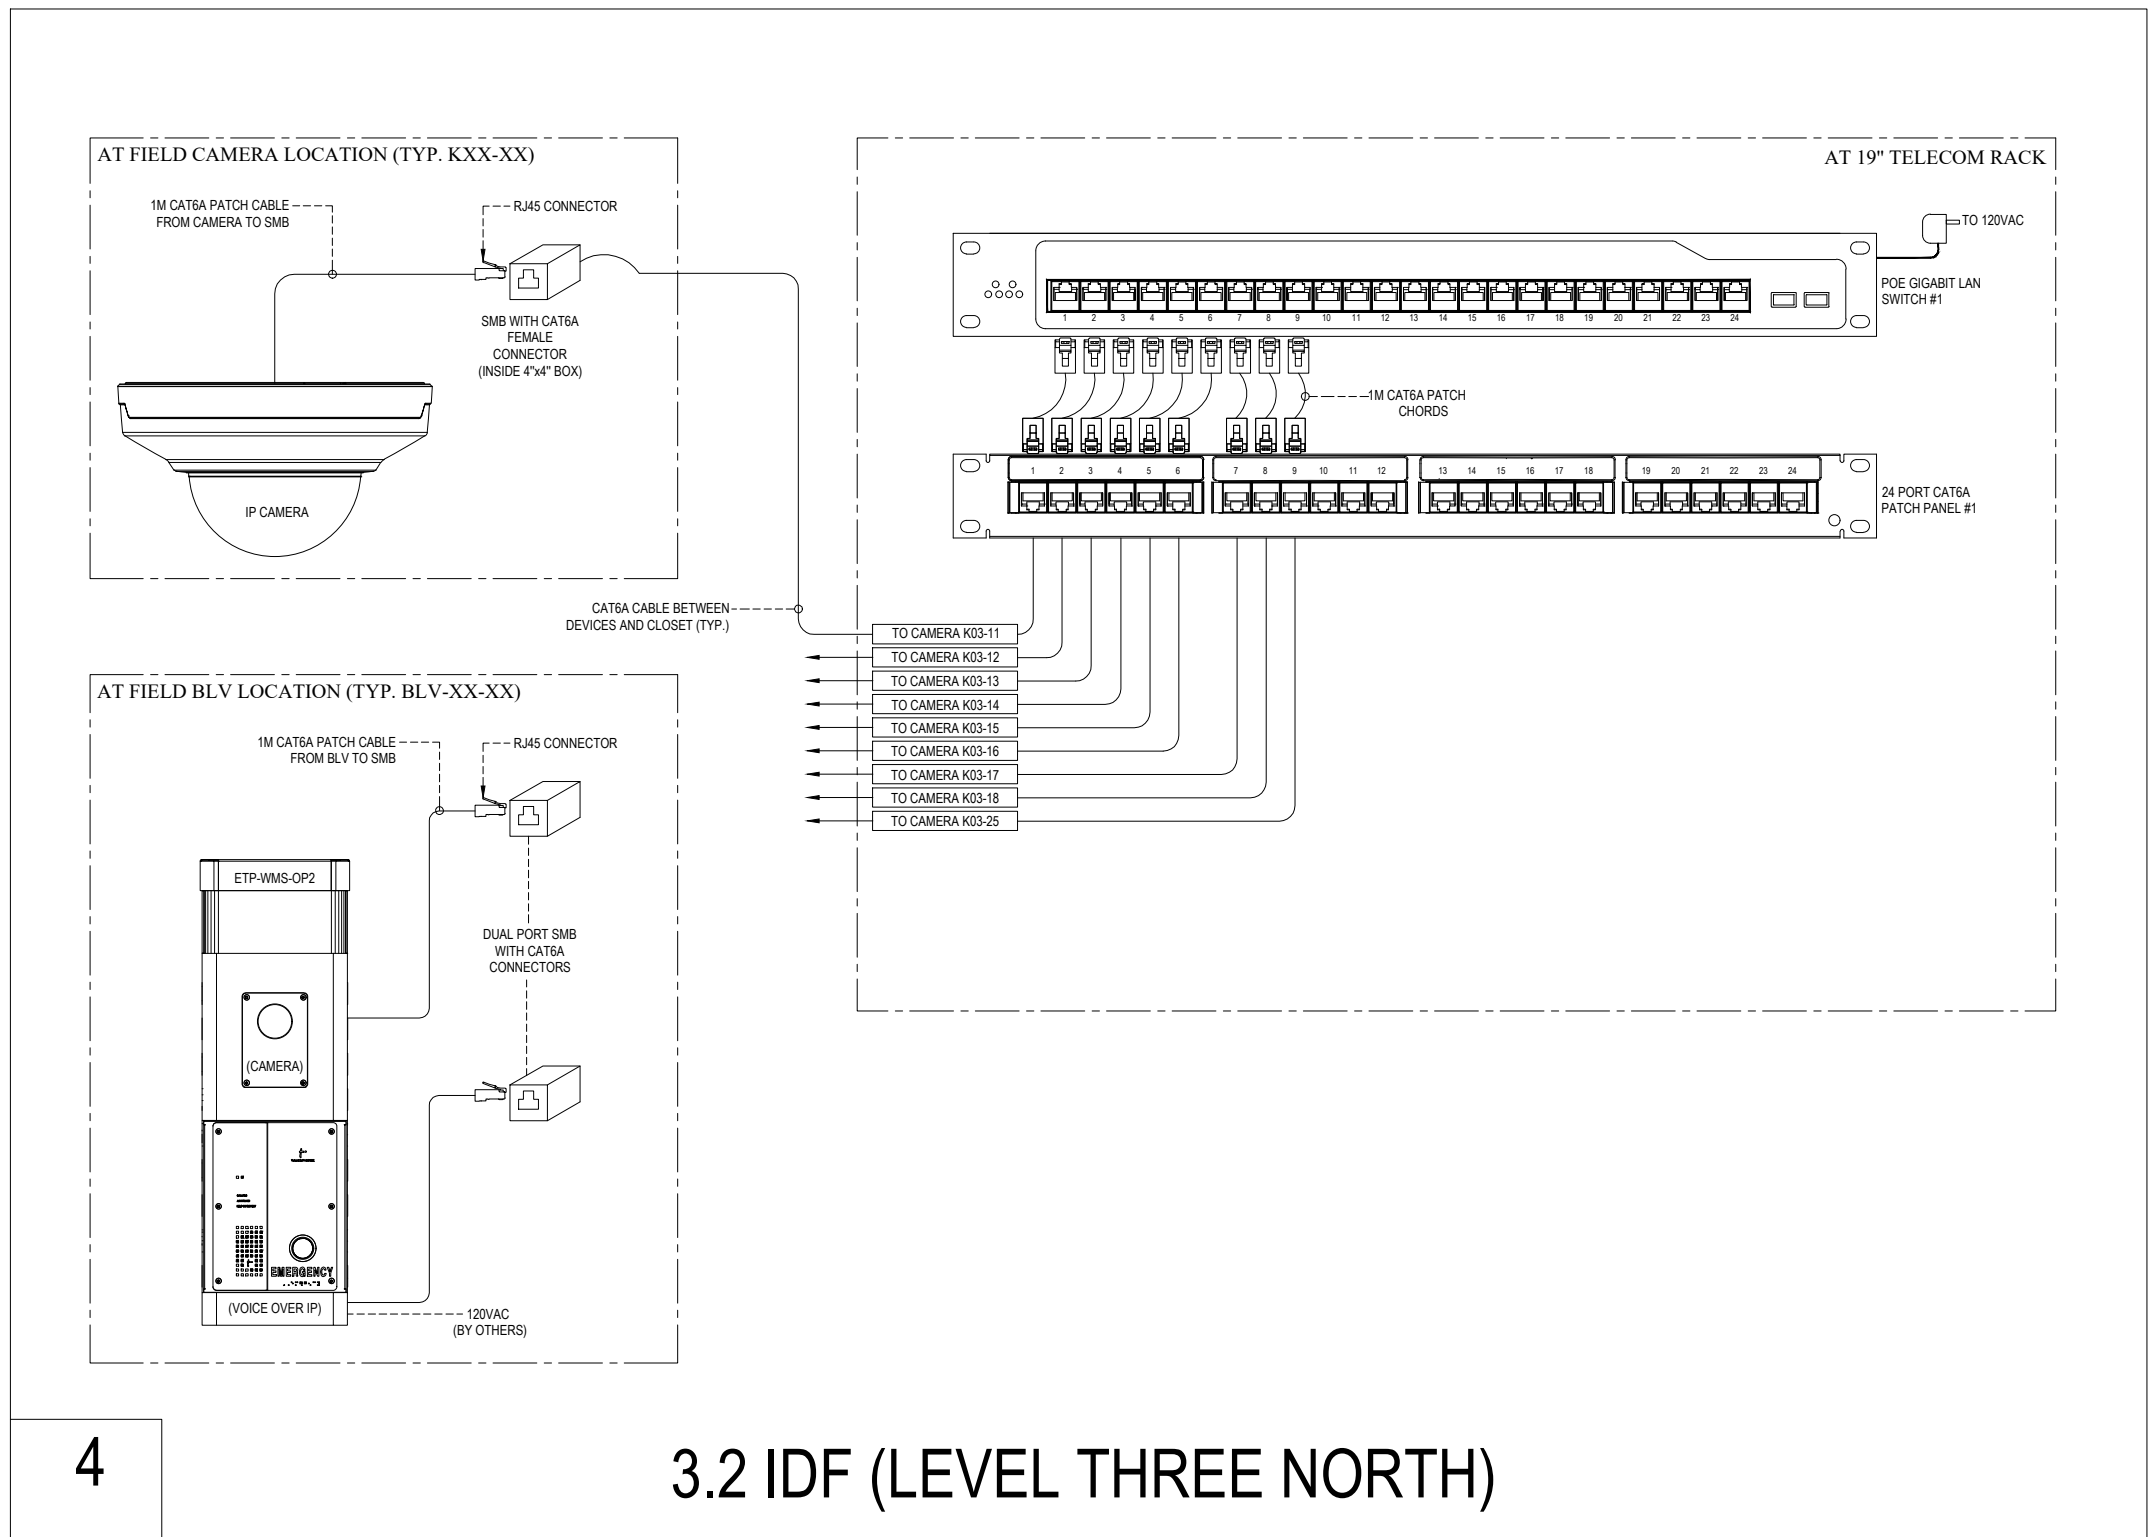


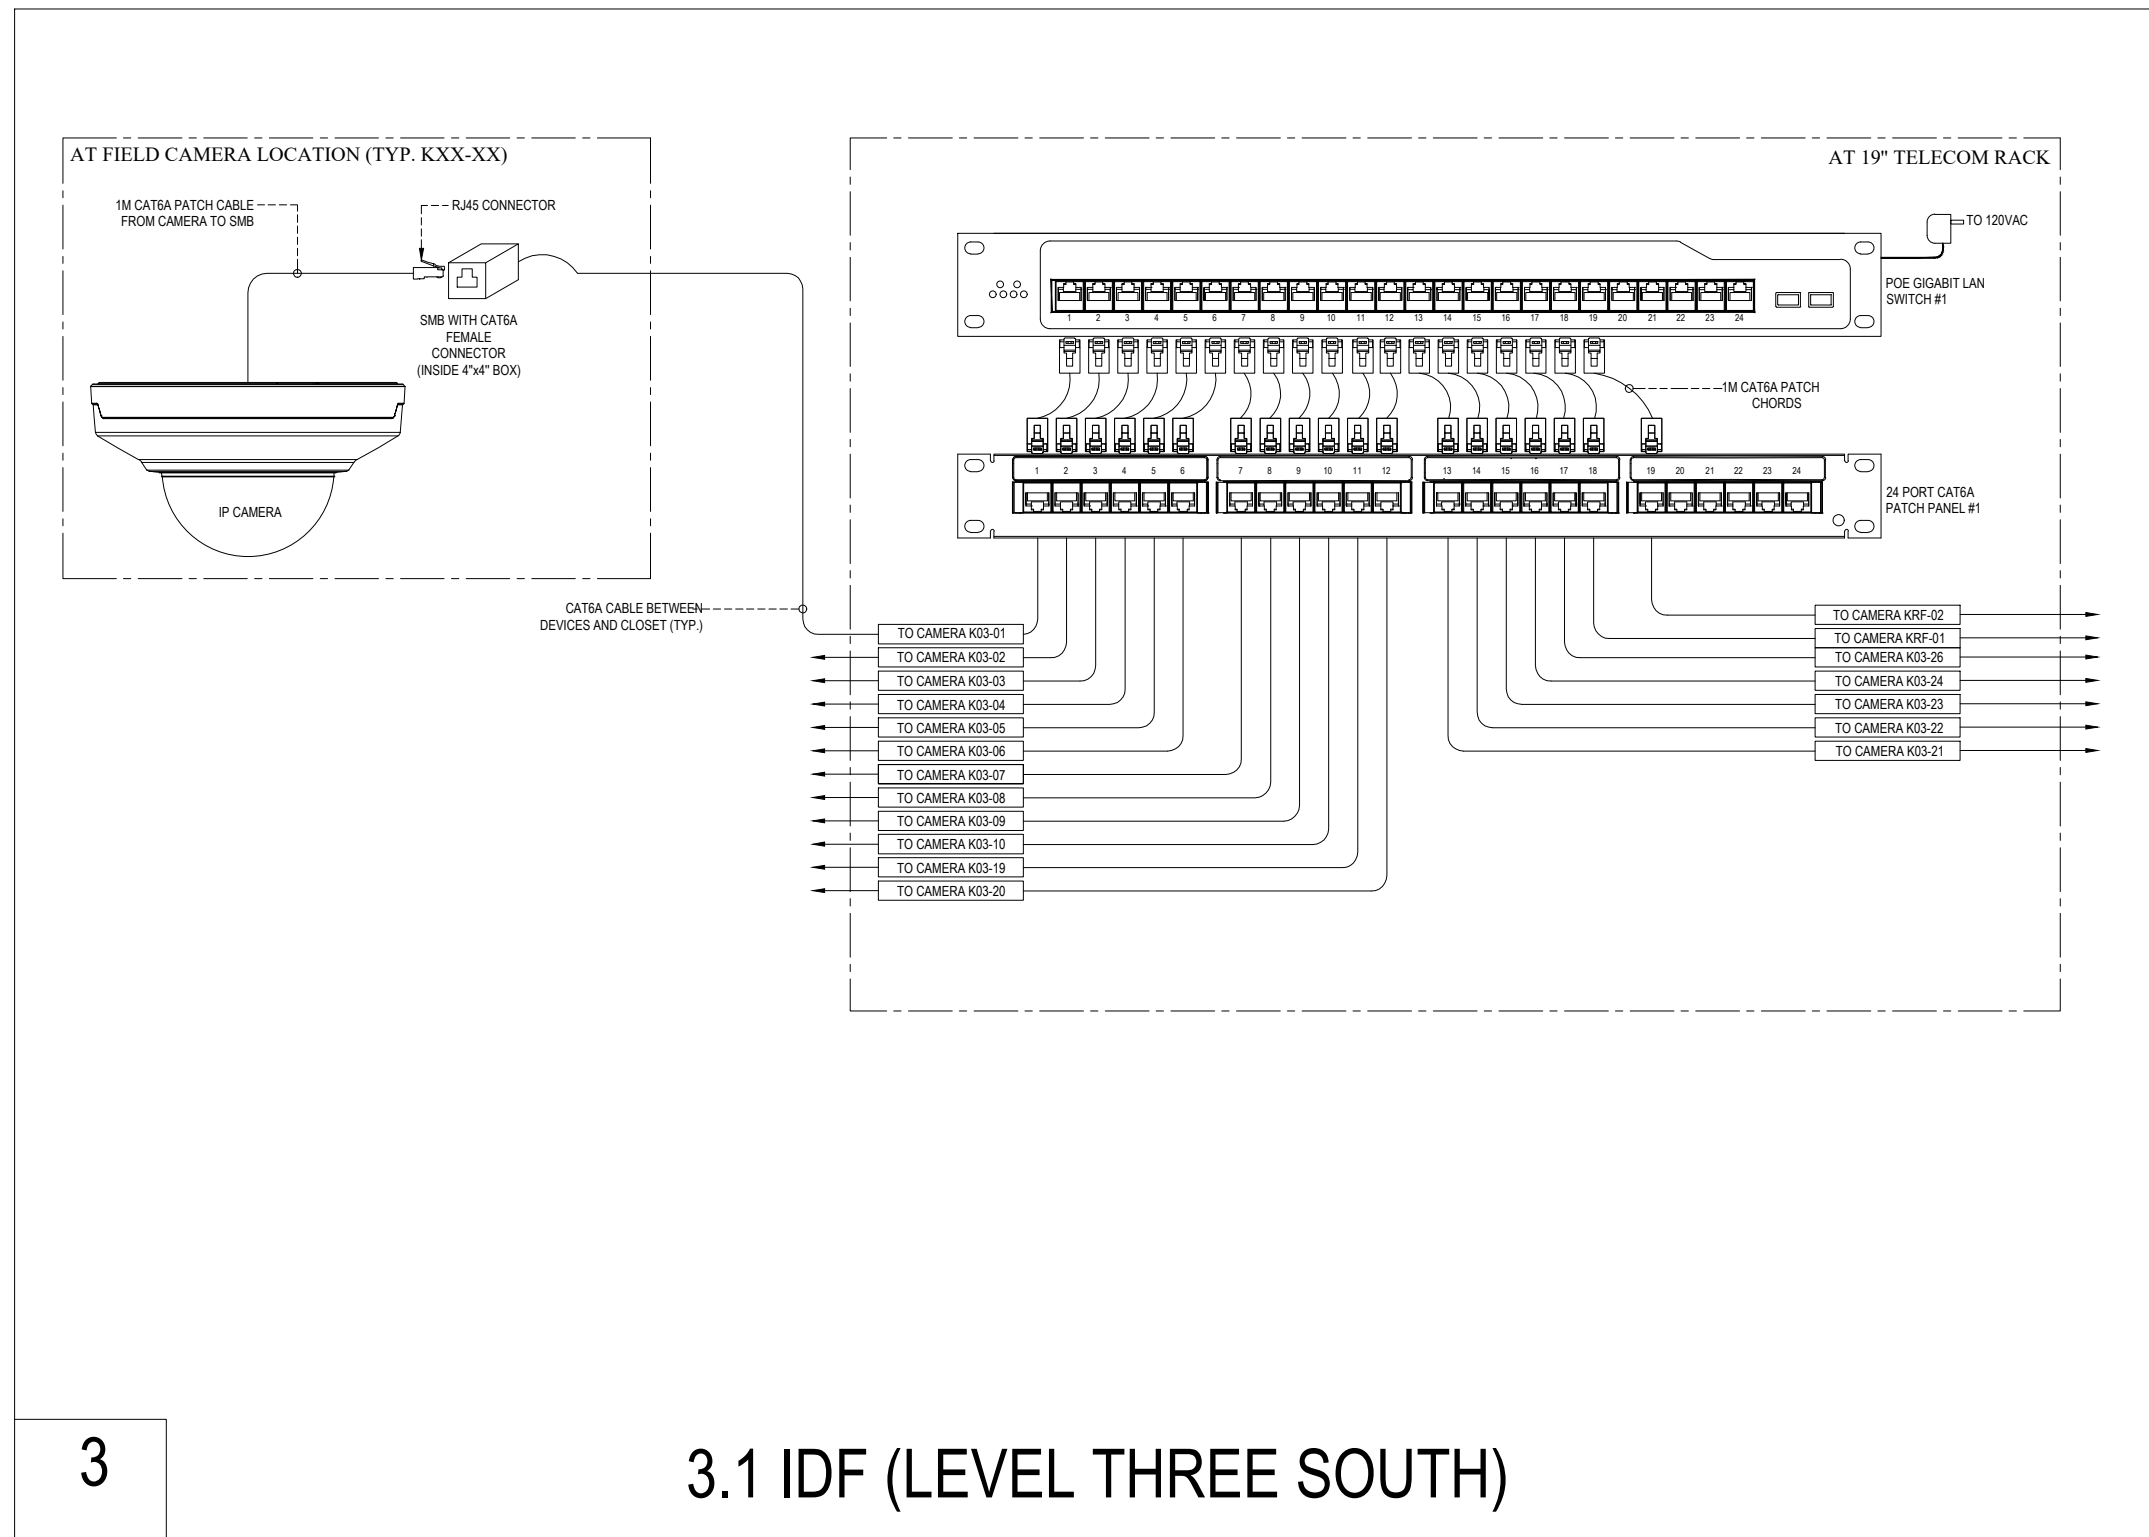

REV.	DATE	DESCRIPTION	DESIGNER	DATE	DESCRIPTION
1	05/03/2024	DYNAMIC SECURITY PLANS			

ST. IGNATIUS COLLEGE PREPARATORY

2001 37th Ave. San Francisco, CA 94116

CAMERA SYSTEM POINT TO POINT DIAGRAM