

7/1/2024 4:26:04 PM









0.1 MDF
ACP ENCLOSURE
LSP-DV250-M

DRAWING NOT TO SCALE

0.1 MDF LOWER LEVEL SOUTH

6" x 6" WIRE GUTTER

900 MHz (AES 128 BIT)
ENCRYPTED WIRELESS
COMMUNICATION

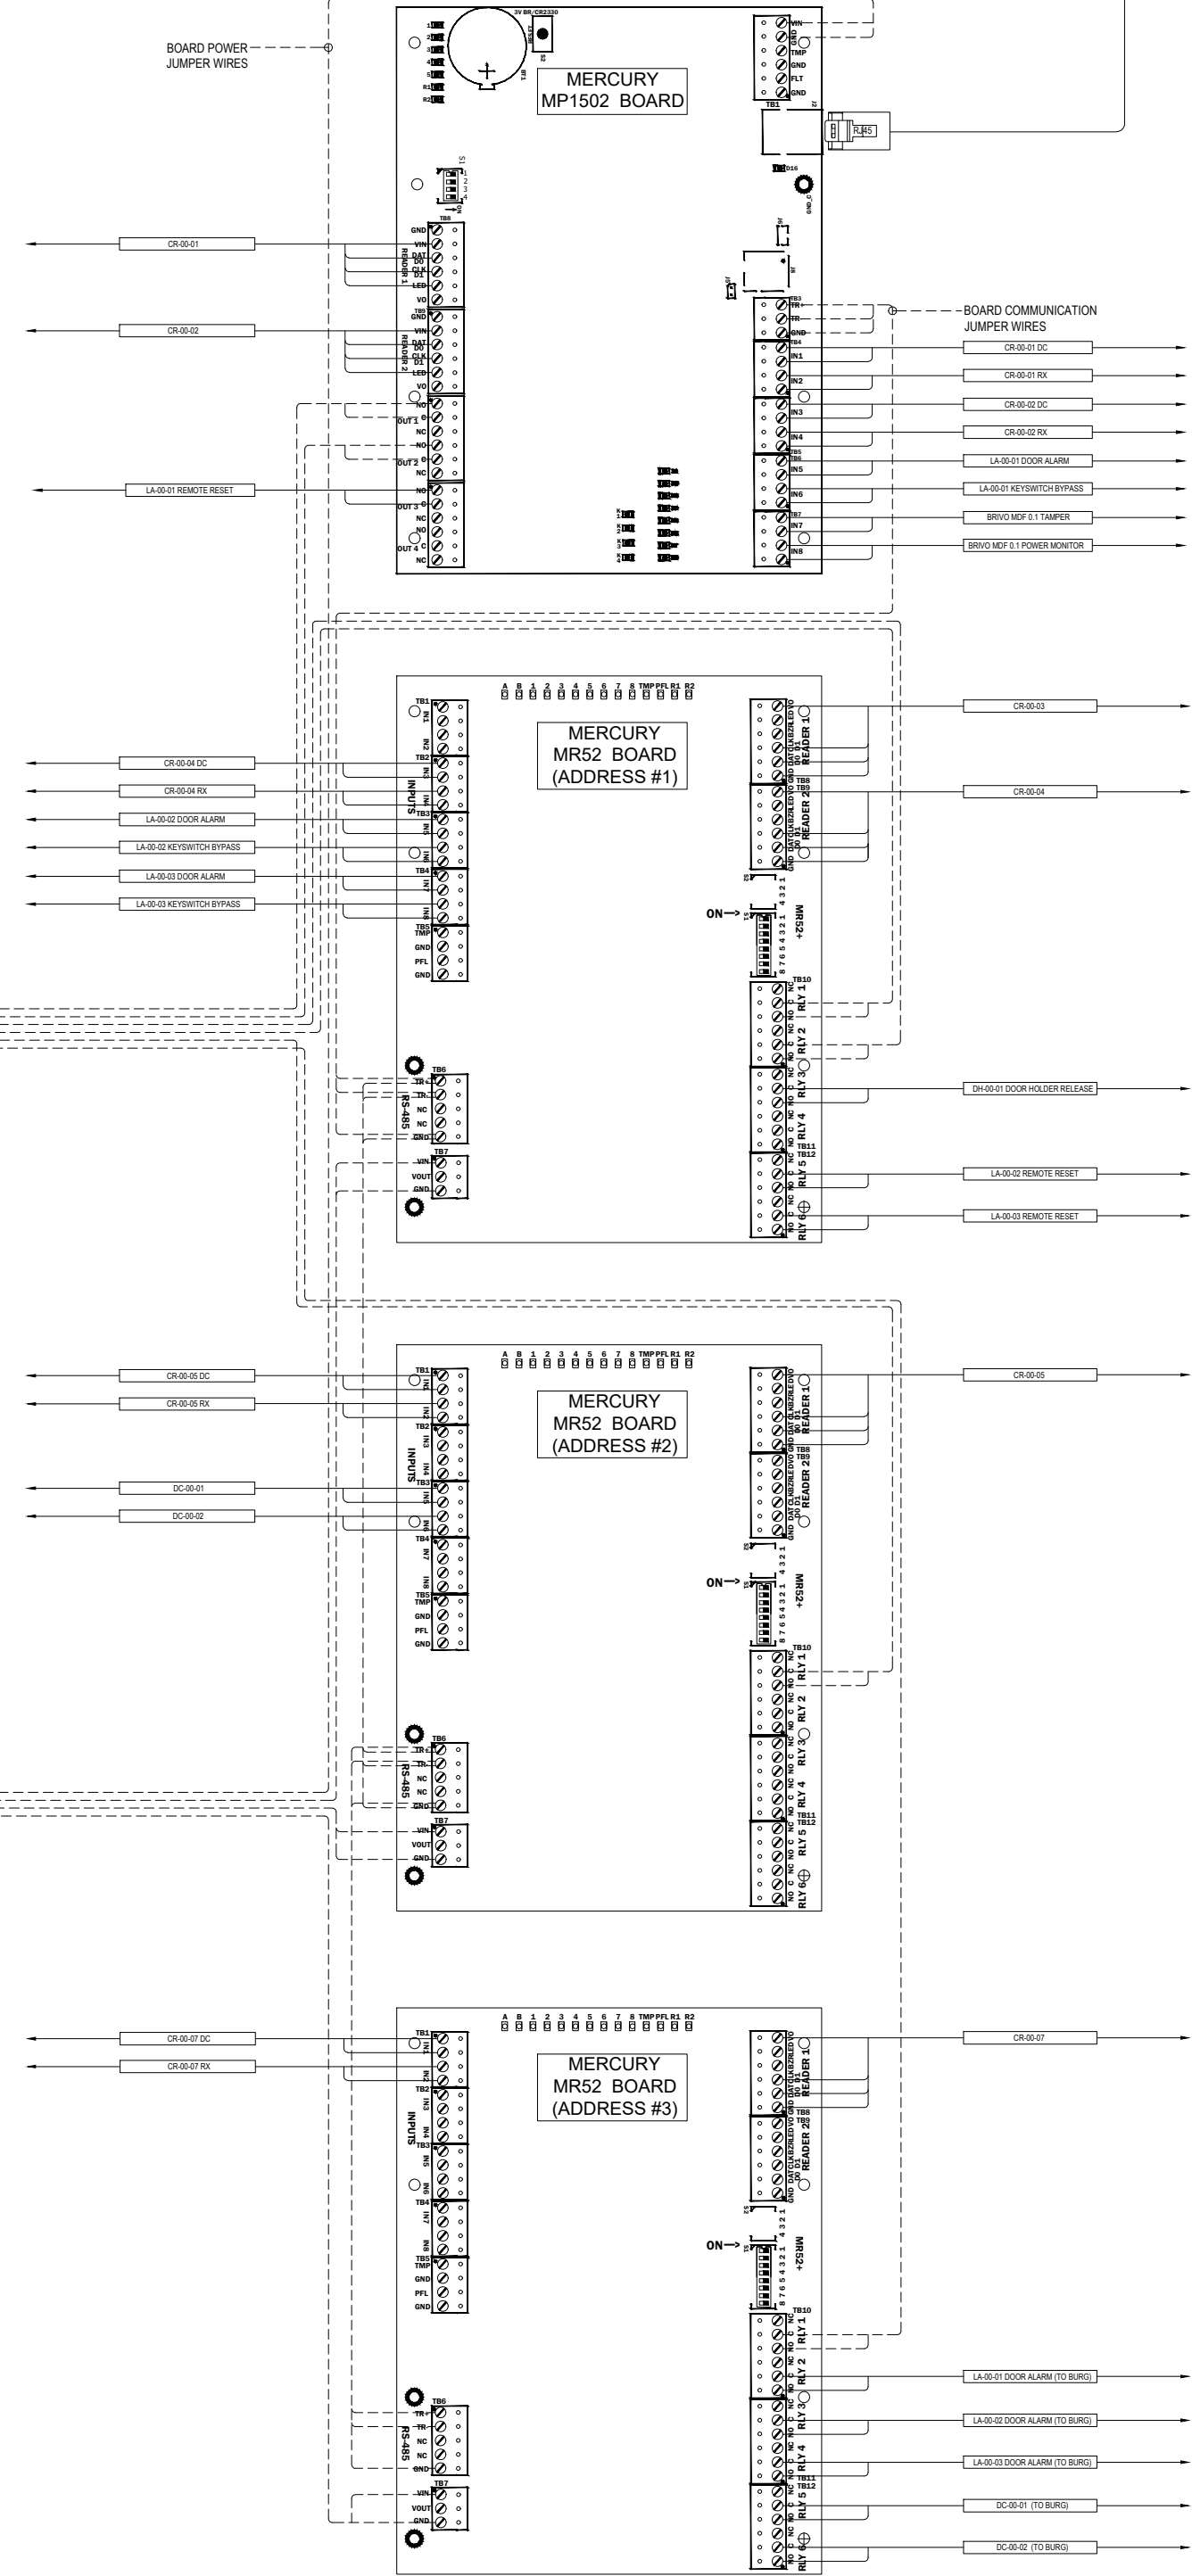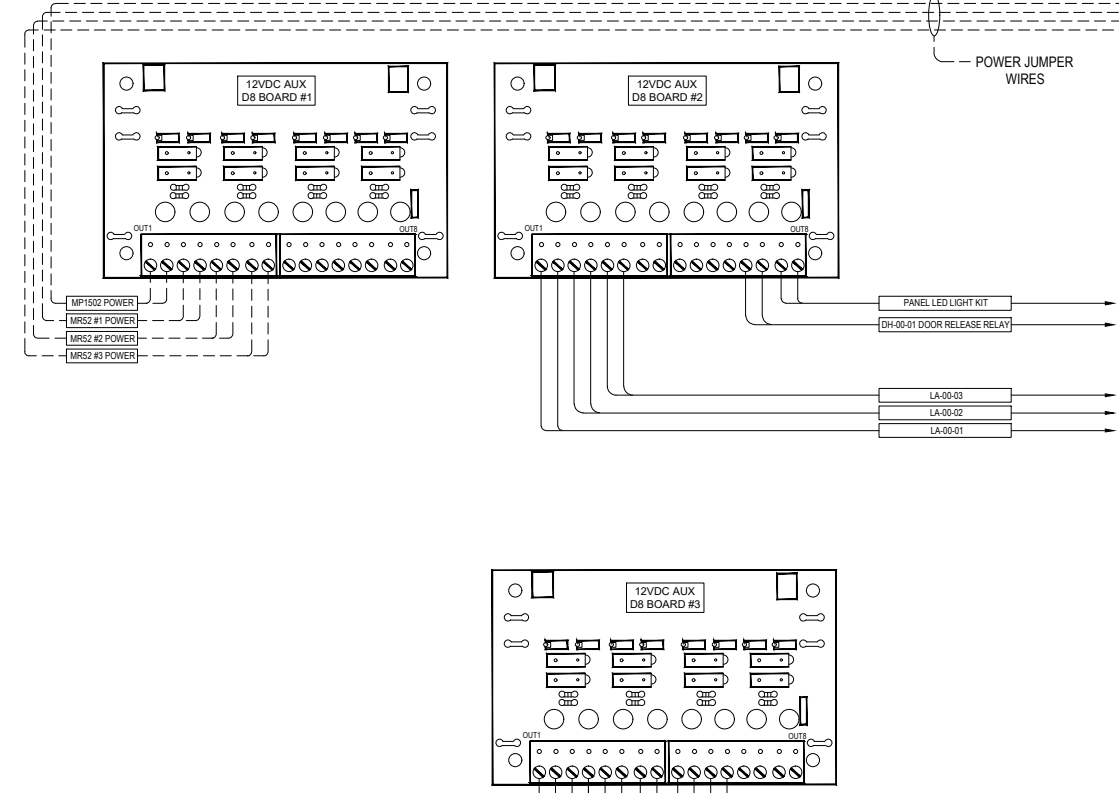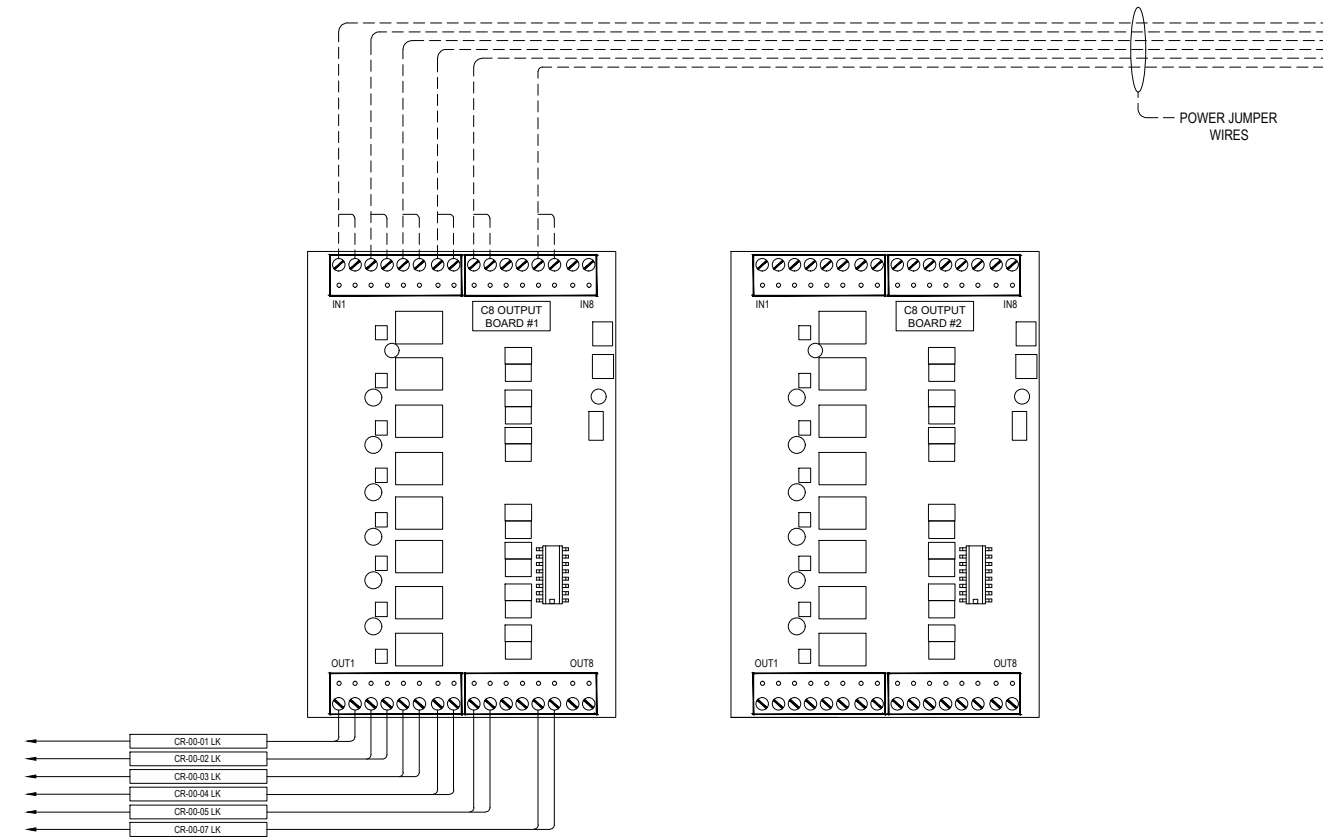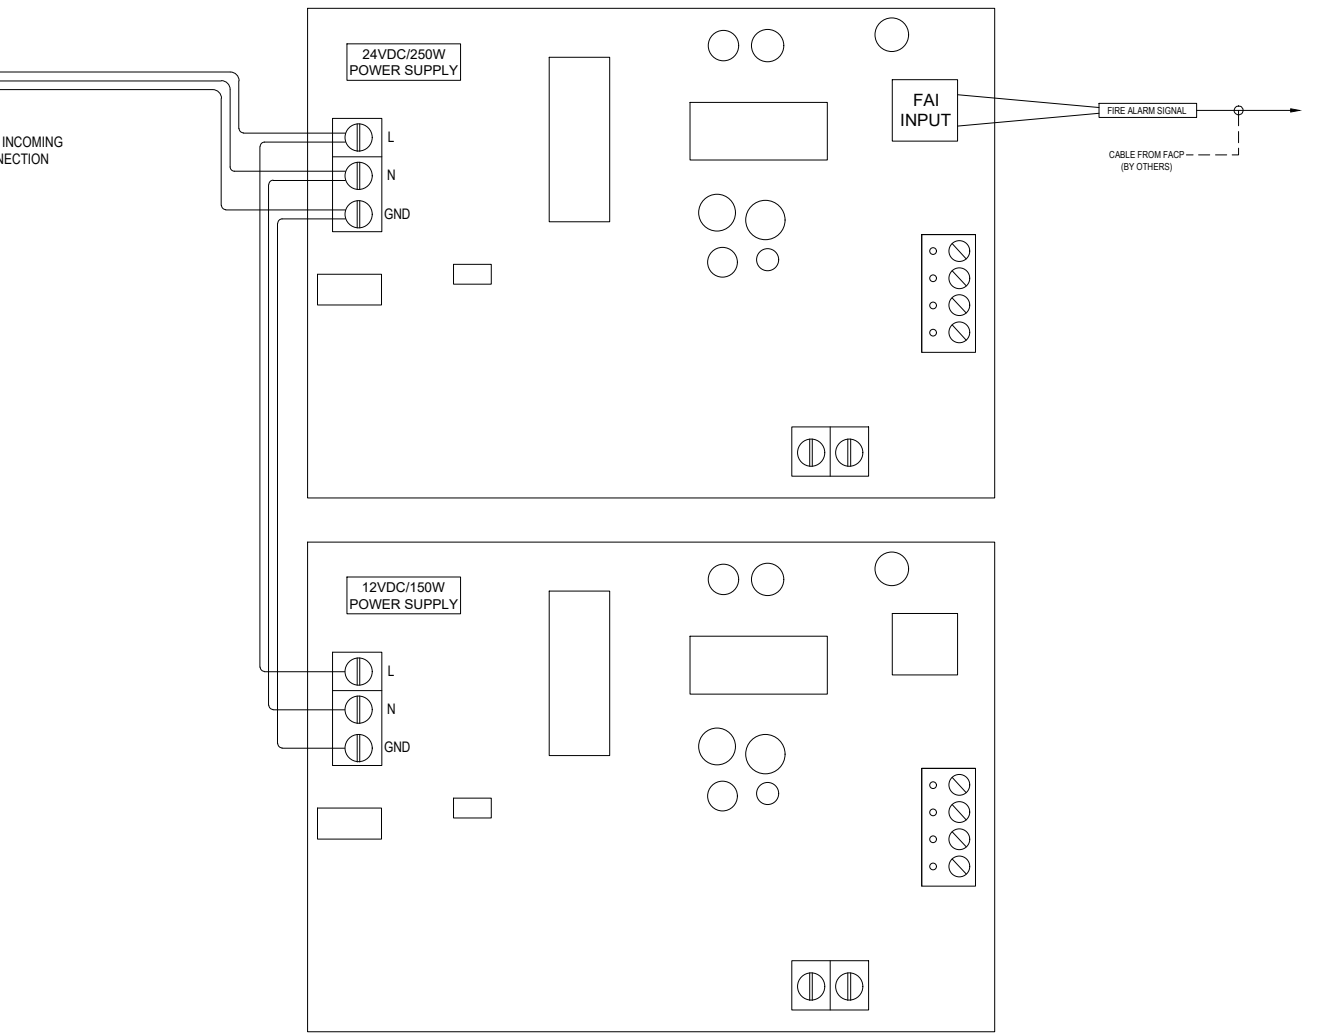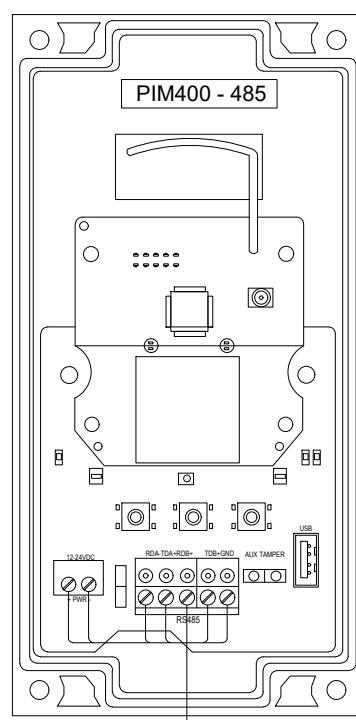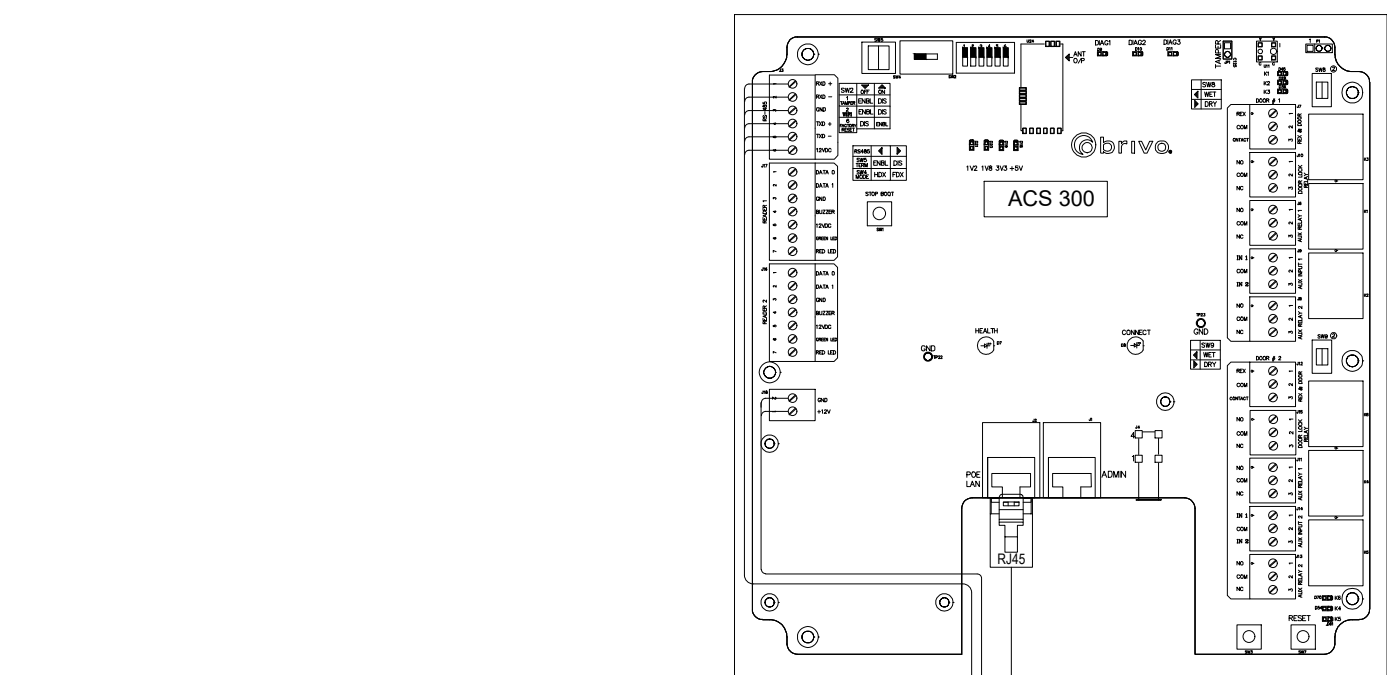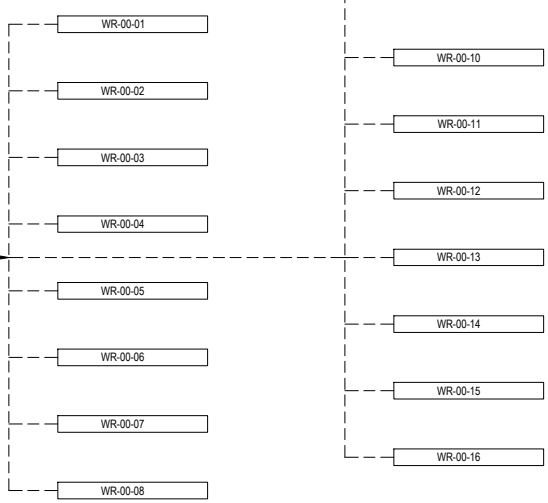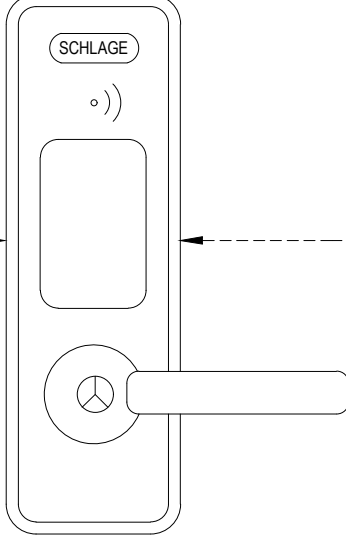

FUTURE
SLOT

FUTURE
SLOT

FUTURE
SLOT

FUTURE
SLOT

(2) CAT5A FROM
PATCH PANEL

(2) CAT5A FROM
TELECOM



STAMP



DB STAMP

REV	DATE	DESCRIPTION
01	05/05/2024	DYNAMIC SECURITY PLANS

ST. IGNATIUS COLLEGE PREPARATORY

2001 37th Ave. San Francisco, CA 94116

ACCESS CONTROL SYSTEM POINT TO POINT DIAGRAM

T6.17A