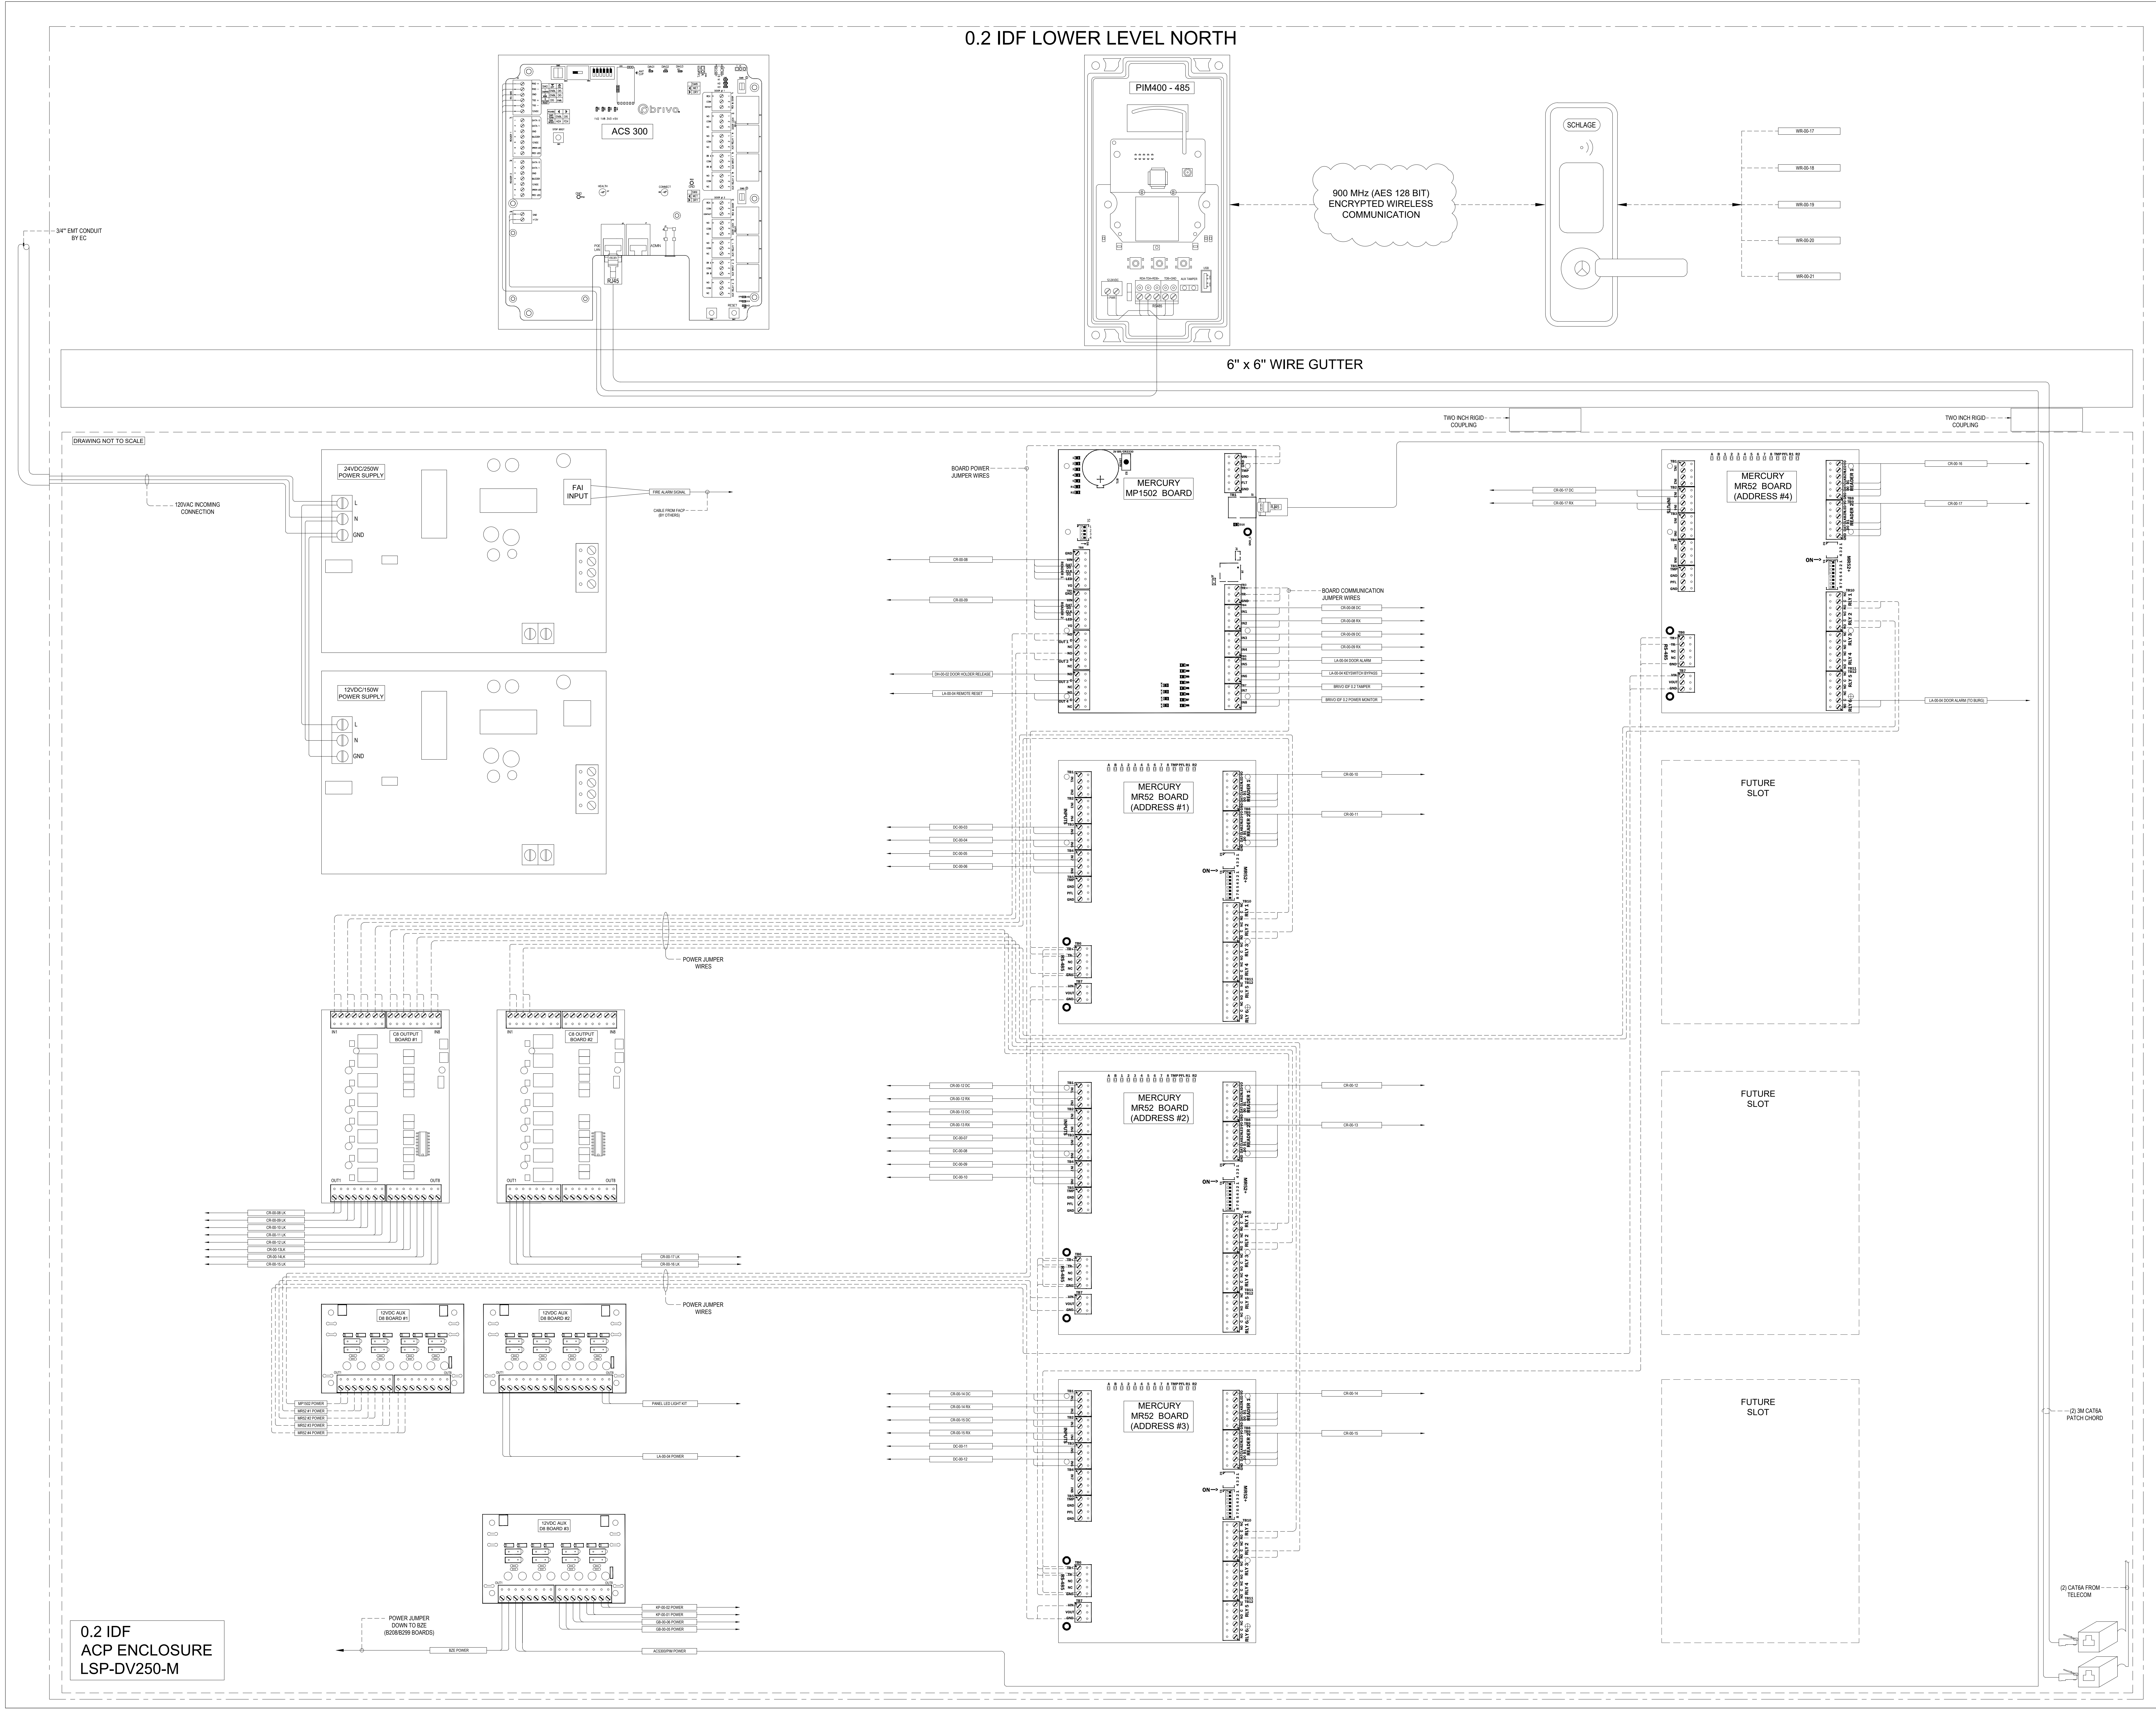

7/1/2026 4:26:04 PM

STAMP

CONSULTANT LOGO

TEECOM
50 California Street
Suite 1500
San Francisco, CA
94111
(510) 337 2800
www.teecom.com

DBI STAMP

REV	DATE	DESCRIPTION
	09/30/2026	DYNAMIC SECURITY PLANS

ST. IGNATIUS COLLEGE PREPARATORY
2001 37th Ave, San Francisco, CA 94116

ACCESS CONTROL SYSTEM POINT TO POINT DIAGRAM

T6.17B