


7/1/2024 4:26:04 PM

1.1 IDF
ACP ENCLOSURE
LSP-DV250-M

1.1 IDF LEVEL ONE SOUTH

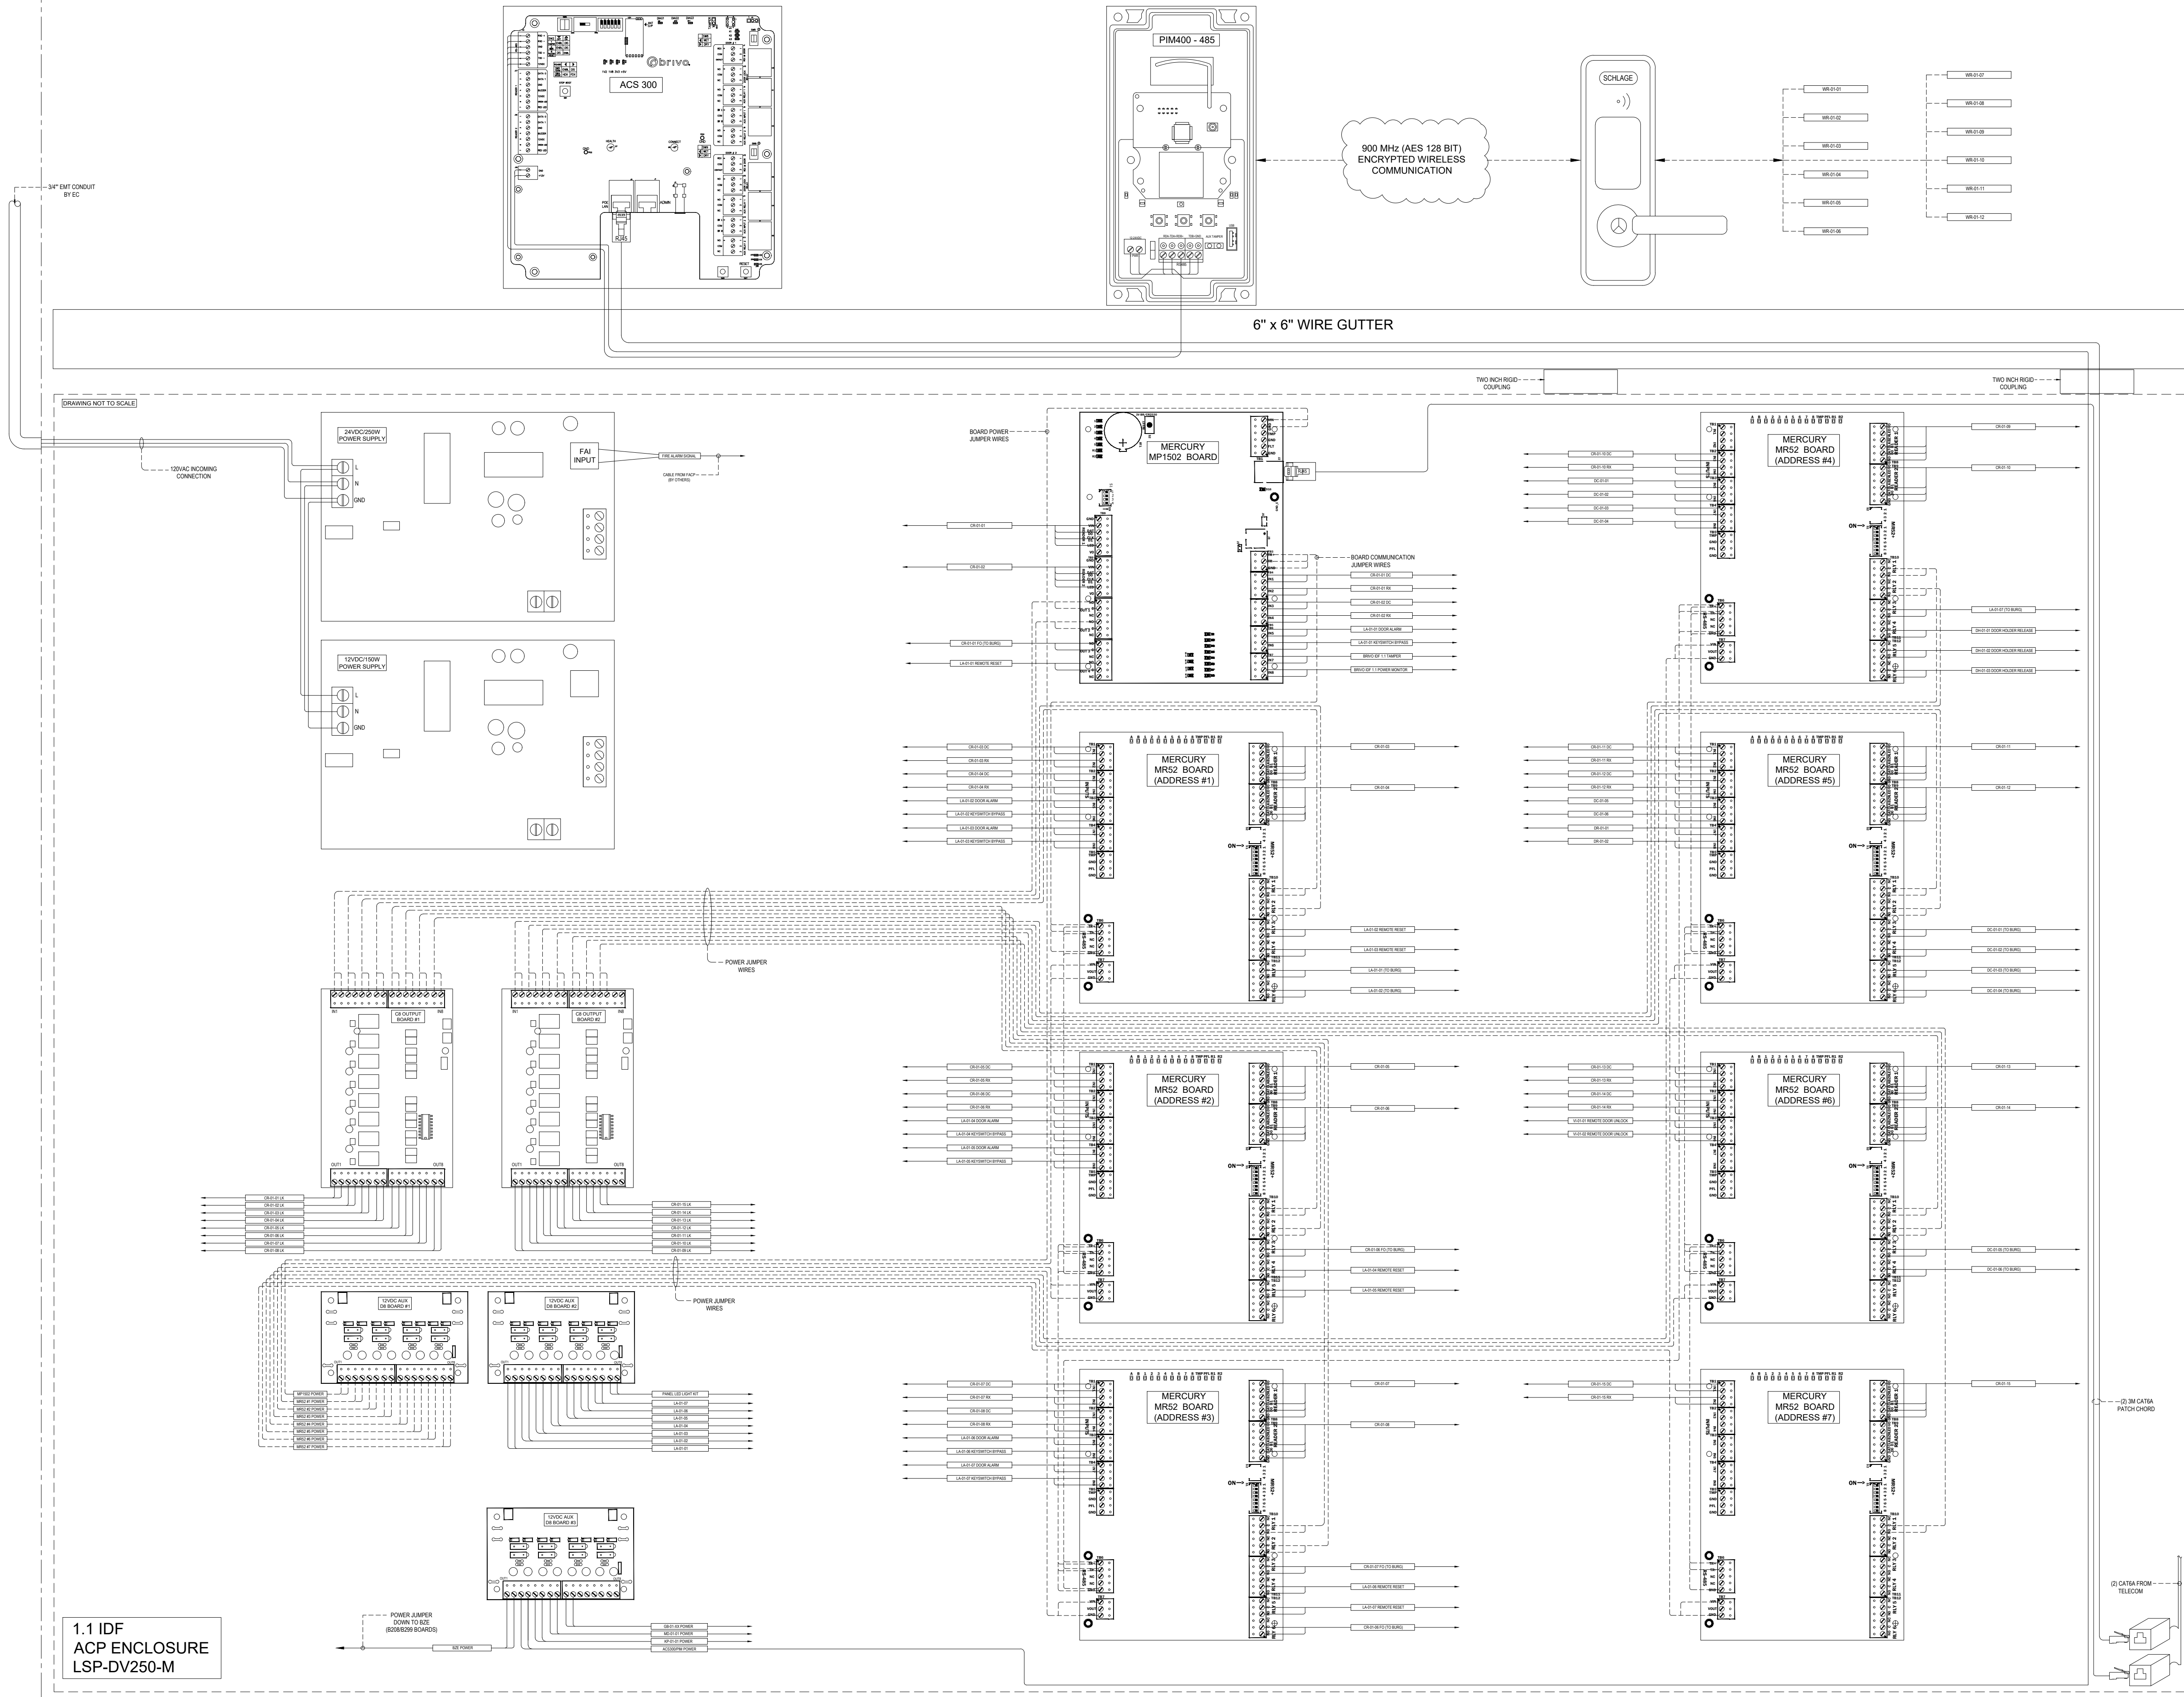

STAMP



DB STAMP

DATE: 05/05/2024
DESCRIPTION: DYNAMIC SECURITY PLANS

ST. IGNATIUS COLLEGE PREPARATORY

ACCESS CONTROL SYSTEM POINT TO POINT DIAGRAM

2001 37th Ave, San Francisco, CA 94116

T6.17C