


7/11/2024 4:26:04 PM

1.2 IDF
ACP ENCLOSURE
LSP-DV250-M

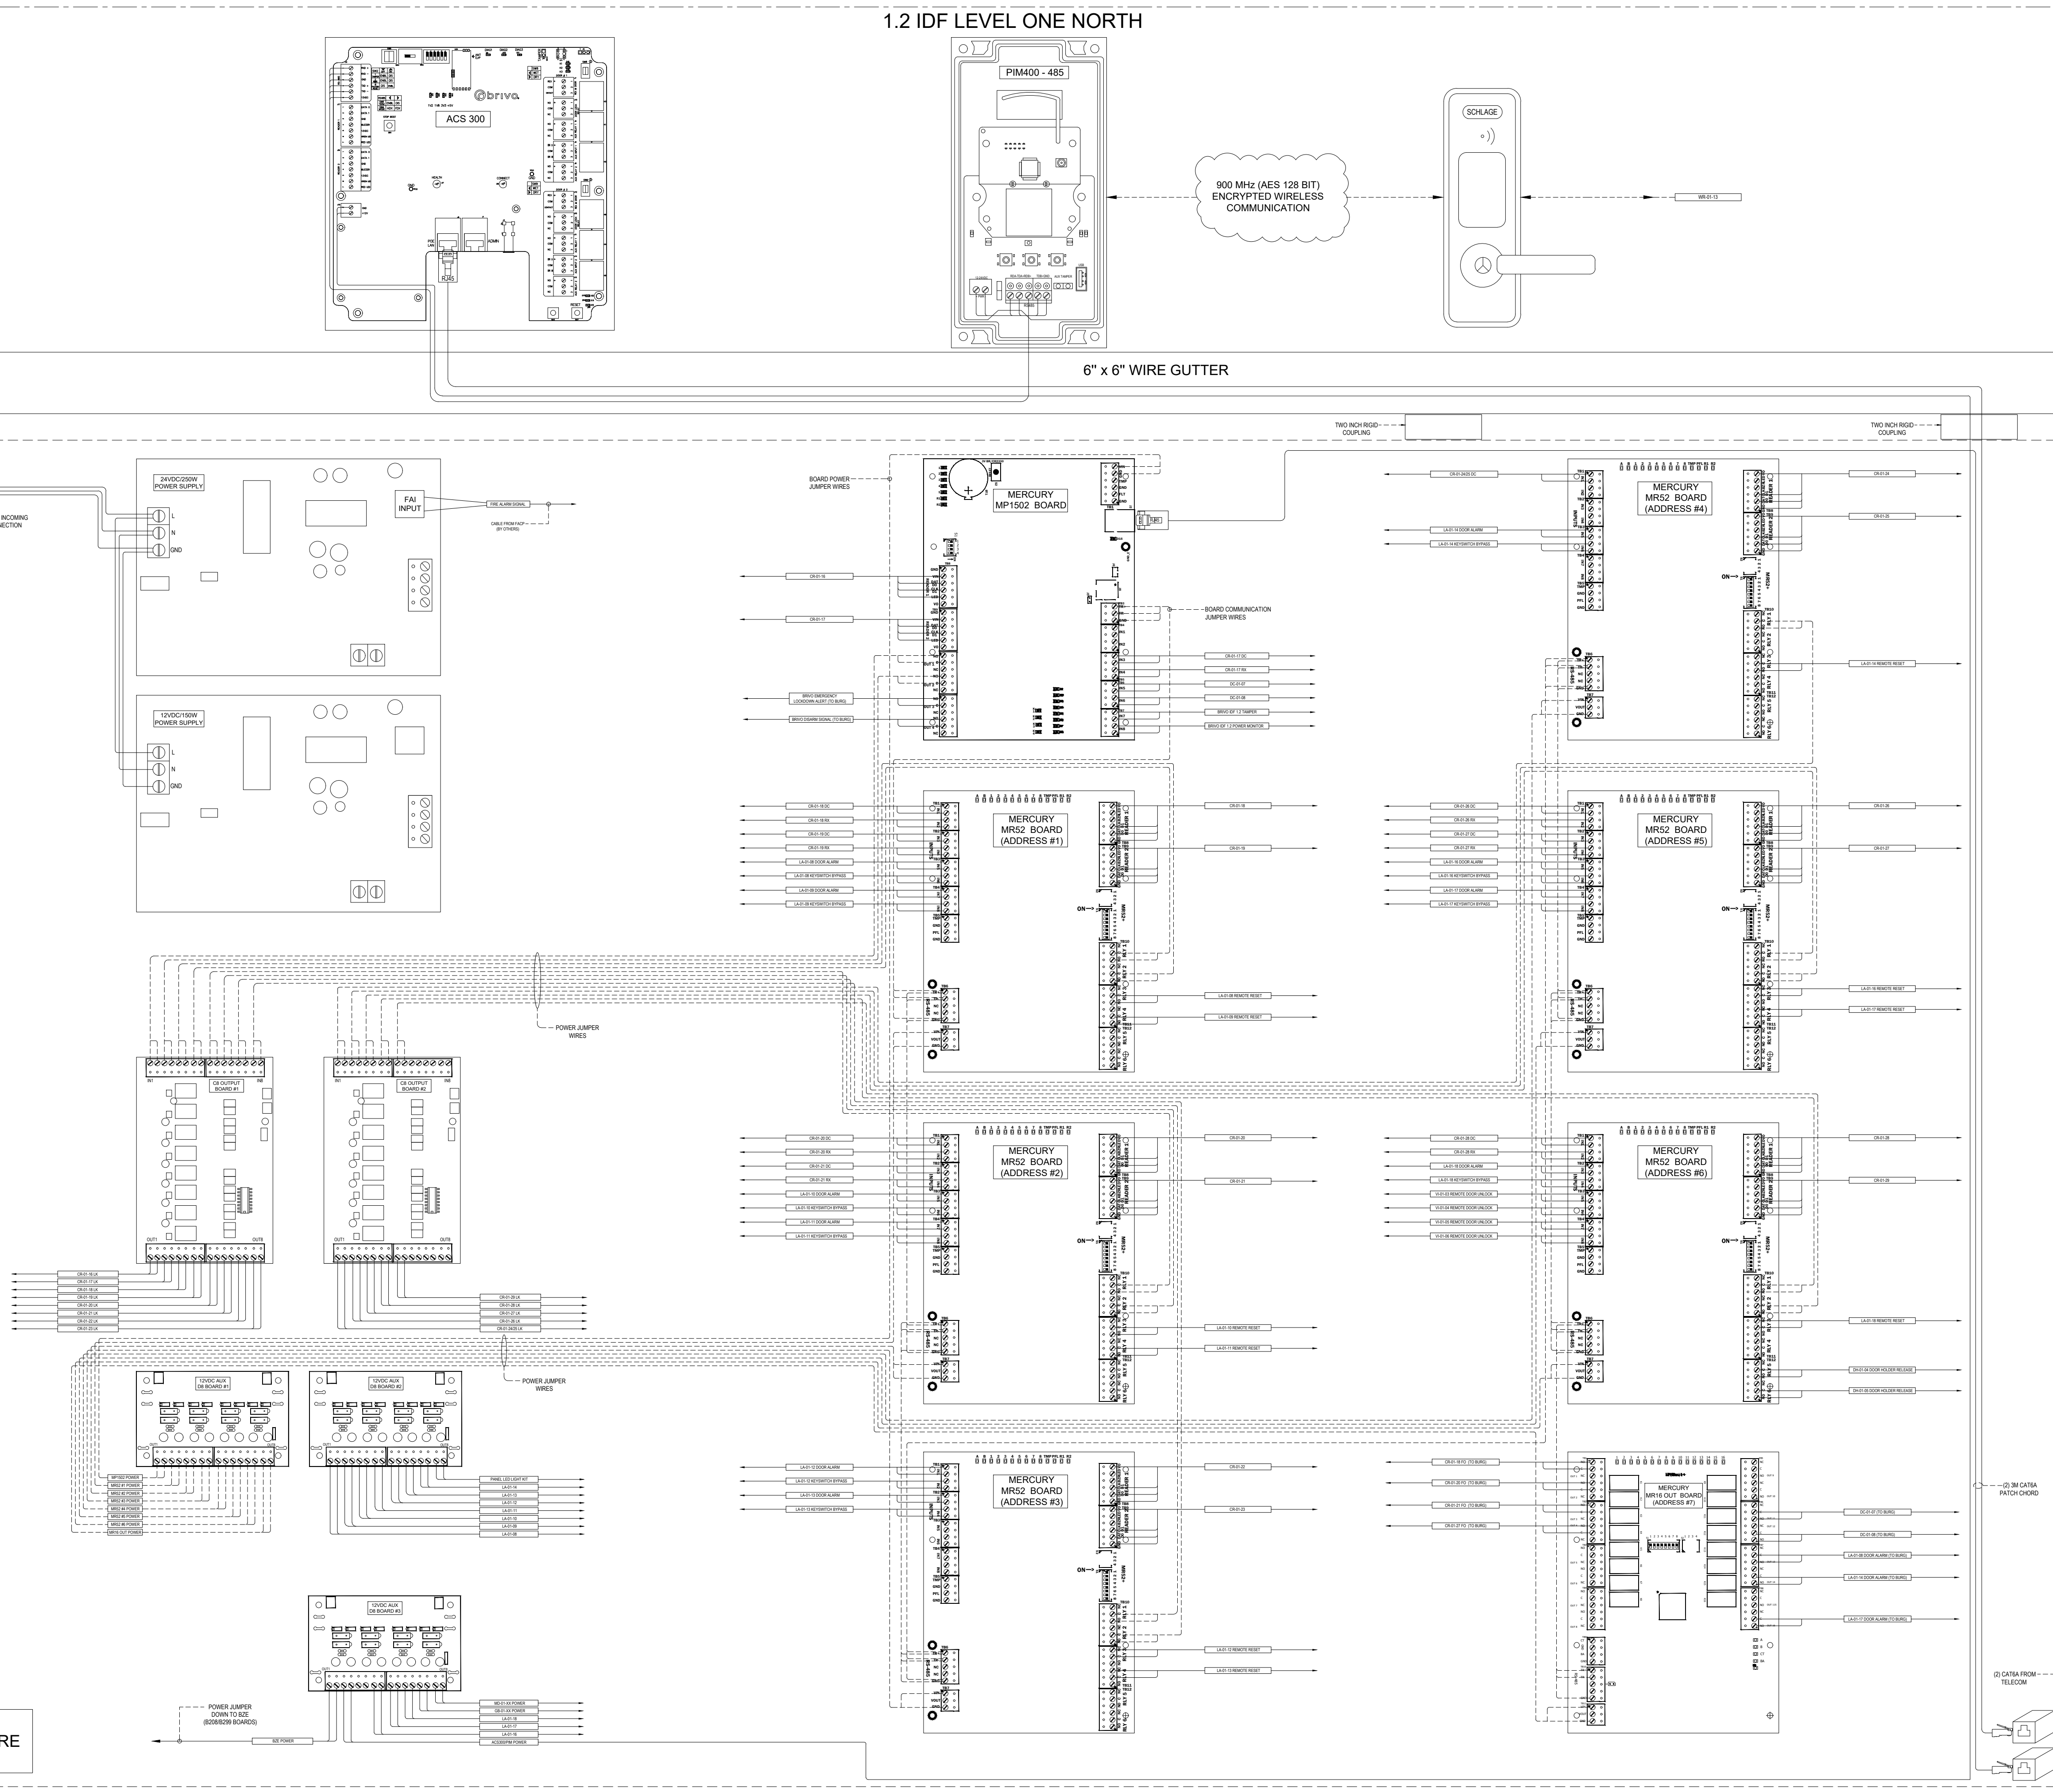

STAMP



DB STAMP

DATE: 05/03/2024
DESCRIPTION: DYNAMIC SECURITY PLANS

ST. IGNATIUS COLLEGE PREPARATORY

2001 37th Ave, San Francisco, CA 94116

ACCESS CONTROL SYSTEM POINT TO POINT DIAGRAM

T6.17D