




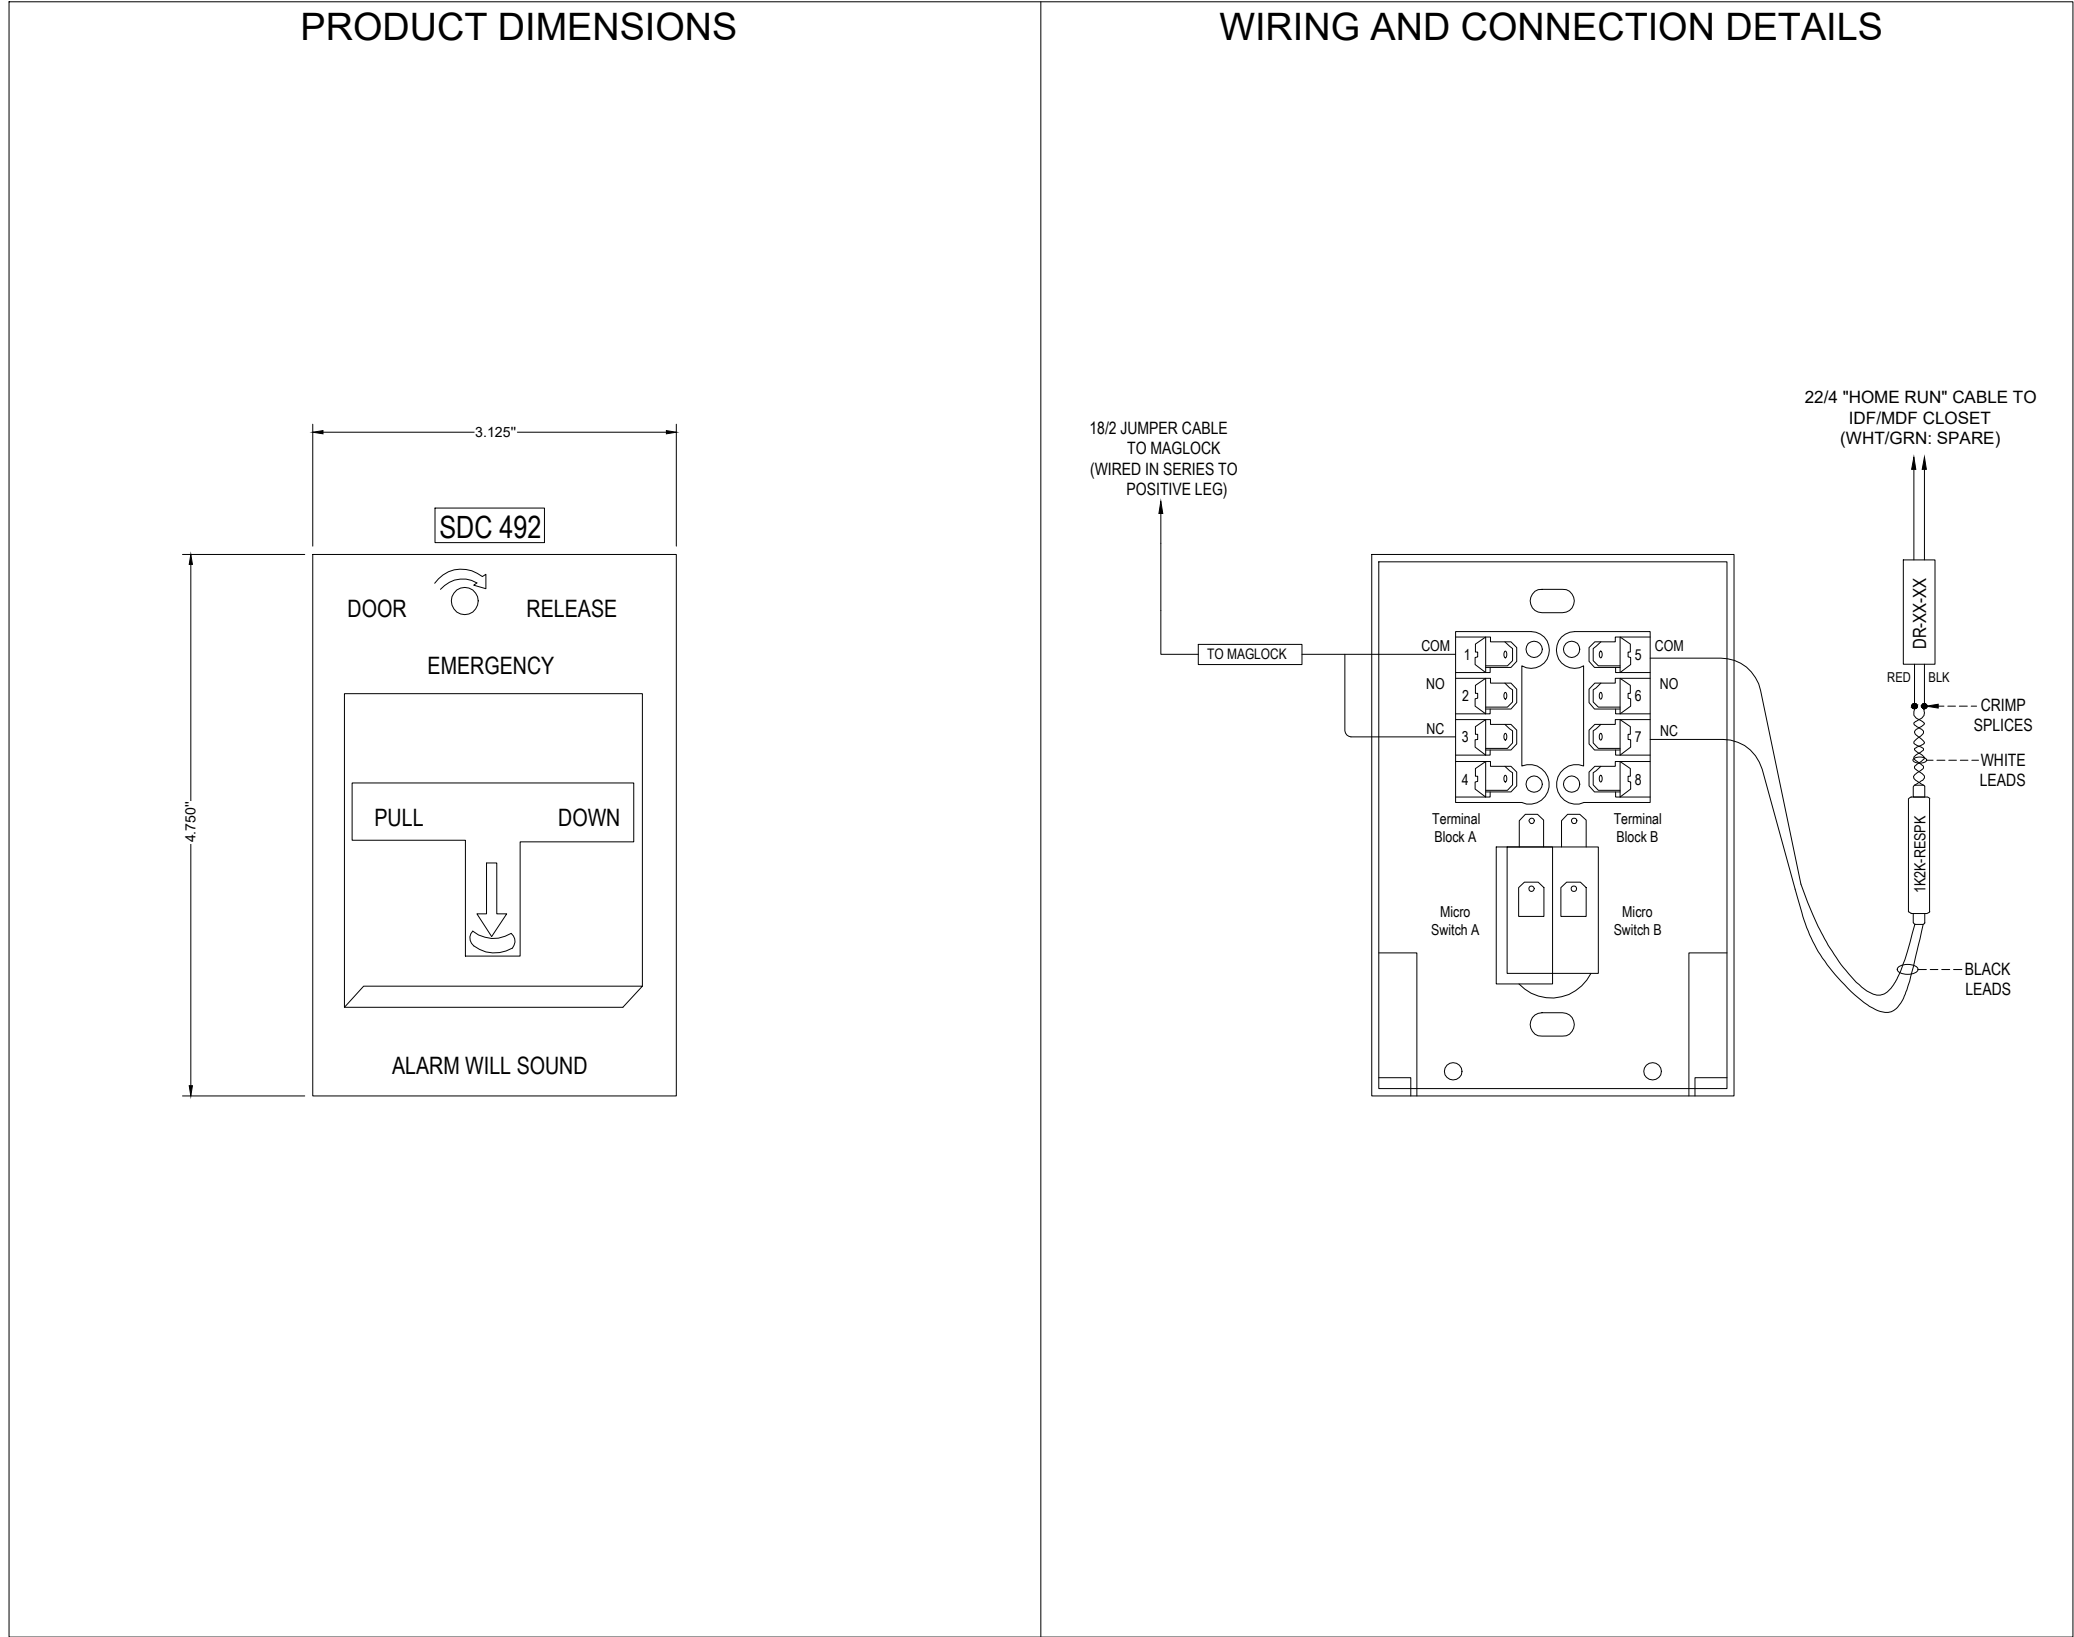


3 TYPICAL WALL-MOUNTED PULLSTATION DOOR RELEASE (DR-XX-XX)

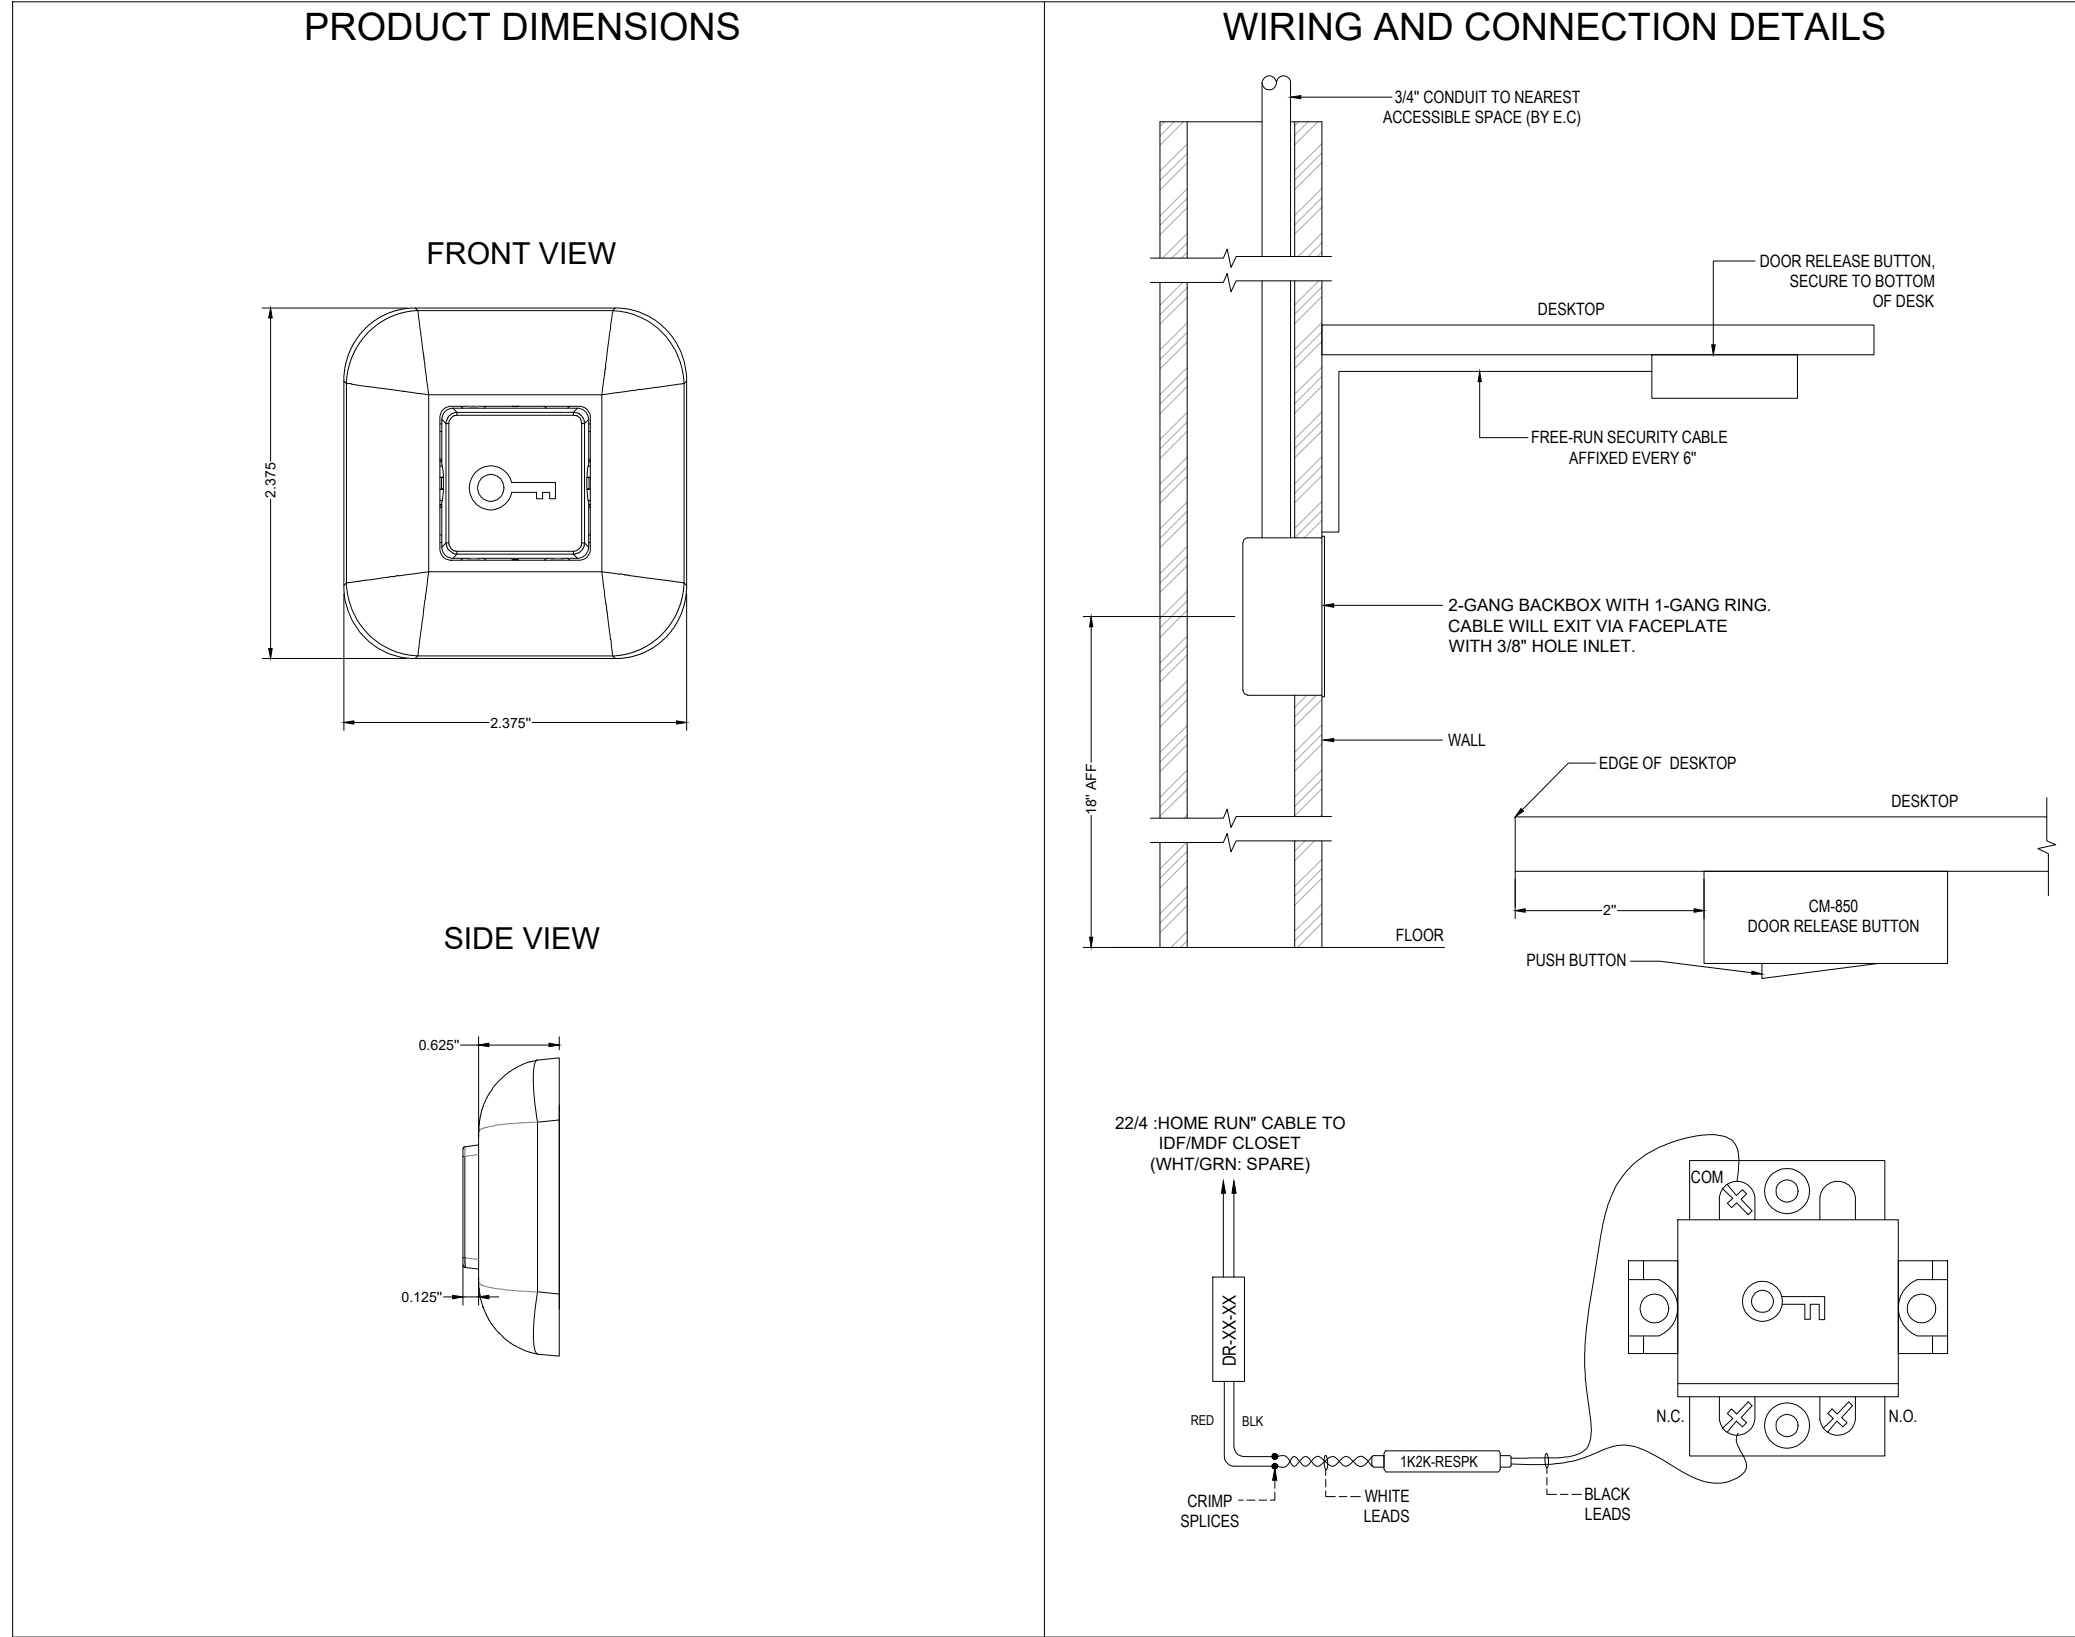

4 TYPICAL UNDER-DESK DOOR RELEASE (DR-XX-XX)

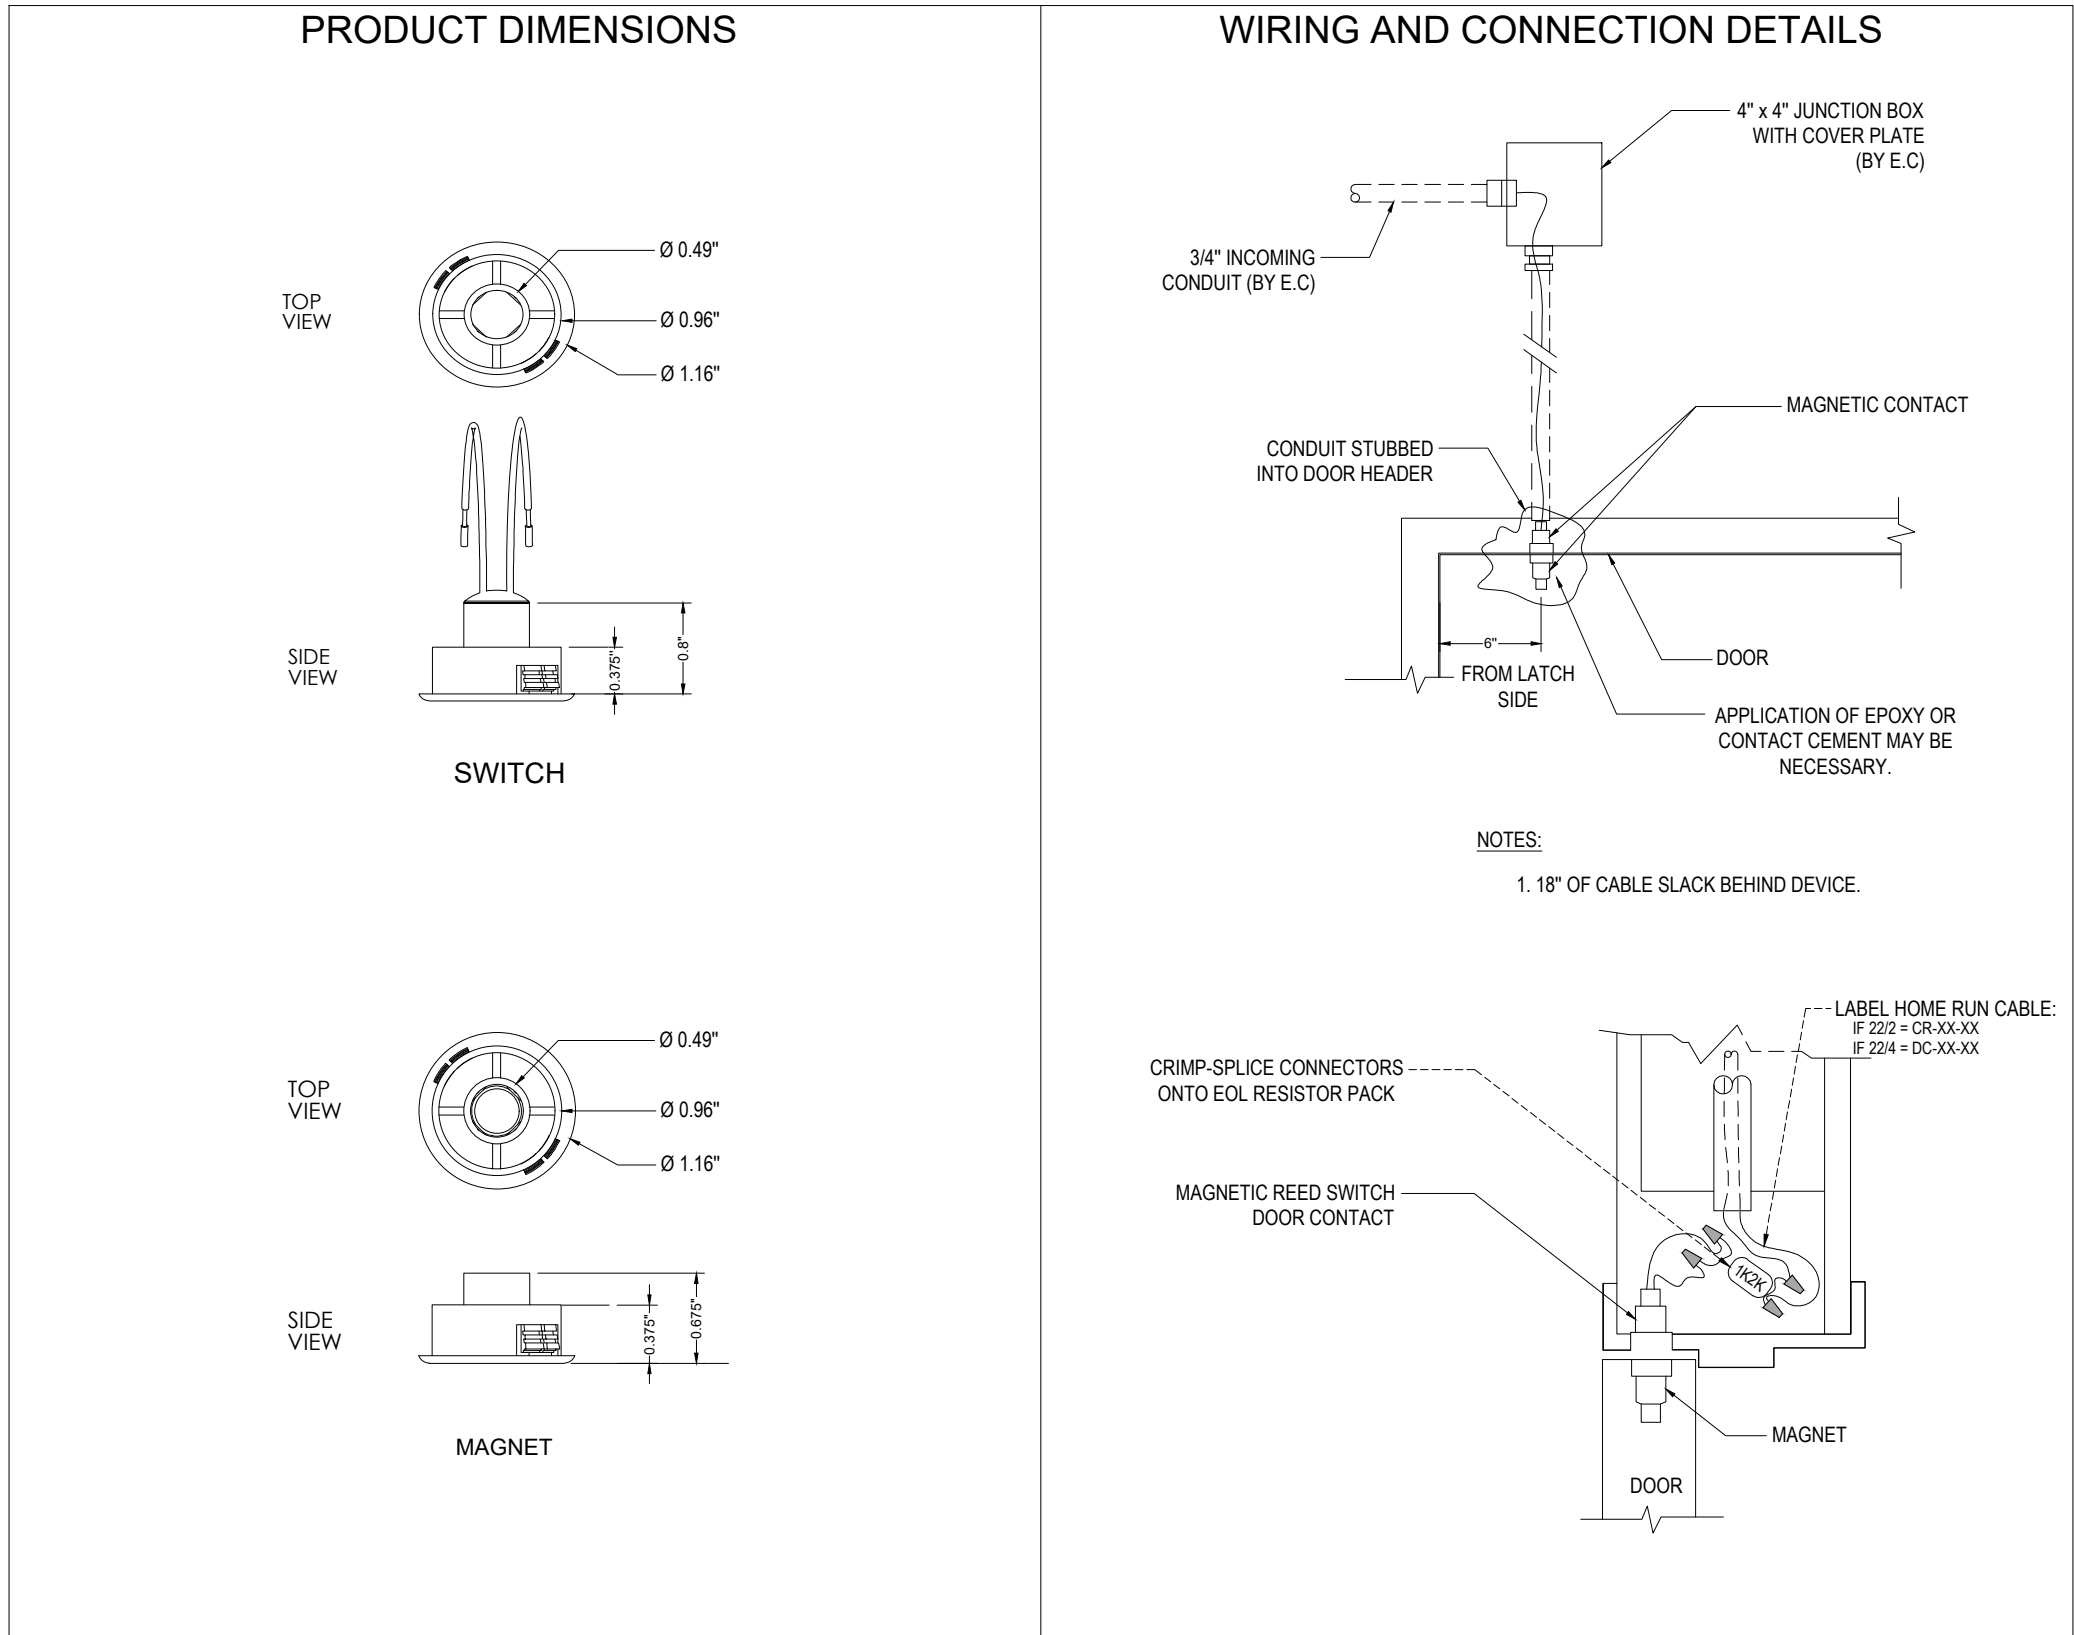

1 TYPICAL DOOR CONTACT(DC-XX-XX)

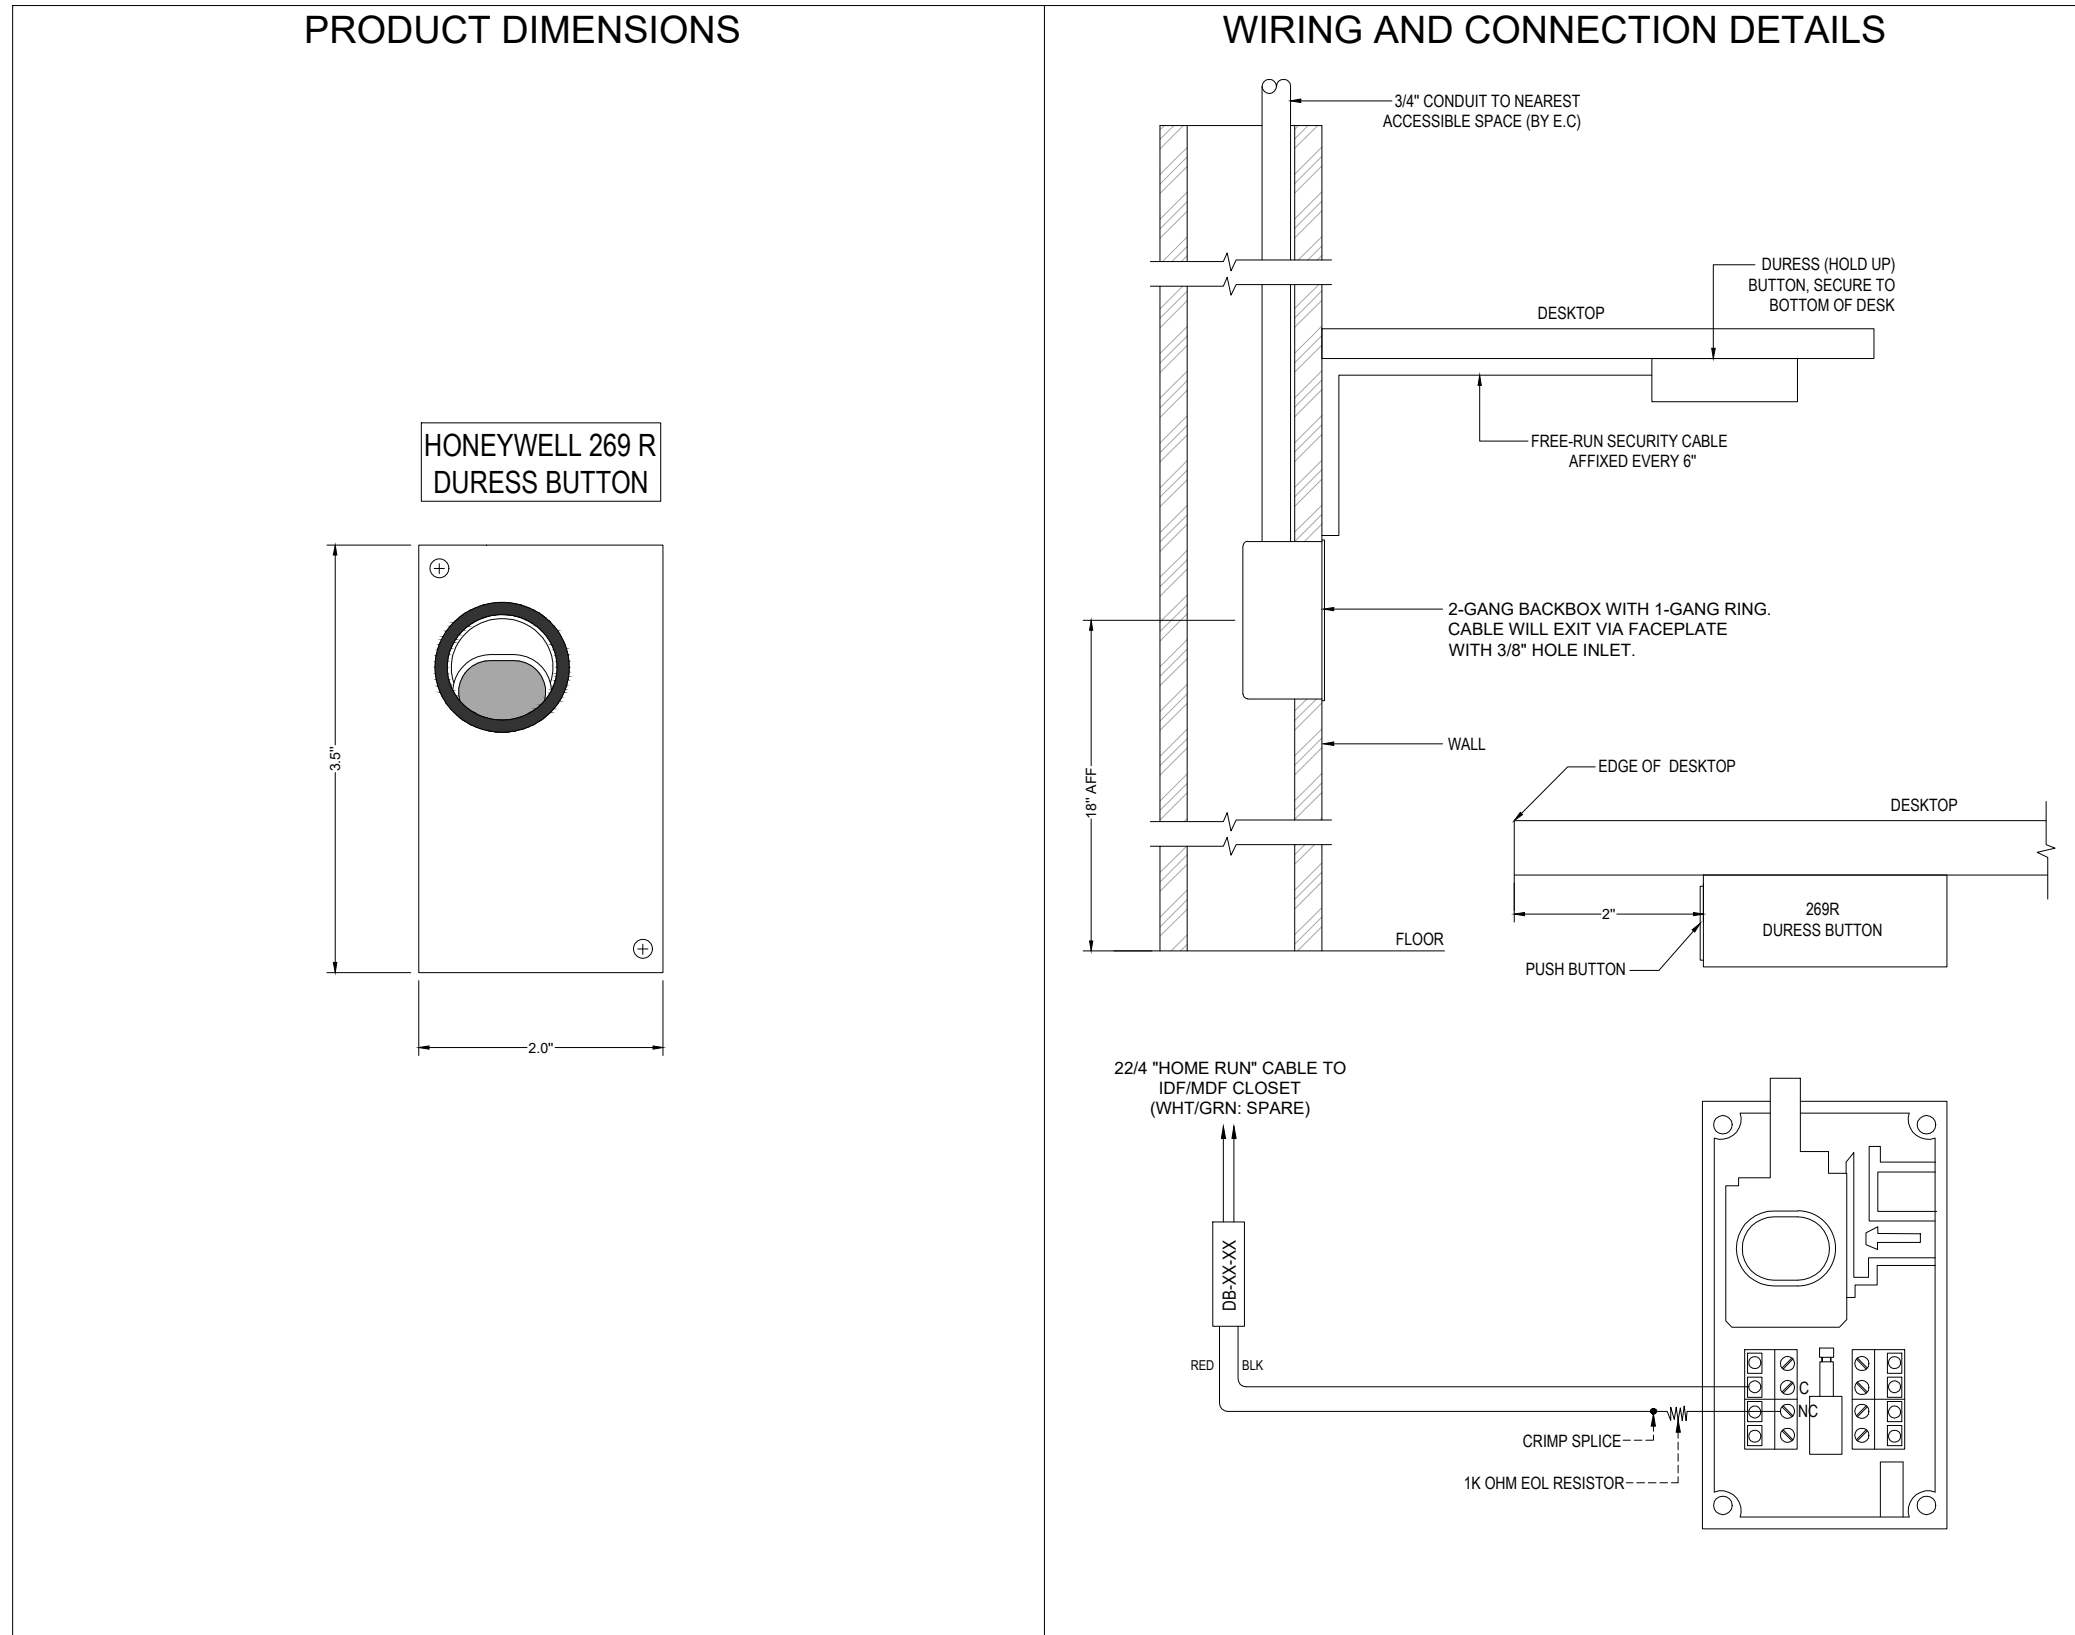

2 TYPICAL DURESS BUTTON (DB-XX-XX)



STAMP



DB STAMP

REV.	DATE	DESCRIPTION
1	08/03/2008	DYNAMIC SECURITY PLANS

ST. IGNATIUS COLLEGE PREPARATORY

2001, 37th Ave. San Francisco, CA 94116

DETAILS - SECURITY DEVICES

T6.19B