




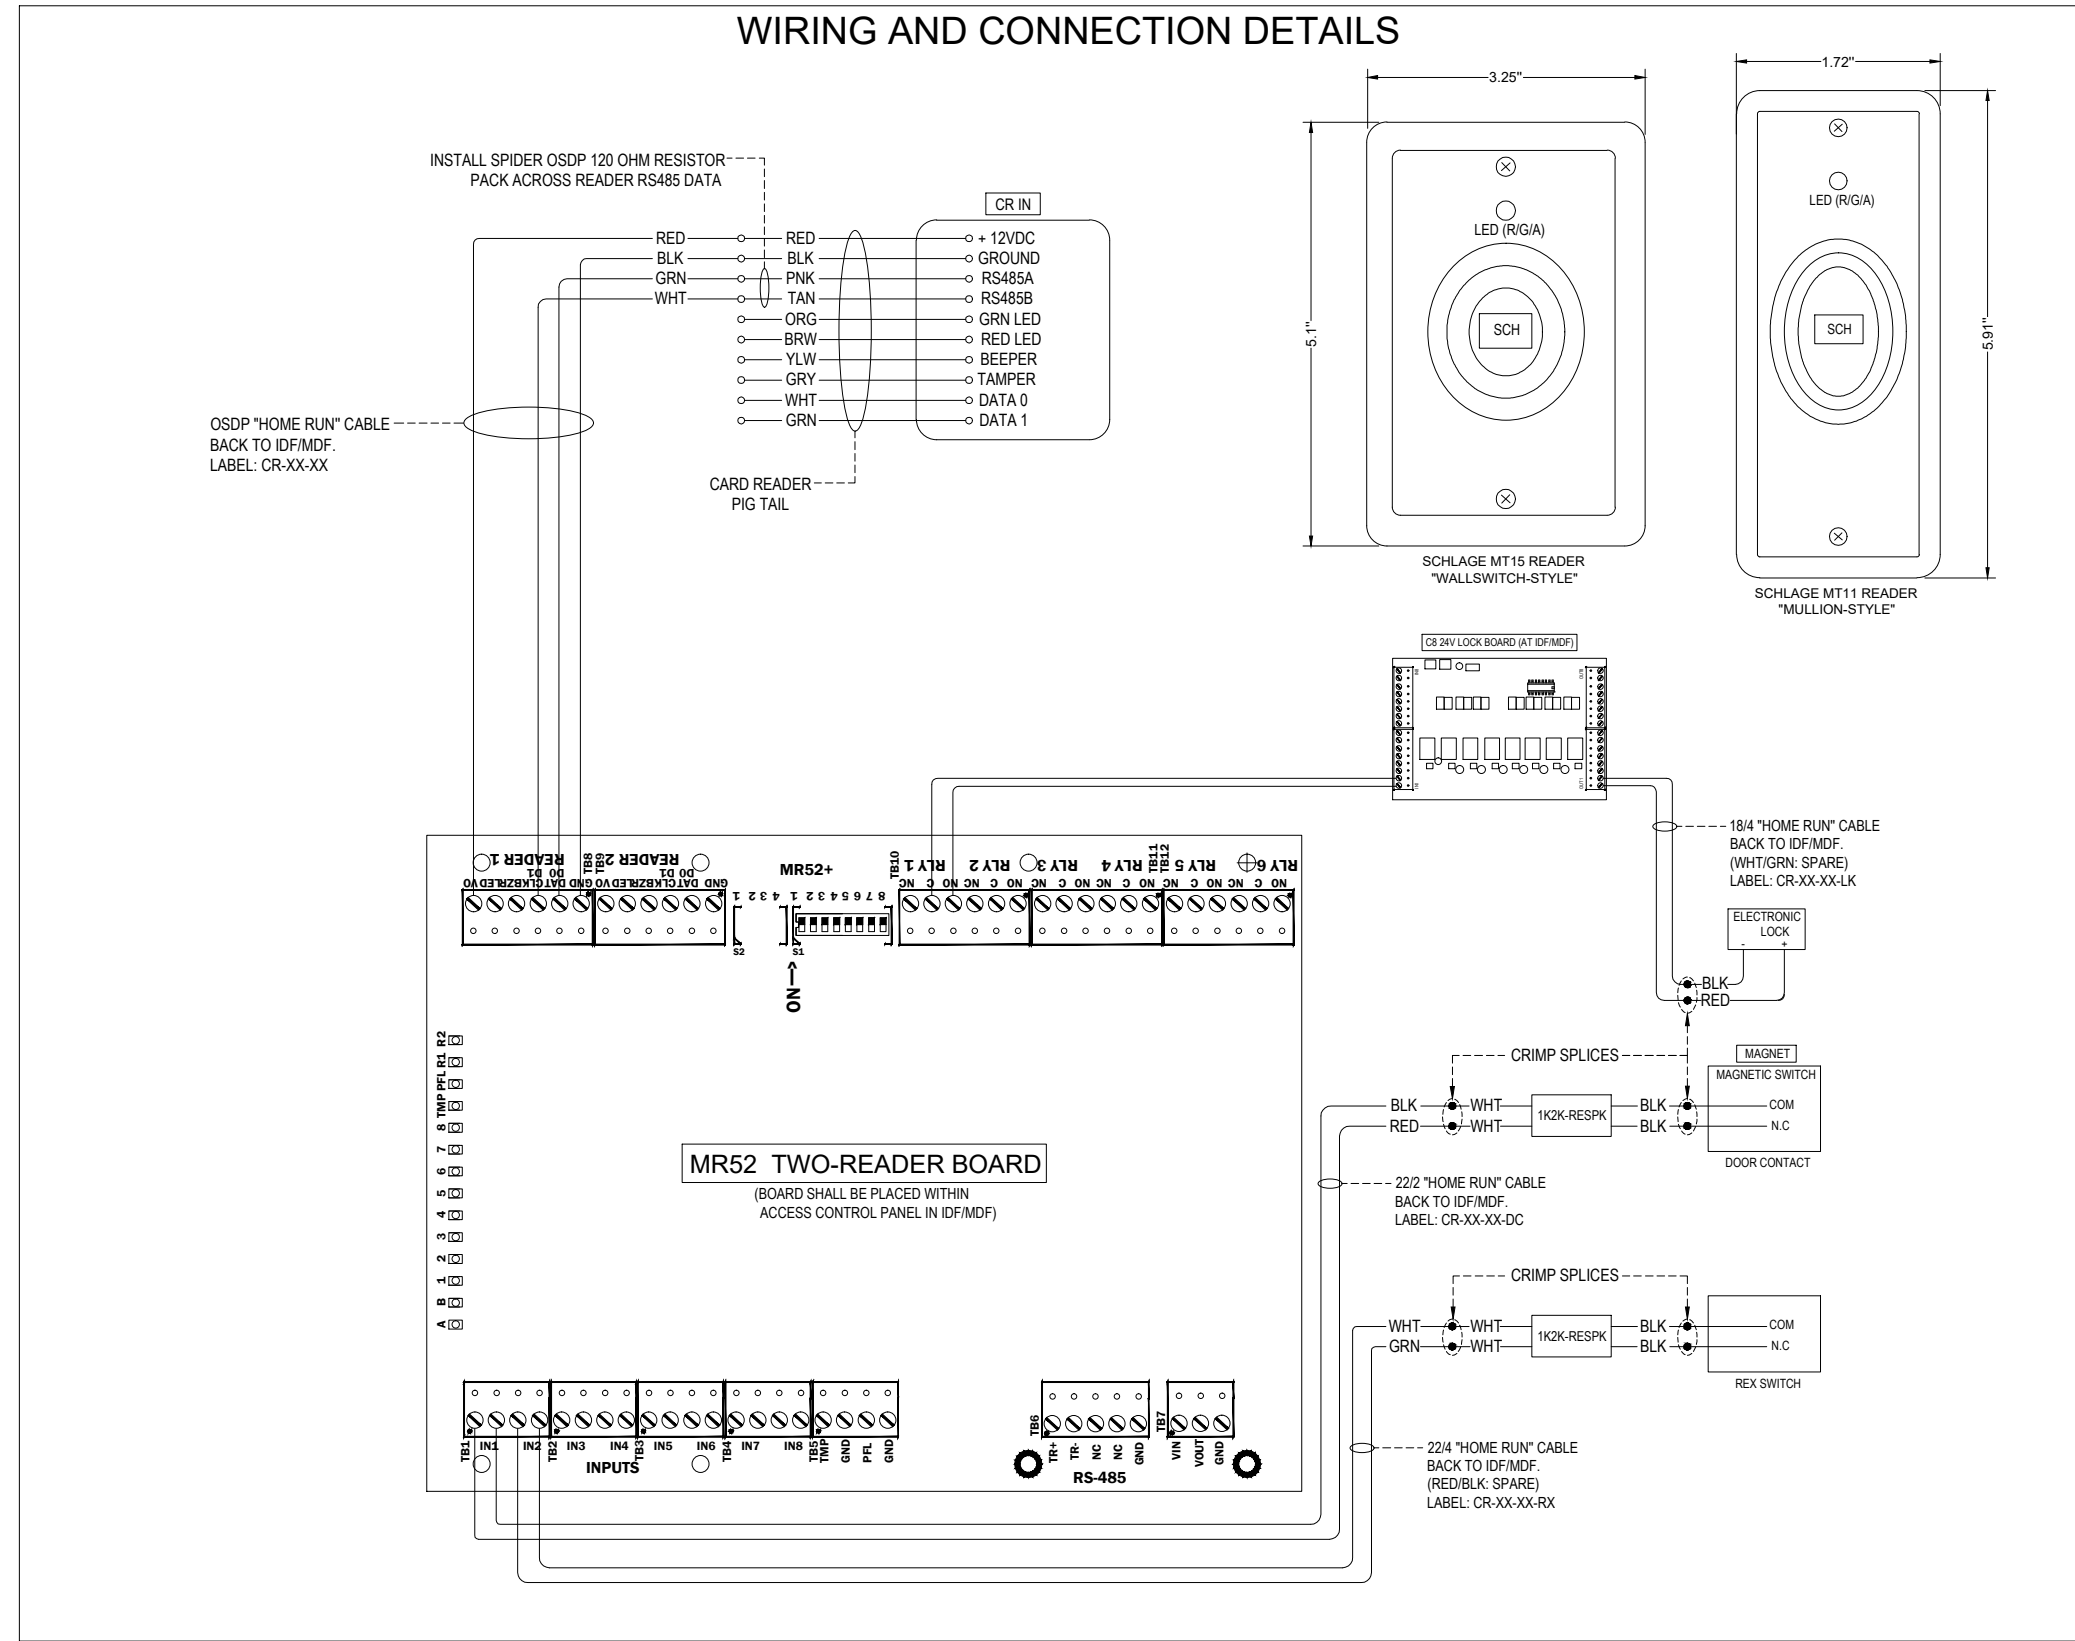


3 TYPICAL CARD READ IN / REX OUT (CR-XX-XX)

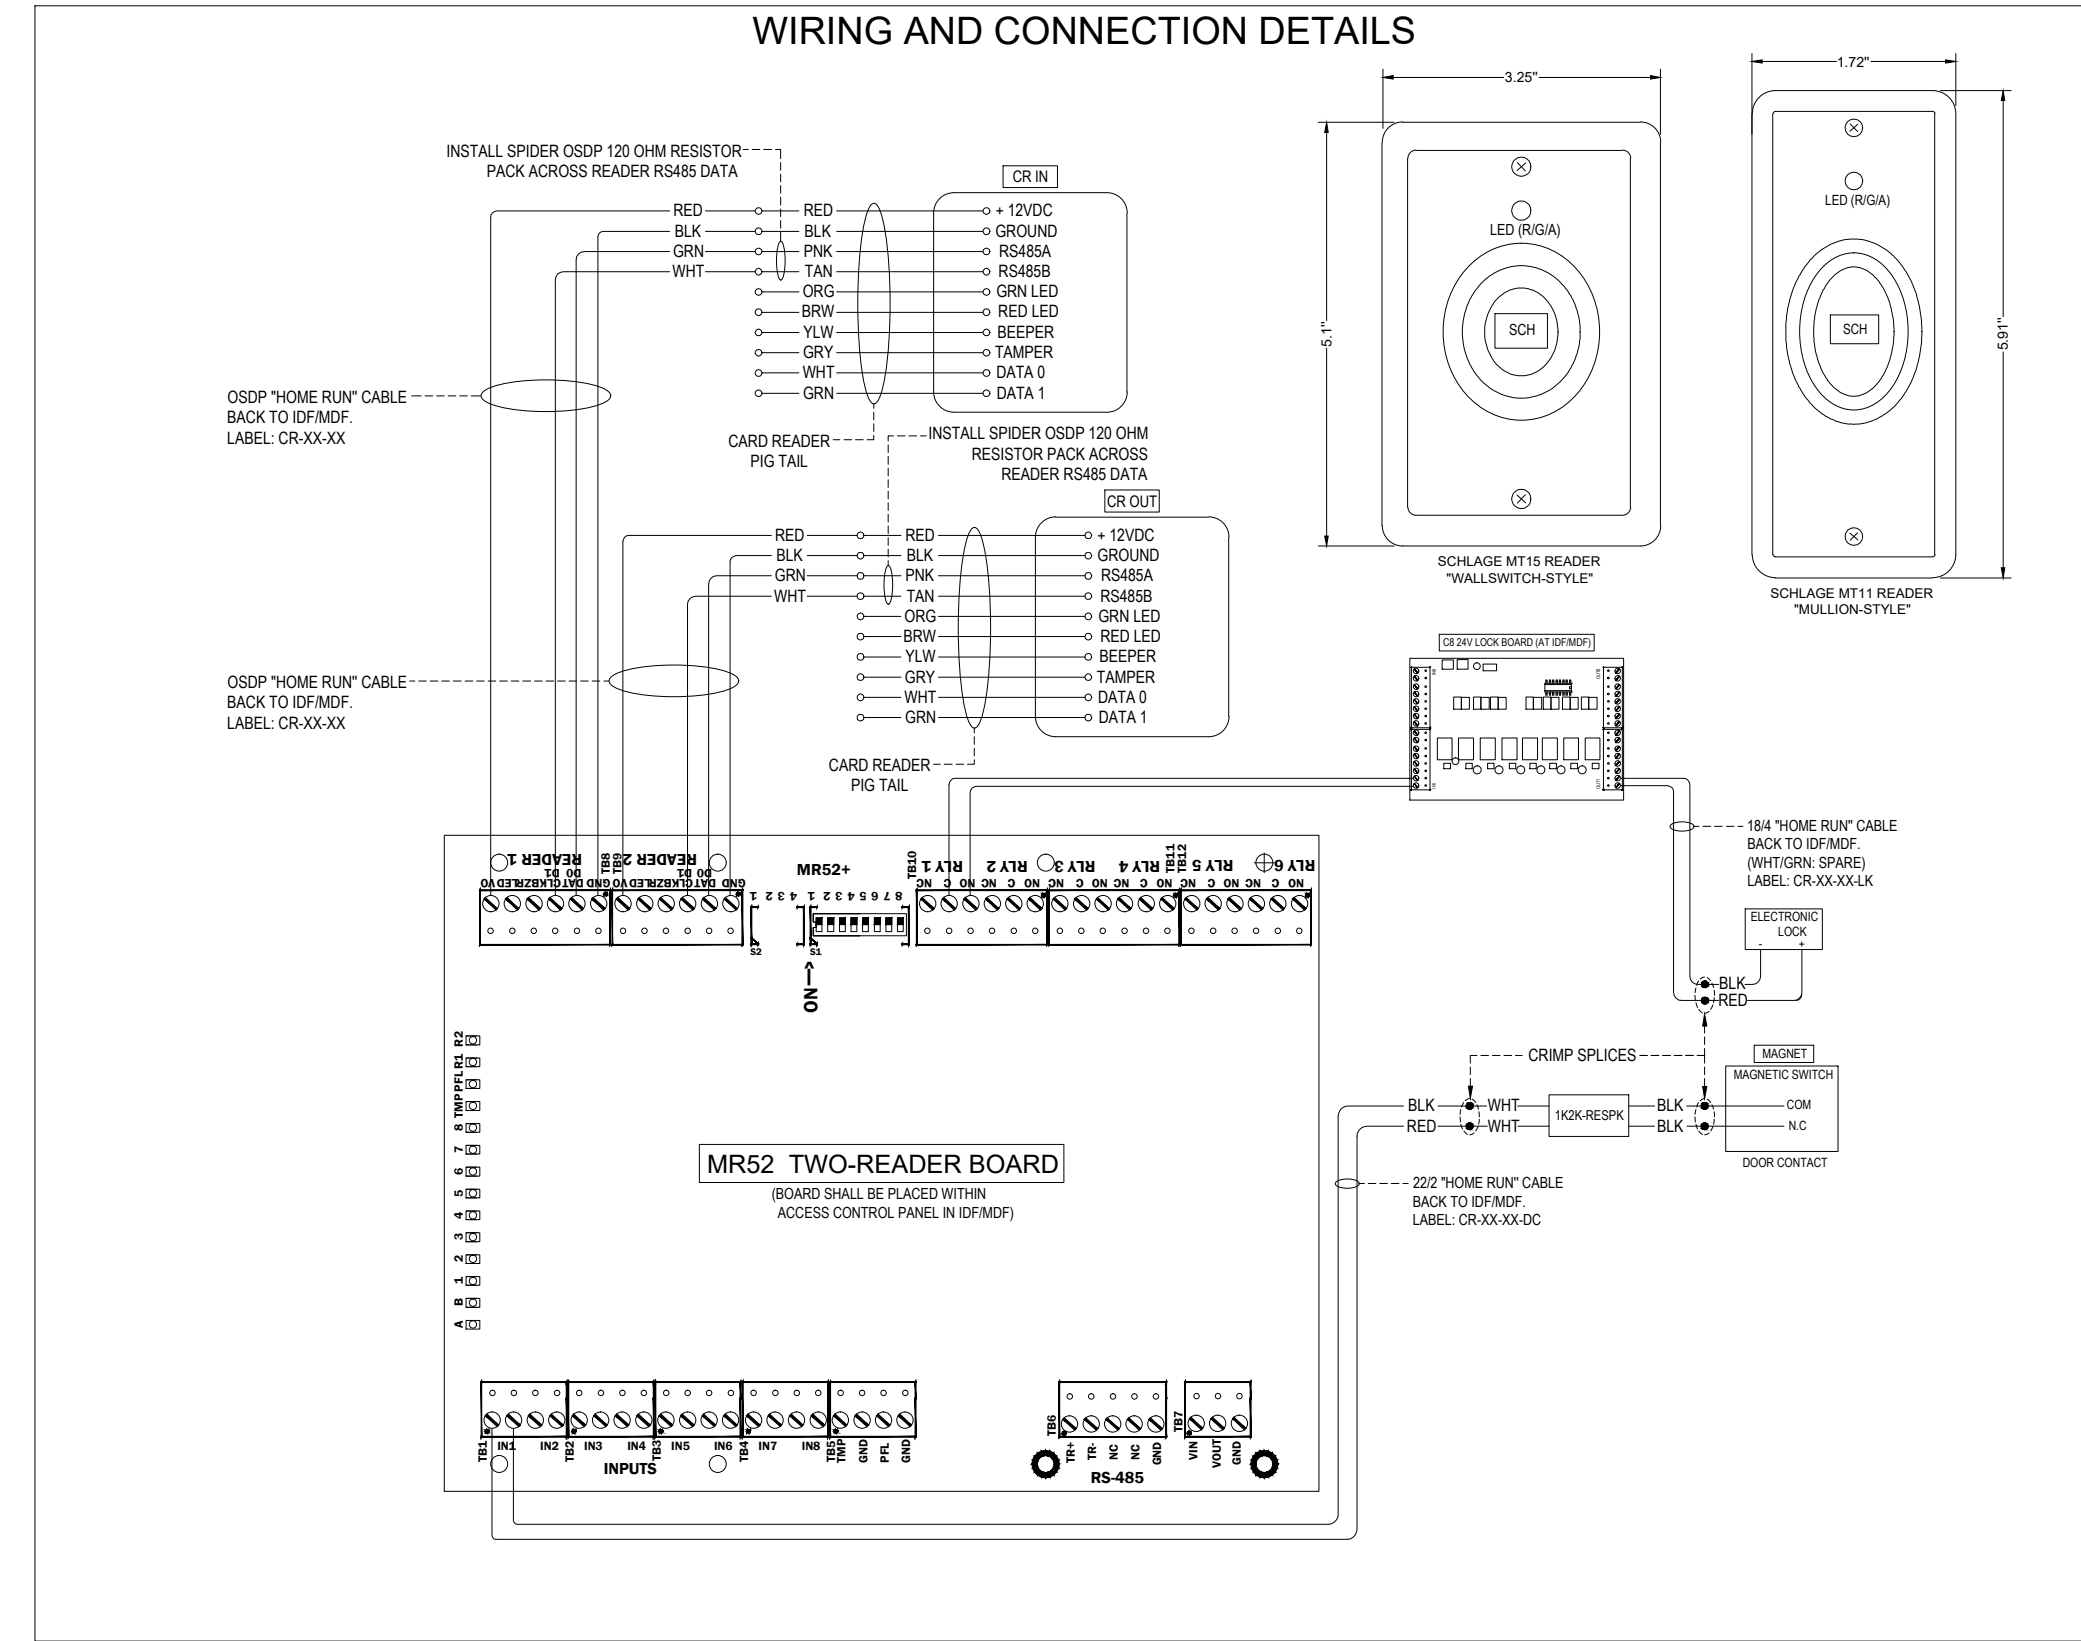


4 TYPICAL CARD READER IN / CARD READER OUT (CR-XX-XX)

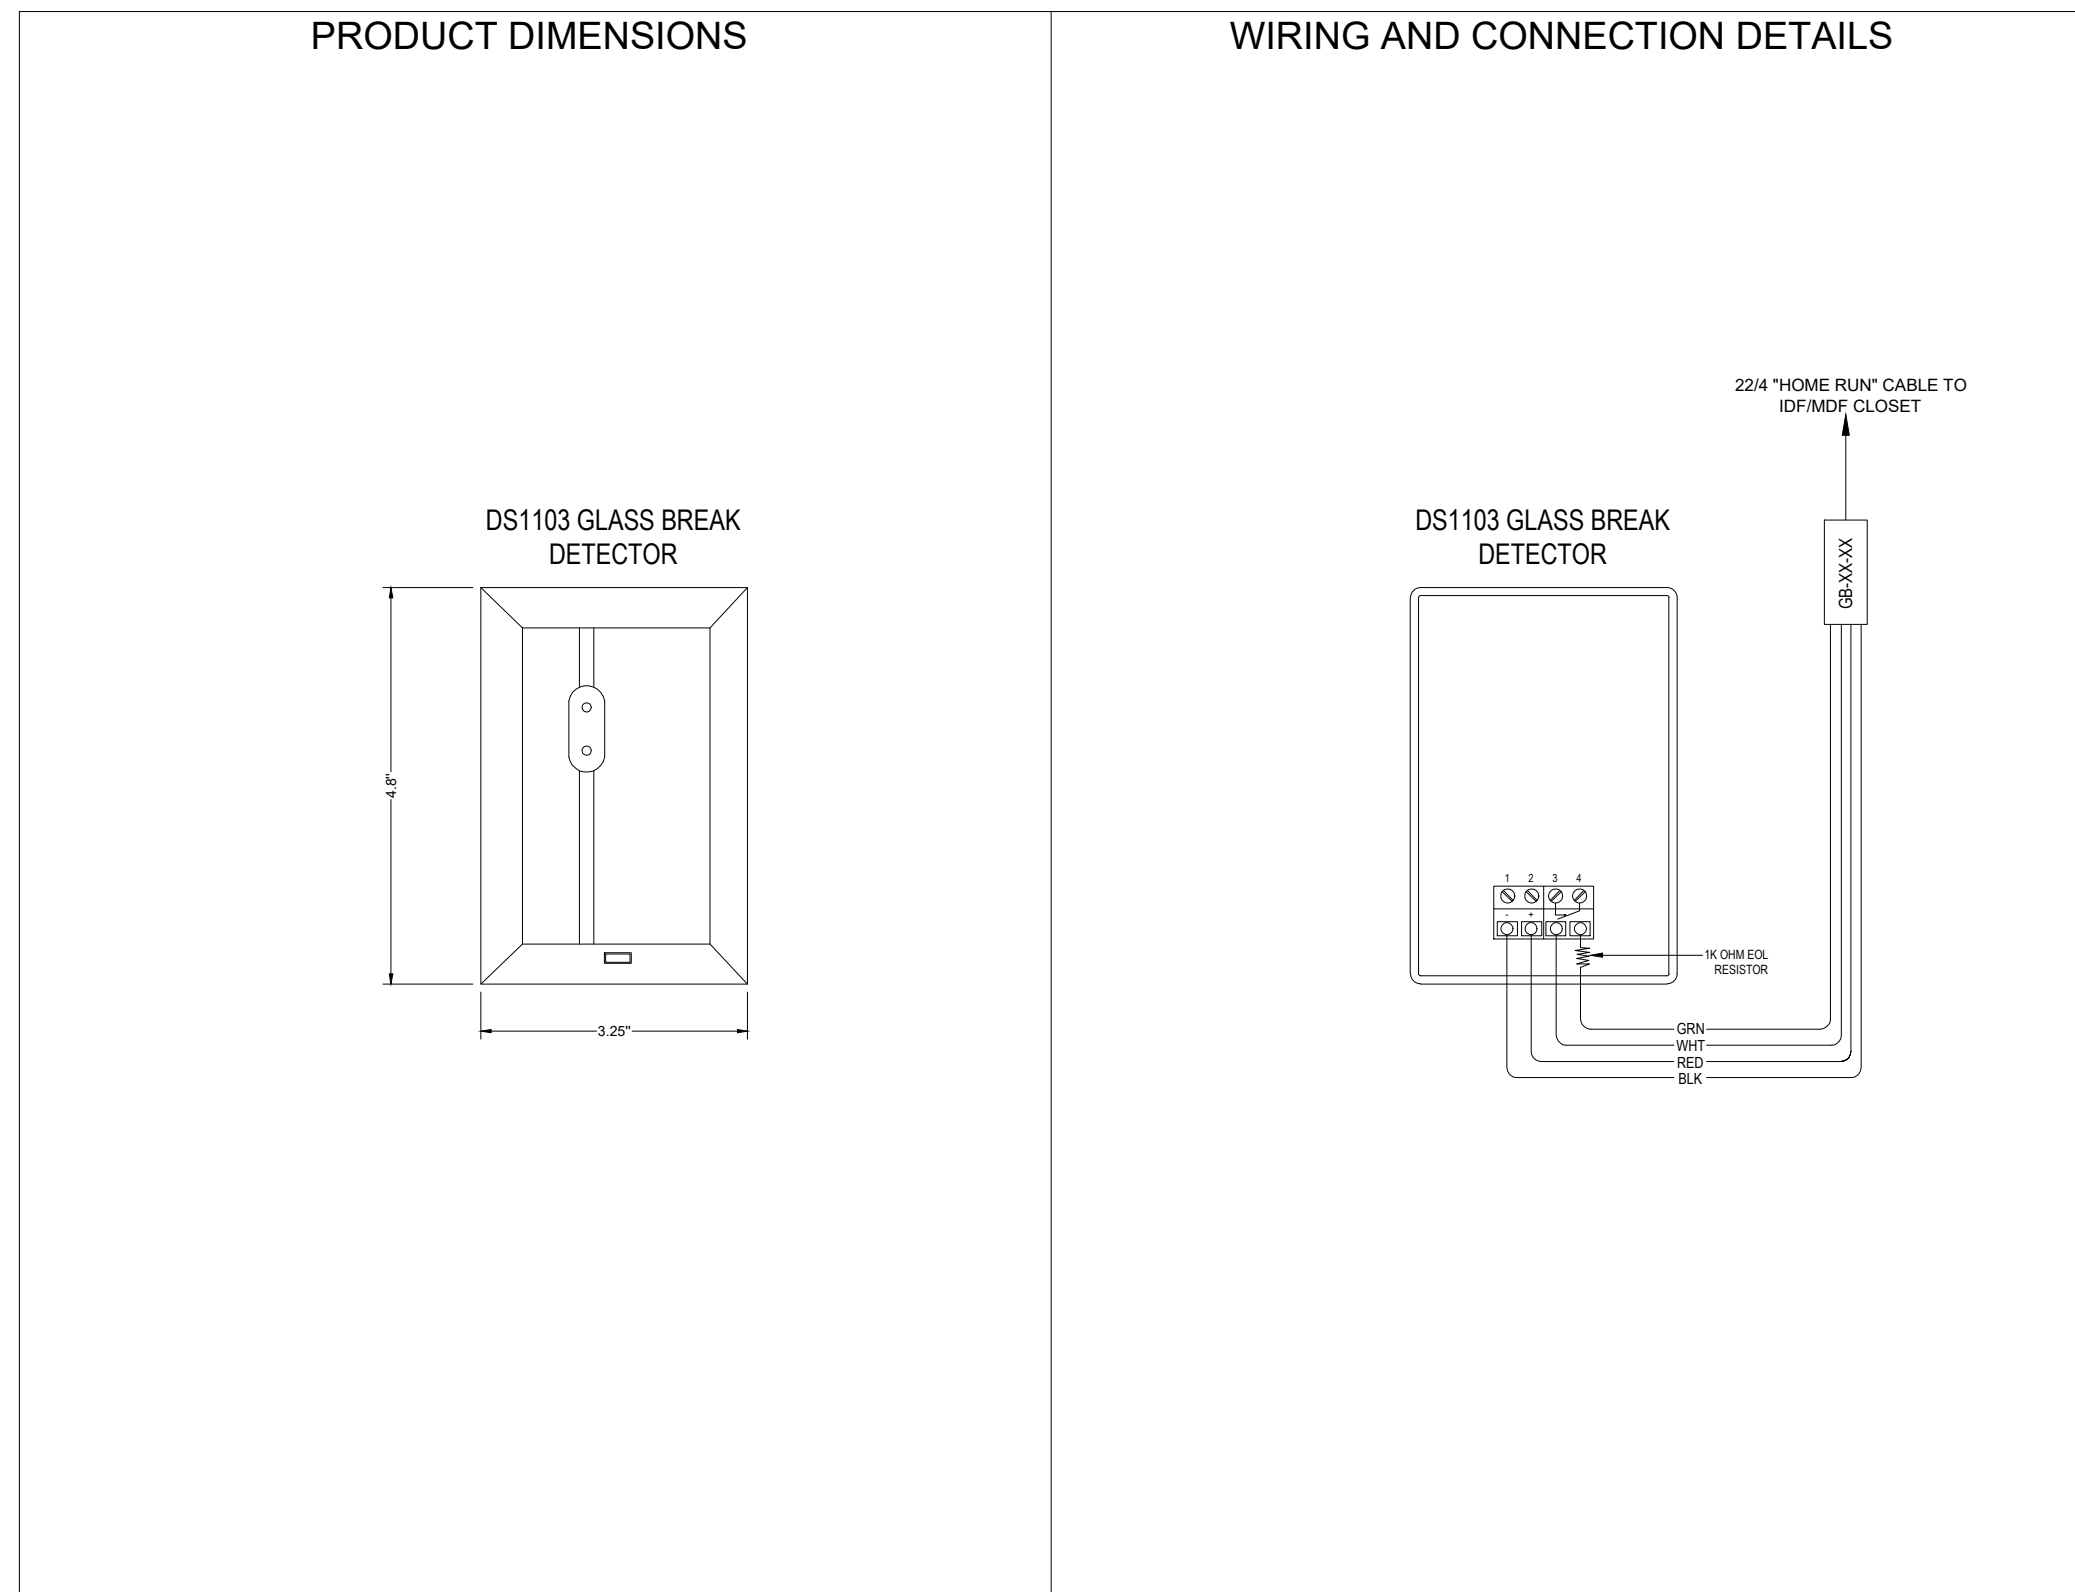

1 TYPICAL GLASS BREAK DETECTOR (GB-XX-XX)
*EACH GB DIRECTLY WIRED BACK TO THE PANEL

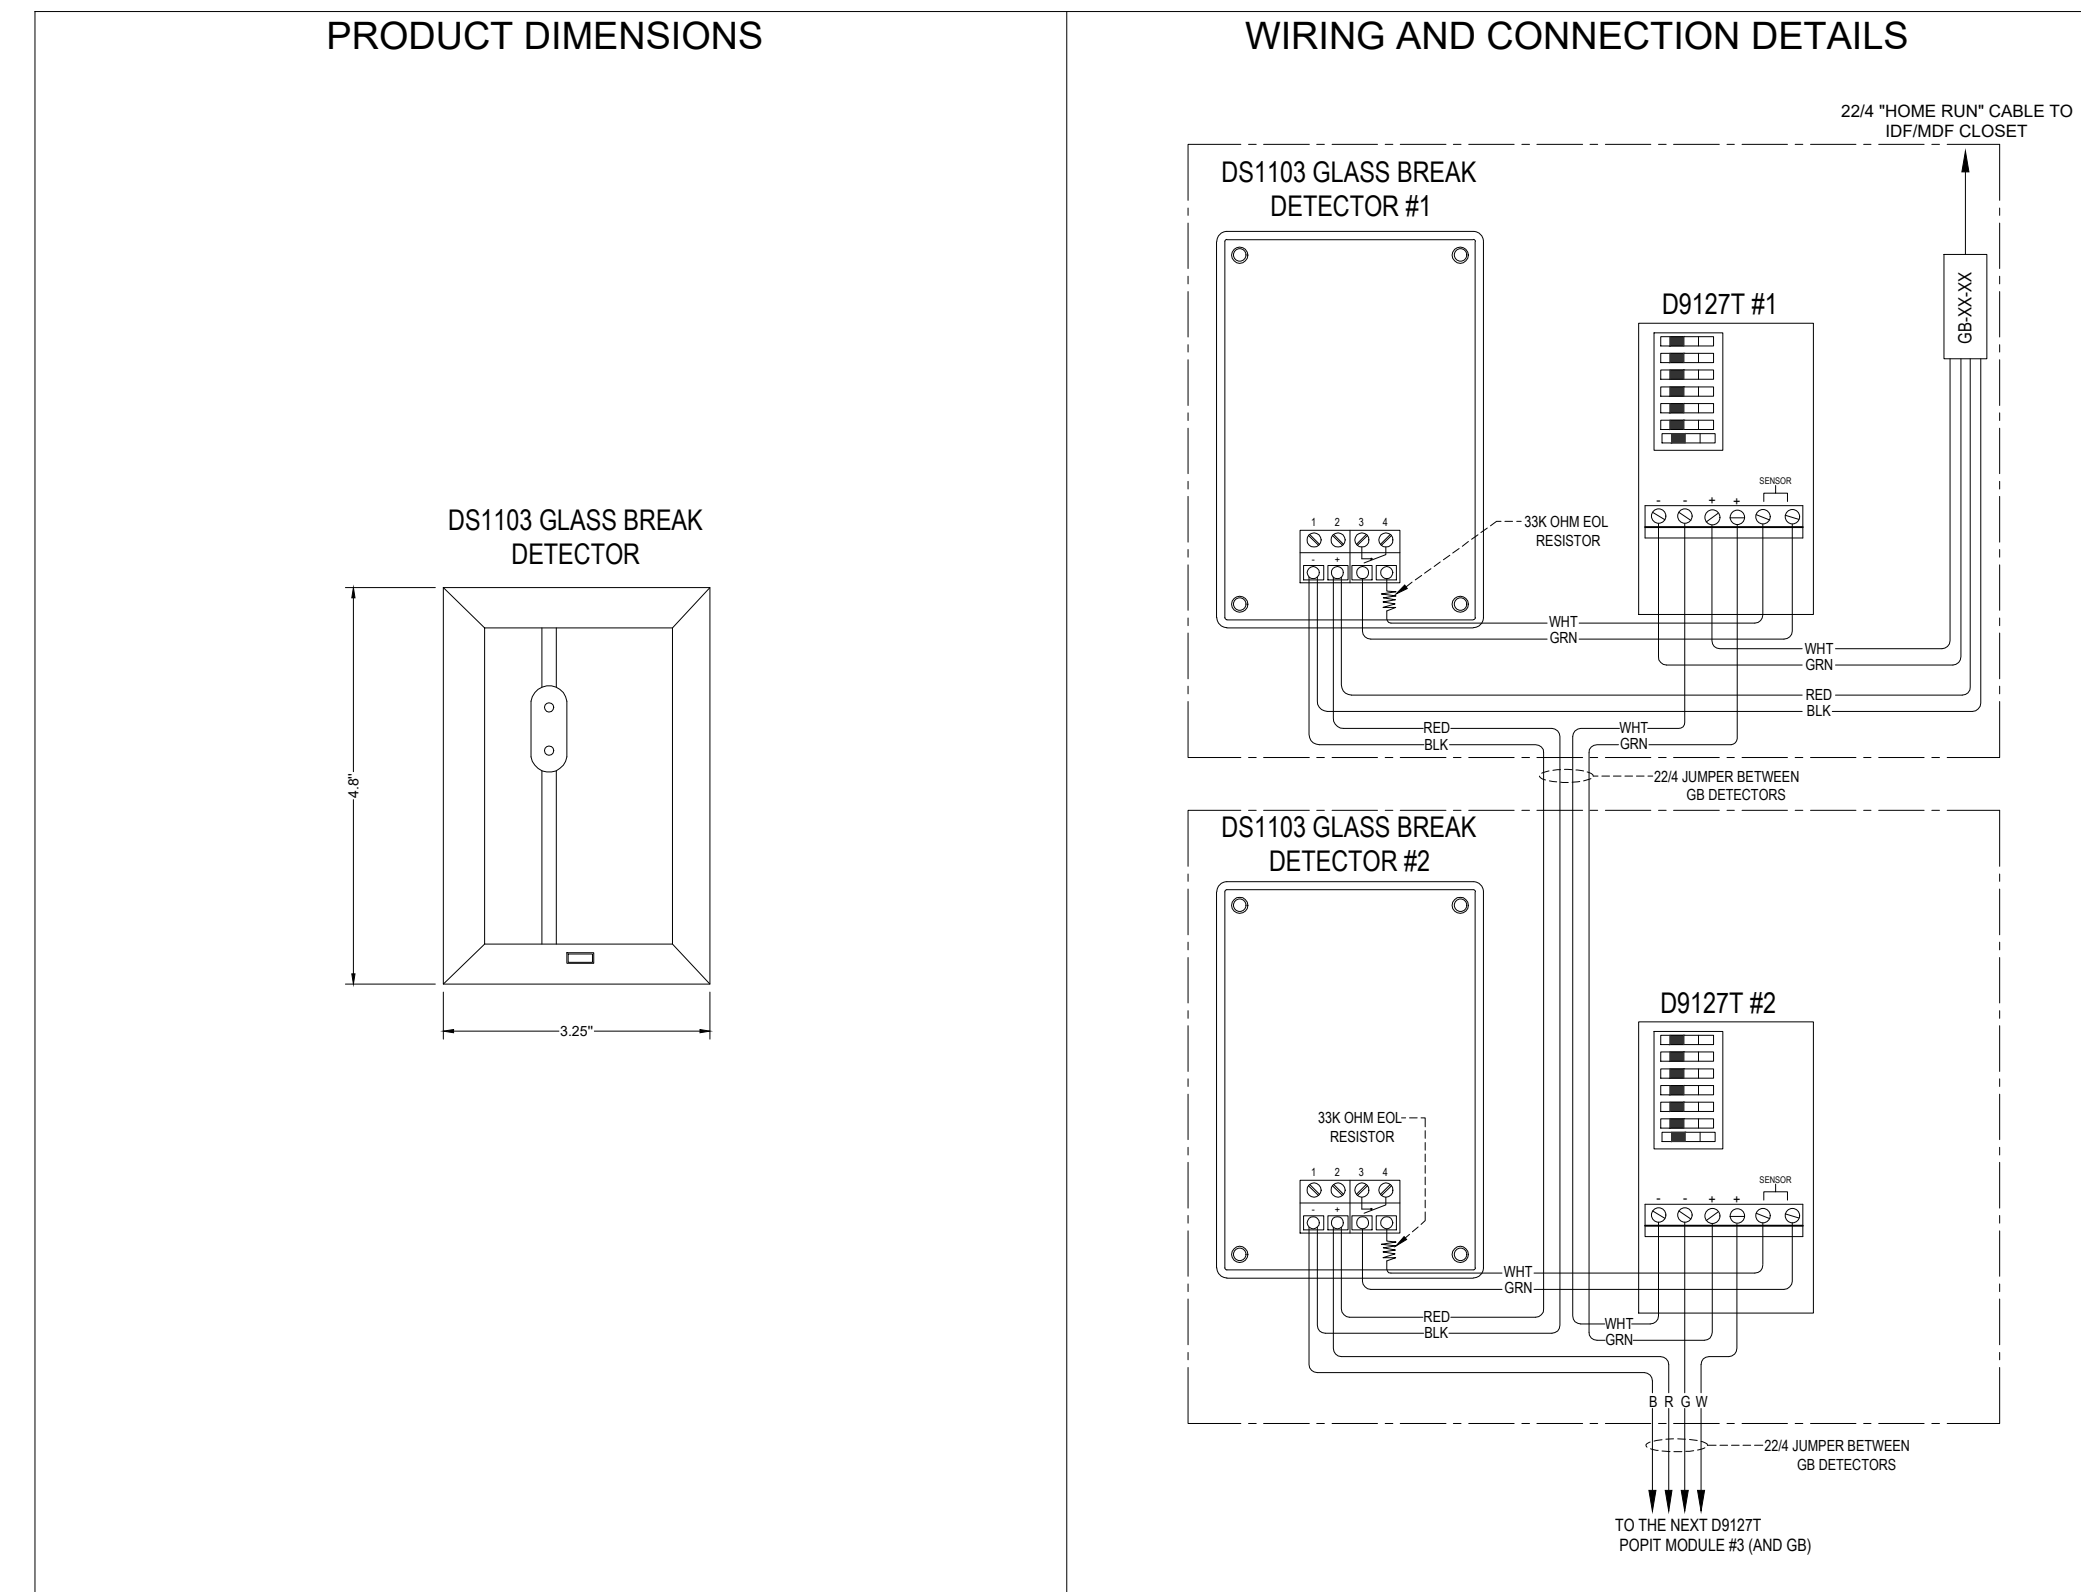

2 TYPICAL GLASS BREAK DETECTOR (GB-XX-XX)
*GB'S FIELD DAISY-CHAINED USING D9127T POPIT MODULES

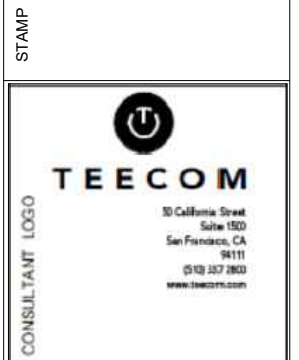

REV	DATE	DESCRIPTION
000000		DYNAMIC SECURITY PLANS

ST. IGNATIUS COLLEGE PREPARATORY
2001, 37th Ave. San Francisco, CA 94116

DETAILS - SECURITY DEVICES

T6.19C