


7/1/2026 4:26:41 PM

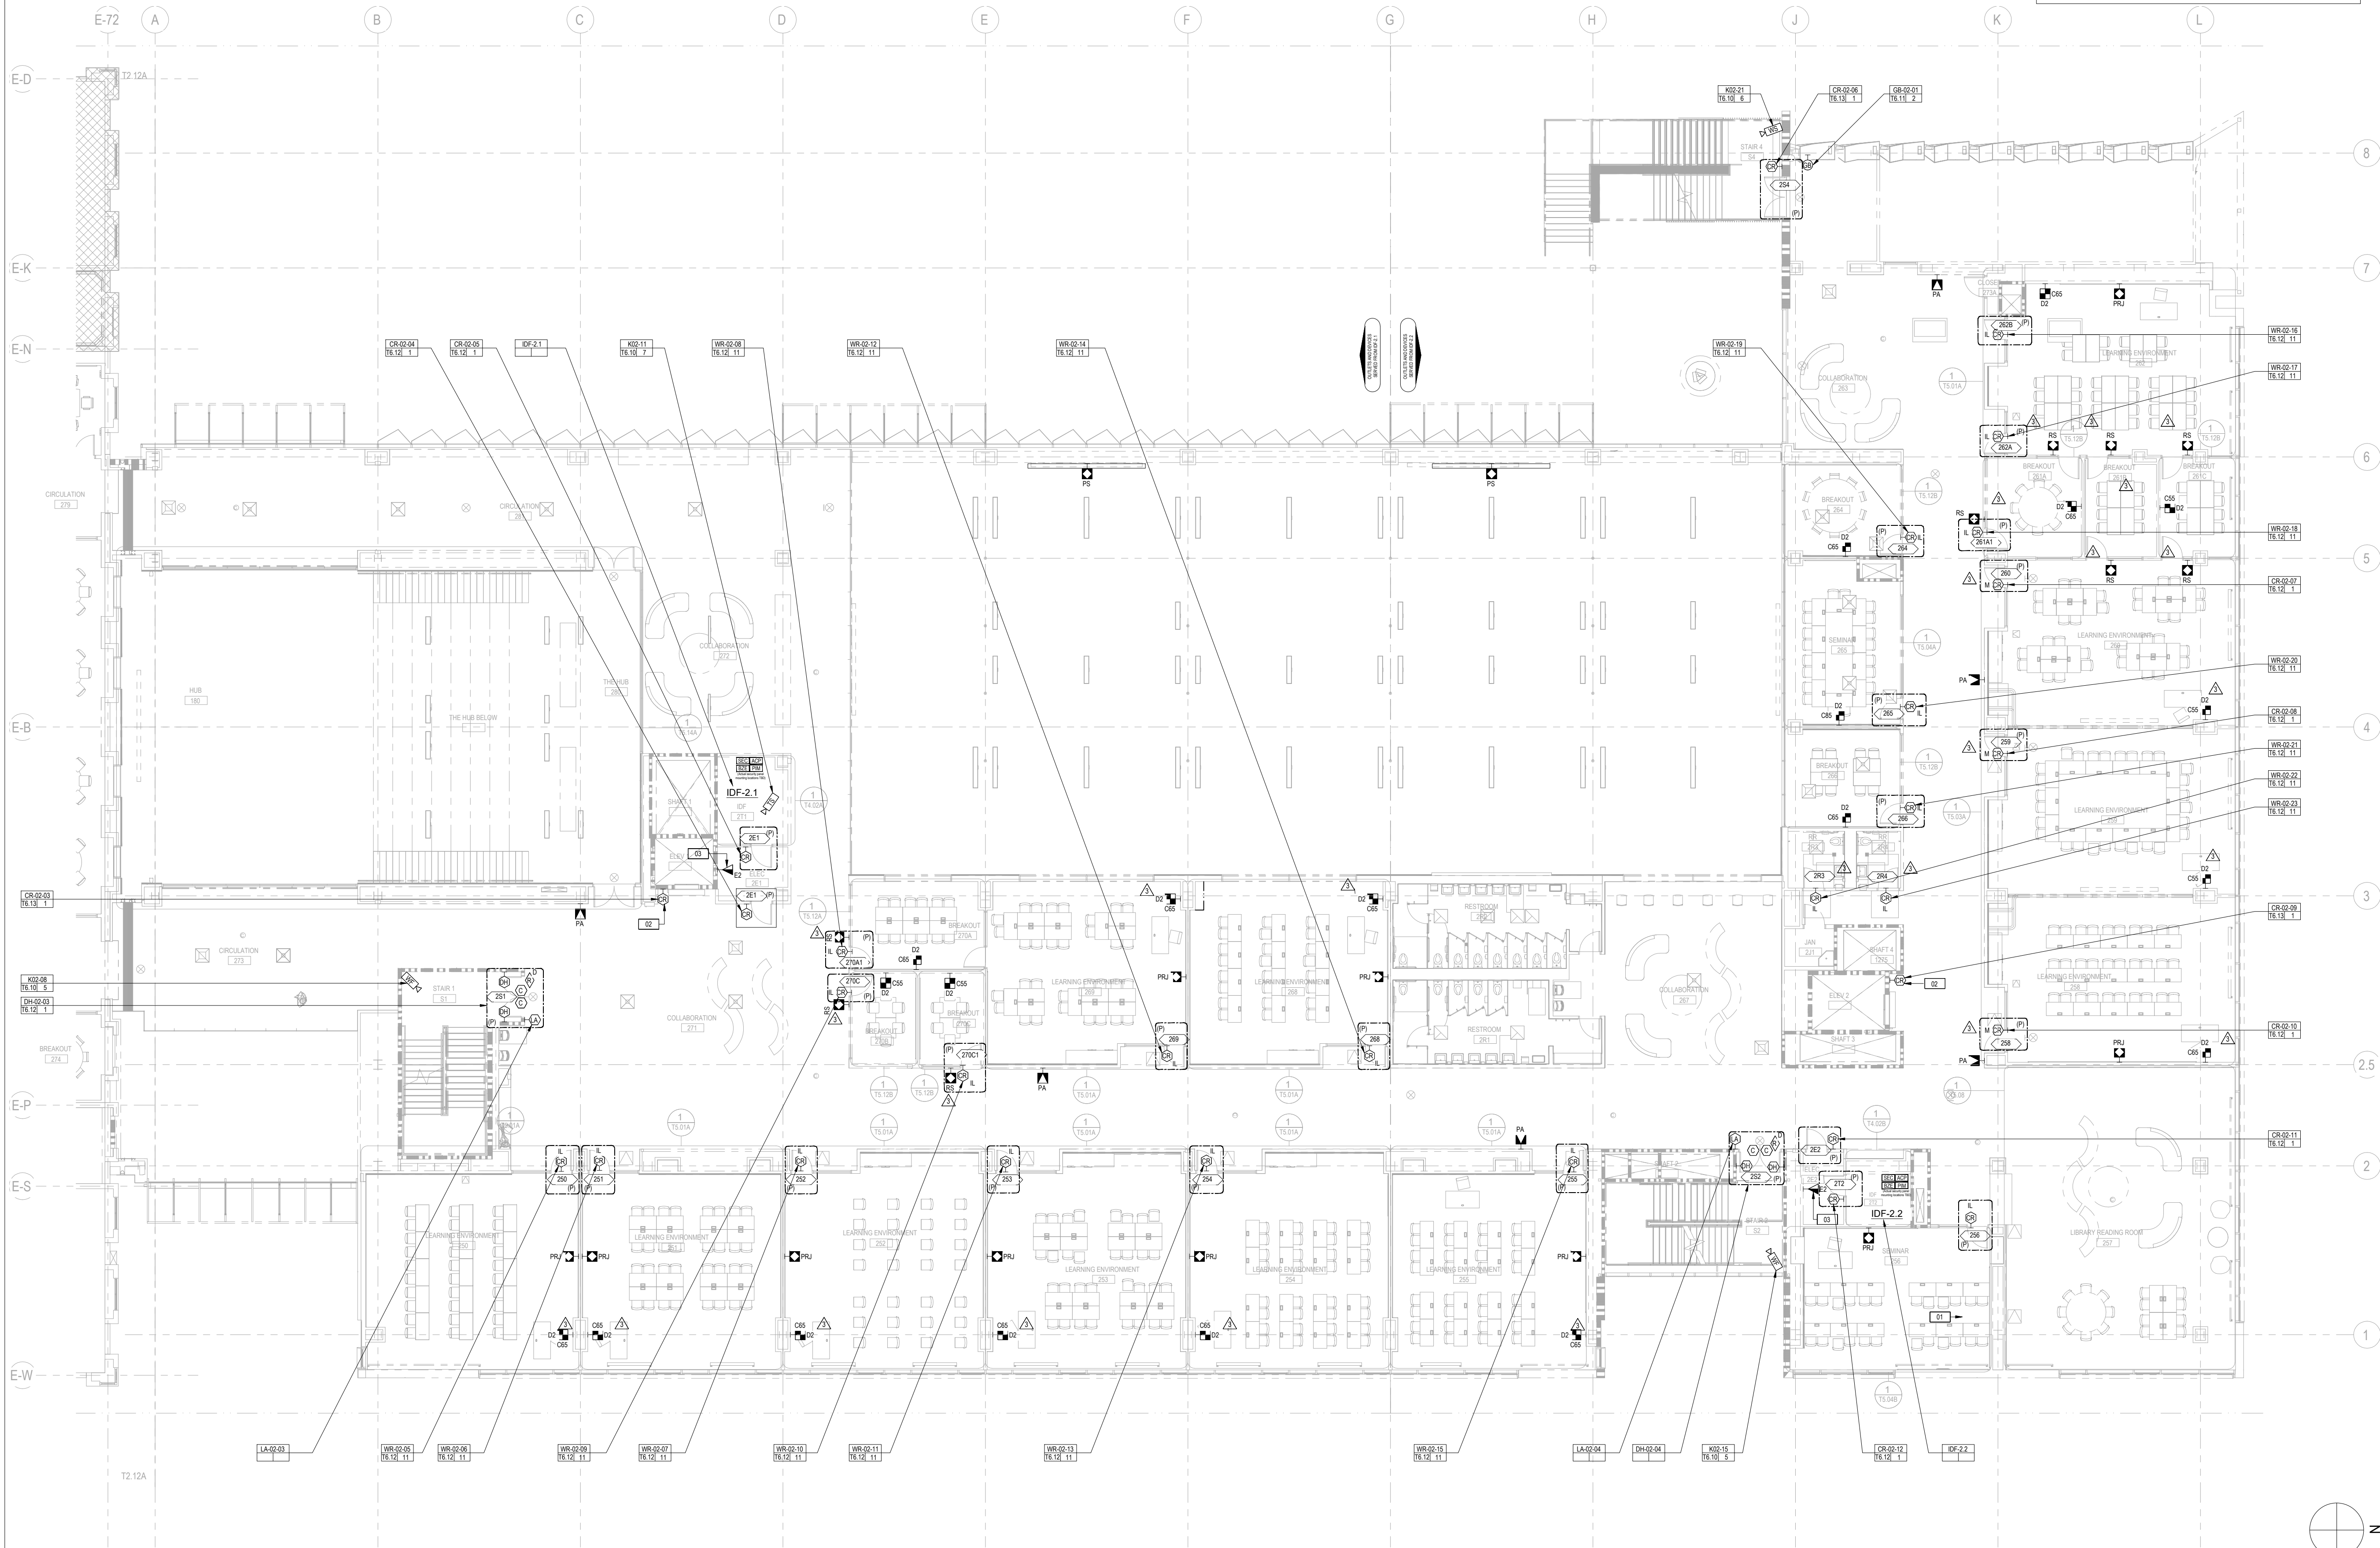

NUMBERED NOTES

- 01 INFRASTRUCTURE TO SUPPORT FUTURE PROJECTOR.
- 02 HALL CALL ELEVATOR CARD READER CONTROL.
- 03 WALL OUTLET FOR MECHANICAL CONTROLS PANEL.

SHEET NOTES

- A. REFER TO SHEET 10.01 FOR ABBREVIATIONS, GENERAL NOTES, AND SYMBOL DEFINITIONS.
- B. REFER TO SHEET 10.02 FOR PRIMARY PATHWAY REQUIREMENTS AND DEFINITIONS.
- C. REFER TO SHEET 10.03 AND 10.04 FOR OUTLETS/DEVICES SECONDARY PATHWAY AND CABLING REQUIREMENTS.
- D. SERVE OUTLETS/DEVICES ON THIS SHEET FROM TELECOM ROOMS AS NOTED.
- E. REFER TO ARCHITECTURAL PLANS FOR EXACT LOCATIONS OF OUTLETS/DEVICES, WHERE SHOWN. OUTLETS/DEVICES ON THIS SHEET ARE SHOWN DIAGRAMMATICALLY.
- F. REFER TO SECURITY INSTALLATION DETAILS FOR SECONDARY PATHWAY REQUIREMENTS, SYSTEM INTERFACES, AND COMPONENT CONFIGURATIONS.
- G. PATHWAYS SHOWN ARE DEDICATED FOR TECHNOLOGY CABLING.
- H. INSTALL SECONDARY PATHWAYS ALONG THE MOST DIRECT ROUTES TO PRIMARY PATHWAYS OR SERVING ROOM.
- I. INSTALL HORIZONTAL CABLES ALONG THE MOST DIRECT PRIMARY PATHWAY ROUTE TO THE SERVING TELECOM ROOM.
- J. PROVIDE APPROVED FIRESTOP SYSTEMS AT PENETRATIONS THROUGH FIRE BARRIERS, SMOKE BARRIERS, AND SMOKE PARTITIONS TO MAINTAIN RATINGS.
- K. PROVIDE AN ALLOWANCE OF (2) CATEGORY 6A CROPS PER 100 SQUARE FEET FOR WIRELESS ACCESS POINTS. DESIGN OF WIRELESS ACCESS POINTS TO BE COORDINATED WITH OWNERS IT DEPARTMENT.



ST. IGNATIUS COLLEGE PREPARATORY

2001 37th Ave. San Francisco, CA 94116

STAMP



TEECOM

10 California Street
Suite 100
San Francisco, CA 94111
415.397.8888
www.teecom.com

CONSULTANT LOGO

DBI STAMP

REV	DATE	DESCRIPTION
1	07/01/2024	ISSUED FOR PERMIT
2	07/01/2024	ISSUED FOR PERMIT
3	07/01/2024	ISSUED FOR PERMIT
4	07/01/2024	ISSUED FOR PERMIT
5	07/01/2024	ISSUED FOR PERMIT
6	07/01/2024	ISSUED FOR PERMIT
7	07/01/2024	ISSUED FOR PERMIT
8	07/01/2024	ISSUED FOR PERMIT

SECTOR PLAN - LEVEL 2 (NORTH)

1/8" = 1'-0"

T2.12B