


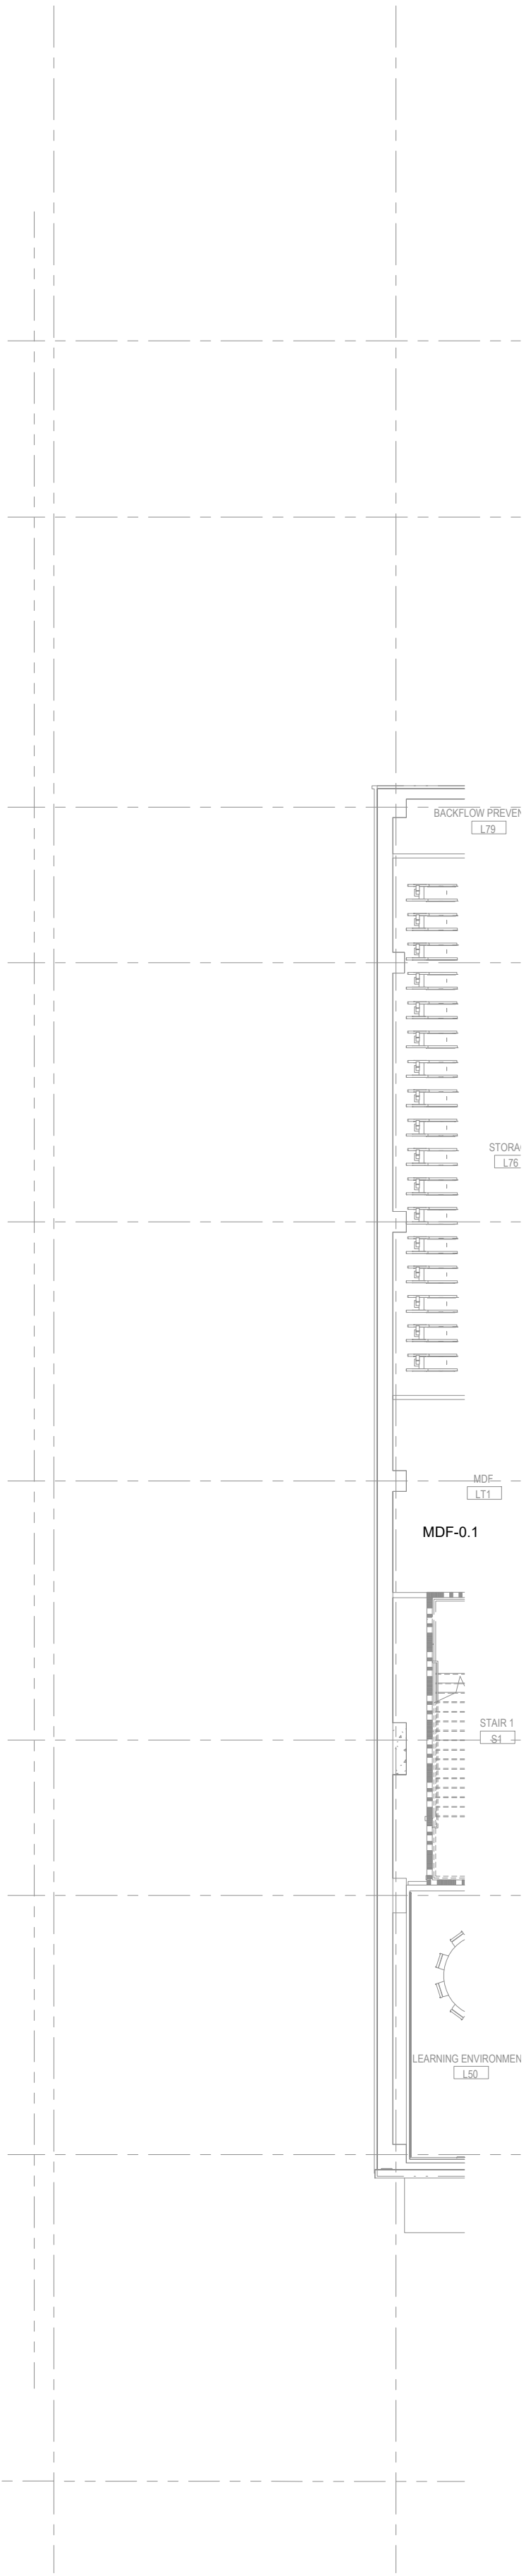

SHEET NOTES

- A. REFER TO SHEET T2.01 FOR ABBREVIATIONS, GENERAL NOTES, AND SYMBOL DEFINITIONS.
- B. REFER TO SHEET T2.02 FOR PRIMARY PATHWAY REQUIREMENTS AND DEFINITIONS.
- C. REFER TO SHEET T2.03 AND T2.04 FOR OUTLETS/DEVICES SECONDARY PATHWAY AND CABLING REQUIREMENTS.
- D. SERVE OUTLETS/DEVICES ON THIS SHEET FROM TELECOM ROOMS AS NOTED.
- E. REFER TO ARCHITECTURAL PLANS FOR EXACT LOCATIONS OF OUTLETS/DEVICES, WHERE SHOWN. OUTLETS/DEVICES ON THIS SHEET ARE SHOWN DIAGRAMMATICALLY.
- F. REFER TO SECURITY INSTALLATION DETAILS FOR SECONDARY PATHWAY REQUIREMENTS, SYSTEM INTERFACES, AND COMPONENT CONFIGURATIONS.
- G. PATHWAYS SHOWN ARE DEDICATED FOR TECHNOLOGY CABLING.
- H. INSTALL SECONDARY PATHWAYS ALONG THE MOST DIRECT ROUTES TO PRIMARY PATHWAYS OR SERVING ROOM.
- I. INSTALL HORIZONTAL CABLES ALONG THE MOST DIRECT PRIMARY PATHWAY ROUTE TO THE SERVING TELECOM ROOM.
- J. PROVIDE APPROVED FIRESTOP SYSTEMS AT PENETRATIONS THROUGH FIRE BARRIERS, SMOKE BARRIERS, AND SMOKE PARTITIONS TO MATCH RATINGS.
- K. PROVIDE AN ALLOWANCE OF (2) CATEGORY 6A DROPS PER 1000 SQUARE FEET FOR WIRELESS ACCESS POINTS. DESIGN OF WIRELESS ACCESS POINTS TO BE COORDINATED WITH OWNERS IT DEPARTMENT.

NUMBERED NOTES

- 01. WALL OUTLET DEDICATED FOR ELEVATOR PHONE LINE. COORDINATE EXACT LOCATION WITH THE ELEVATOR VENDOR.
- 02. HALL CALL ELEVATOR CARD READER CONTROL.
- 03. WALL OUTLET FOR MECHANICAL CONTROLS PANEL.
- 04. LOCATION OF CAMERA MONITOR FOR DINING ROOM.



STAMP



DB STAMP


REV	DATE	DESCRIPTION
1	05/12/2024	10% DESIGN DEVELOPMENT
2	06/12/2024	20% DESIGN DEVELOPMENT
3	07/12/2024	30% DESIGN DEVELOPMENT
4	08/12/2024	40% DESIGN DEVELOPMENT
5	09/12/2024	50% DESIGN DEVELOPMENT
6	10/12/2024	60% DESIGN DEVELOPMENT
7	11/12/2024	70% DESIGN DEVELOPMENT
8	12/12/2024	80% DESIGN DEVELOPMENT
9	01/12/2025	90% DESIGN DEVELOPMENT
10	02/12/2025	100% DESIGN DEVELOPMENT

ST. IGNATIUS COLLEGE PREPARATORY

2001 37th Ave, San Francisco, CA 94116

SECTOR FLOOR PLAN - LOWER LEVEL (SOUTH)

1/8" = 1'-0"

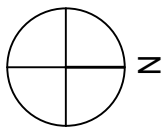

T2.10A