


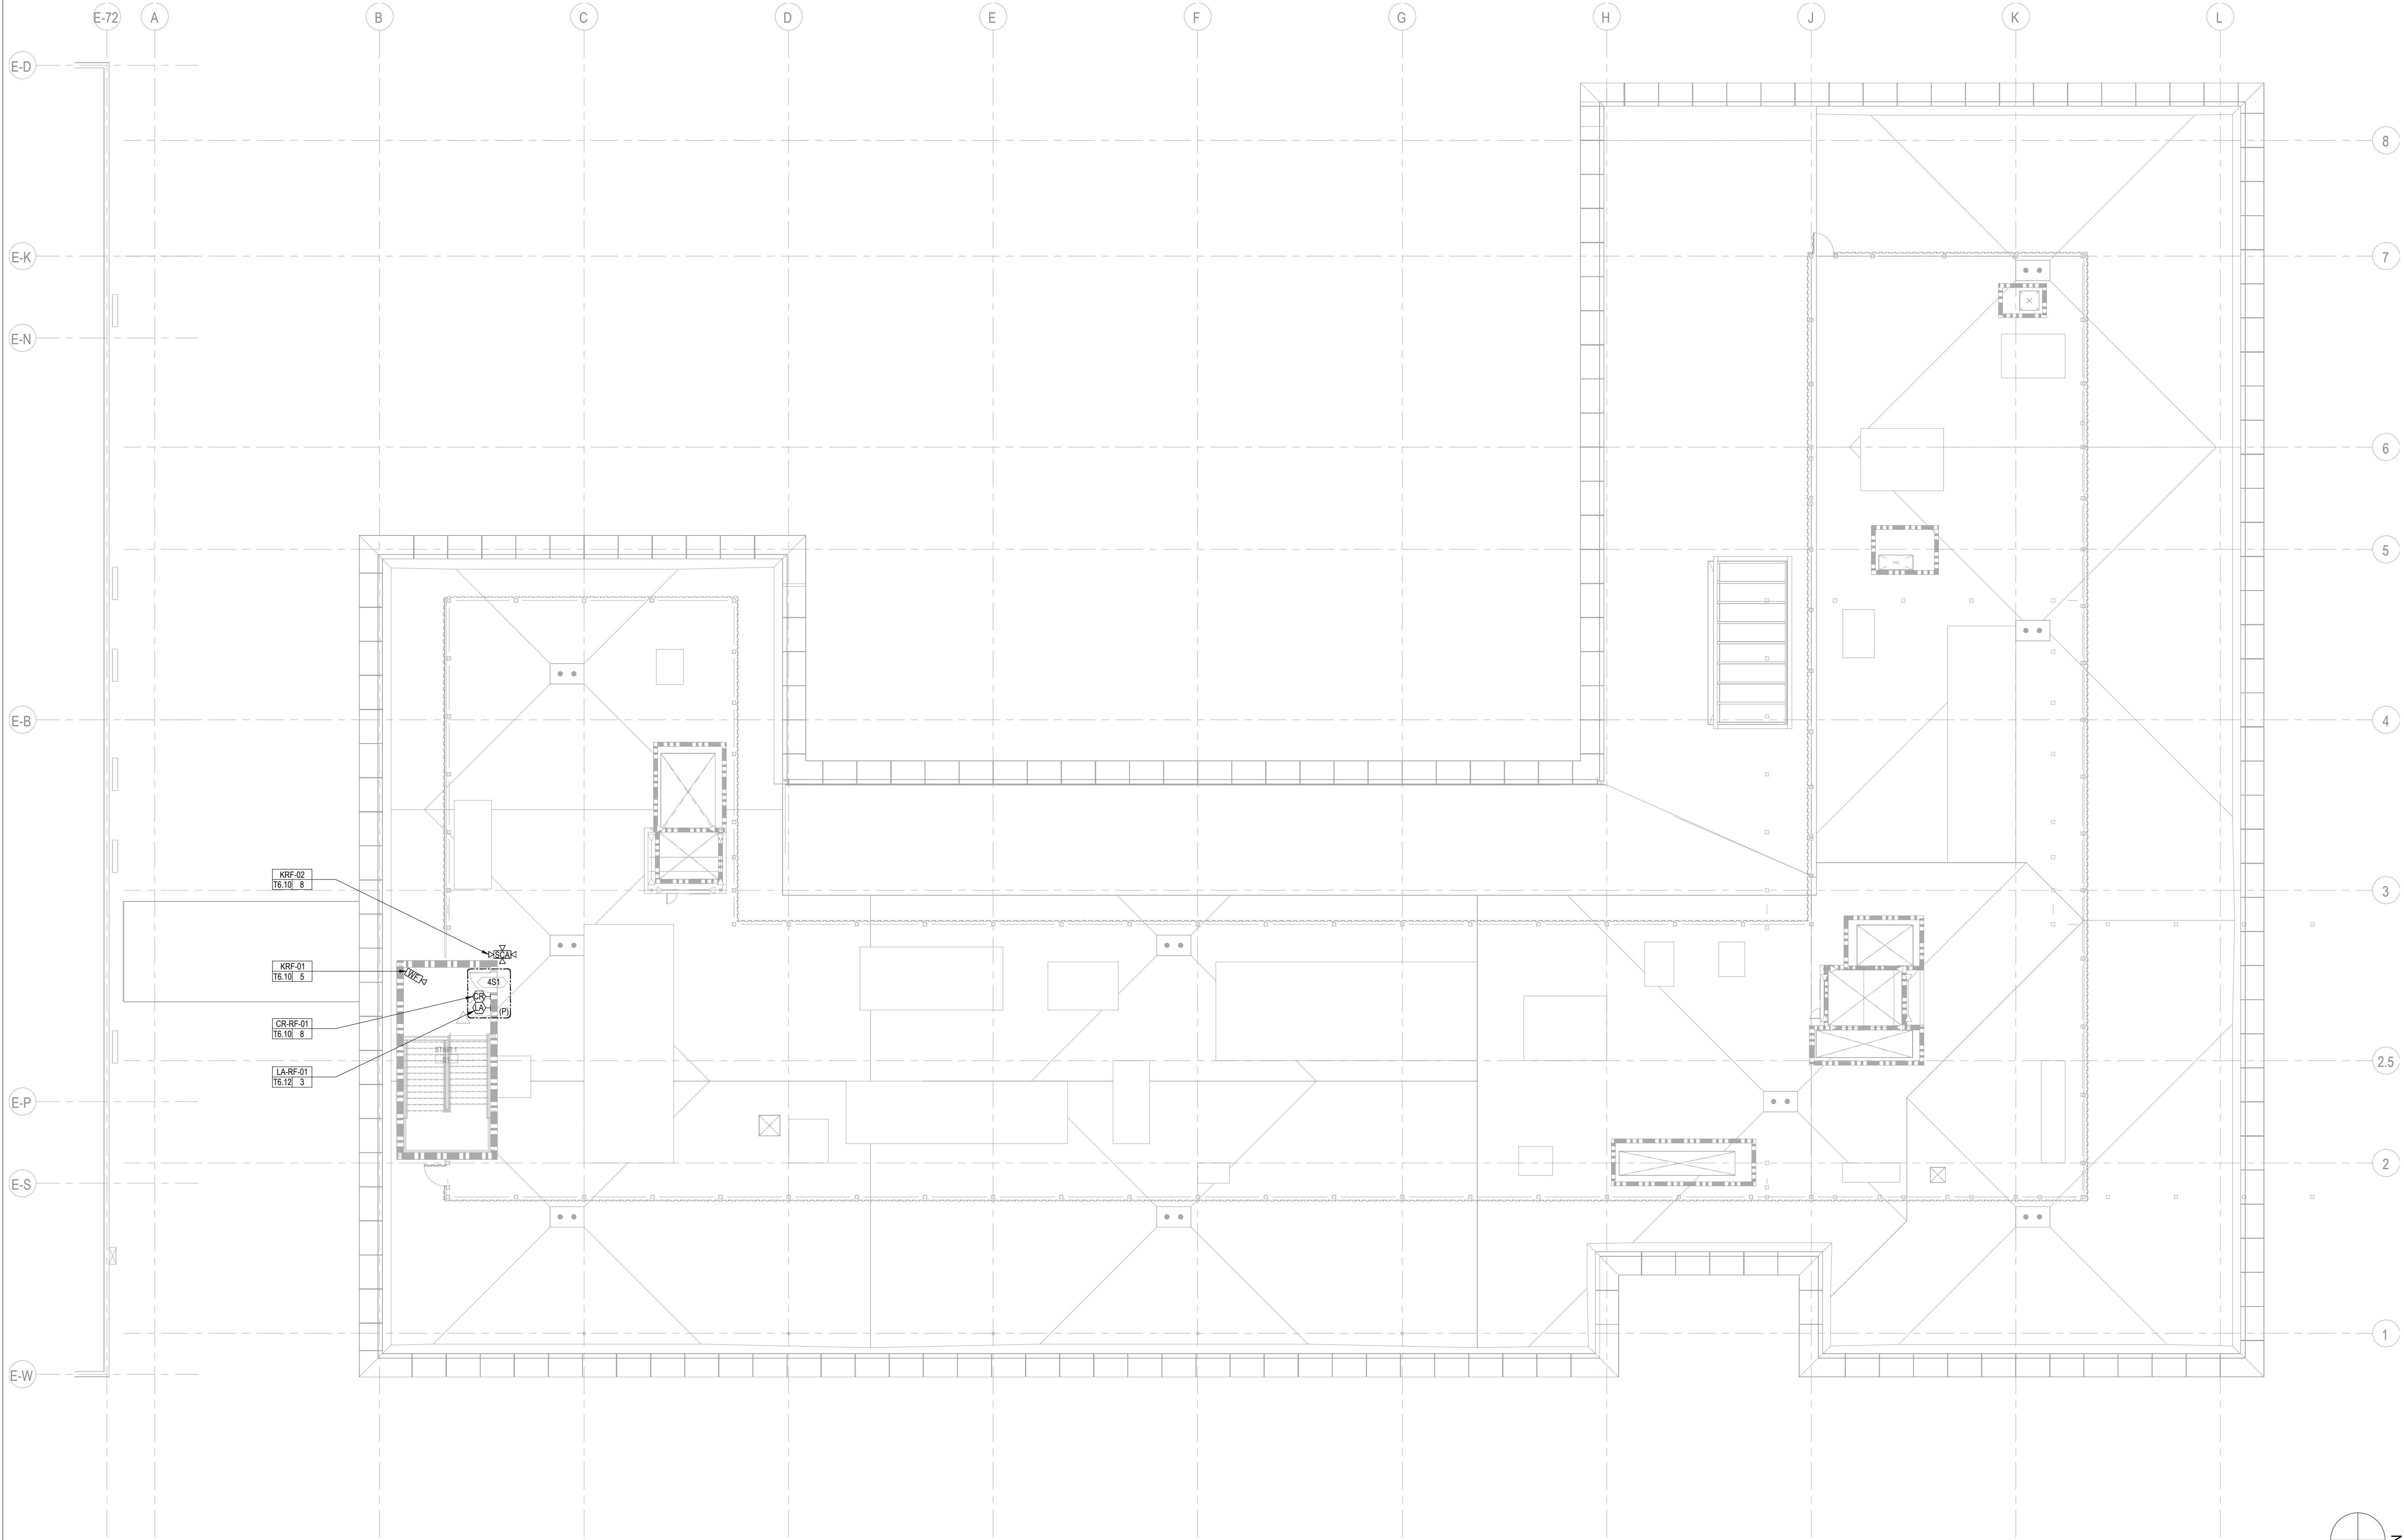

NUMBERED NOTES

- 01 WALL OUTLET DEDICATED FOR ELEVATOR PHONE LINE. COORDINATE EXACT LOCATION WITH THE ELEVATOR VENDOR.
- 02 WALL CALL ELEVATOR CARD READER CONTROL.
- 03 WALL OUTLET FOR MECHANICAL CONTROLS PANEL.
- 04 LOCATION OF CAMERA MONITOR FOR DINING ROOM.

SHEET NOTES

- A. REFER TO SHEET T2.01 FOR ABBREVIATIONS, GENERAL NOTES, AND SYMBOL DEFINITIONS.
- B. REFER TO SHEET T2.02 FOR PRIMARY PATHWAY REQUIREMENTS AND DEFINITIONS.
- C. REFER TO SHEET T2.03 AND T2.04 FOR OUTLETS/DEVICES SECONDARY PATHWAY AND CABLING REQUIREMENTS.
- D. SERVE OUTLETS/DEVICES ON THIS SHEET FROM TELECOM ROOMS AS NOTED.
- E. REFER TO ARCHITECTURAL PLANS FOR EXACT LOCATIONS OF OUTLETS/DEVICES, WHERE SHOWN. OUTLETS/DEVICES ON THIS SHEET ARE SHOWN DIAGRAMMATICALLY.
- F. REFER TO SECURITY INSTALLATION DETAILS FOR SECONDARY PATHWAY REQUIREMENTS, SYSTEM INTERFACES, AND COMPONENT CONFIGURATIONS.
- G. PATHWAYS SHOWN ARE DEDICATED FOR TECHNOLOGY CABLING.
- H. INSTALL SECONDARY PATHWAYS ALONG THE MOST DIRECT ROUTES TO PRIMARY PATHWAYS OR SERVING ROOM.
- I. INSTALL HORIZONTAL CABLES ALONG THE MOST DIRECT PRIMARY PATHWAY ROUTE TO THE SERVING TELECOM ROOM.
- J. PROVIDE APPROVED FIRESTOP SYSTEMS AT PENETRATIONS THROUGH FIRE BARRIERS, SMOKE BARRIERS, AND SMOKE PARTITIONS TO MAINTAIN RATINGS.
- K. PROVIDE AN ALLOWANCE OF (3) CATEGORY 6A DROPS PER 100 SQUARE FEET FOR WIRELESS ACCESS POINTS. DESIGN OF WIRELESS ACCESS POINTS TO BE COORDINATED WITH OWNERS IT DEPARTMENT.



STAMP



DBI STAMP

REV	DATE	DESCRIPTION
1	02/02/2024	SEALED FOR PERMIT
2	02/02/2024	SEALED FOR PERMIT
3	02/02/2024	SEALED FOR PERMIT
4	02/02/2024	SEALED FOR PERMIT
5	02/02/2024	SEALED FOR PERMIT
6	02/02/2024	SEALED FOR PERMIT
7	02/02/2024	SEALED FOR PERMIT
8	02/02/2024	SEALED FOR PERMIT

ST. IGNATIUS COLLEGE PREPARATORY

2001 37th Ave, San Francisco, CA 94116

SECTOR FLOOR PLAN - ROOF LEVEL (NORTH)

1/8" = 1'-0"

T2.14B